INDEX (ÍNDICE)

(NO. DA PAG.) SH. NO.	CONTENTS (CONTEÚDO)	REVISION NO. (NUMERO DA REVISÃO) 1	2	3	4	5	6	7	8	9
01	TITLE, NOTES, INDEX & REVISIONS (TÍTULO, OBSERVAÇÕES, ÍNDICE E REVISÕES)	☒								
01A	SYMBOLS (SÍMBOLOS)	☒								
02	TRACK & SIGNAL PLAN (PLANO DE VIA E SINAL COM CABOS)	☒								
02A	CABLE PLACEMENT LAYOUT (ESQUEMA DE COLOCAÇÃO DE CABOS)	☒								
03	ELECTROLOGIXS PROGRAM (PROGRAMA DO ELECTROLOGIXS)	☒								
04	ELECTROLOGIXS PTC PROGRAM (PROGRAMA PTC DO ELECTROLOGIXS)	☒								
05	OFFICE CONTROL & INDICATION EQUIVALENT CIRCUITS (CIRCUITOS DE CONTROLE E INDICAÇÃO DO CCO)	☒								
06	POWER DISTRIBUTION (DISTRIBUIÇÃO DE ENERGIA)	☒								
07	ELECTROLOGIXS MODULE CONFIGURATION (CONFIGURAÇÃO DO MÓDULO ELECTROLOGIXS)	☒								
08	ELECTROLOGIXS COMMUNICATION CIRCUITS (CIRCUITOS DE COMUNICAÇÃO DO ELECTROLOGIXS)	☒								
09	TRACK CIRCUITS (CIRCUITOS DE VIA)	☒								
10	ELECTROLOGIXS TRACK AND VITAL I/O (I/O DE VIA E VITAL DO ELECTROLOGIXS)	☒								
11	SIGNALS 2D, 2E & 4E LIGHTING CIRCUITS (CIRCUITOS DOS SINAIS 2D, 2E E 4E)	☒								
12	ELECTROLOGIXS I/O CIRCUITS (CIRCUITOS I/O DO ELECTROLOGIXS)	☒								
13	SWITCH CIRCUITS (CIRCUITOS DA MÁQUINA DE CHAVE)	☒								
14	LOCAL CONTROL PANEL LAYOUT (LAYOUT DO PAINEL DE CONTROLE LOCAL)	☒								
15	LOCAL CONTROL PANEL & EXPANSION PANELS (PAINEL DE CONTROLE LOCAL E EXPANSÕES)	☒								
16	LOCAL CONTROL PANEL & EXPANSION PANEL I/O CARDS (MODULOS DO PAINEL DE CONTROLE LOCAL E EXPANSÕES)	☒								
17	6'X 6' HOUSE LAYOUT "D" WALL (HOUSE 6'X 6' LAYOUT DA PAREDE "D")	☒								
18	6'X 6' HOUSE LAYOUT "A" WALL (HOUSE 6'X 6' LAYOUT DA PAREDE "A")	☒								
19	6'X 6' HOUSE LAYOUT "B" WALL (HOUSE 6'X 6' LAYOUT DA PAREDE "B")	☒								
20	6'X 6' HOUSE LAYOUT "C" WALL (HOUSE 6'X 6' LAYOUT DA PAREDE "C")	☒								
21	TERMINAL BOARD DETAIL (DETALHE DO PAINEL DE TERMINAIS [TB])	☒								

☒ = DESIGN COMPLETED (DESIGN COMPLETADO)
























☒ = REVISION COMPLETED (REVISÃO COMPLETADA)

REVISIONS (REVISÕES)

REV. NO.	PROJECT NO.	DESIGN DATE	IN SERVICE DATE	REVISION DATE
NO.DA REV	NO. DO PROJETO	DATA DO DESIGN	DATA DO AS BUILT	DATA DA REVISÃO
1	MRS1026503	24–MAY–11	30–MAY–11	22–JUN–11


MRS LOGISTICA S.A.

DESCRIÇÃO:	TÍTULO, OSERVAÇÕES, ÍNDICE E REVISÕES		
LOCAÇÃO:	P2–04A (1)		
DESIGN POR:	XORAIL	REVISÃO: 1	DATA: 22–JUN–11
CAD POR:	XORAIL	ARQUIVO:	EE–SD–FA–0FIN–116.01

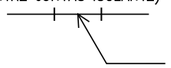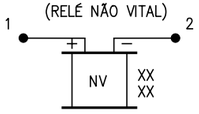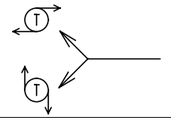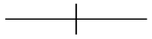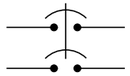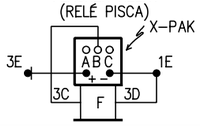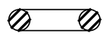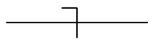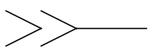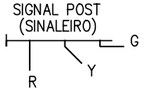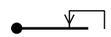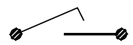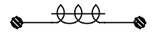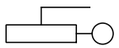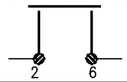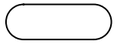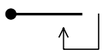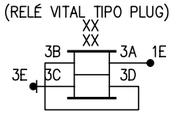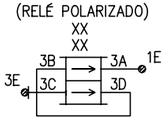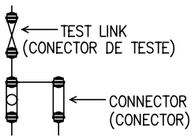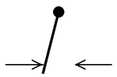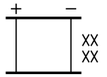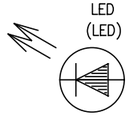TRACK CIRCUIT BETWEEN INSULATED JOINTS (CIRCUITO DE VIA ENTRE JUNTAS ISOLANTE) 	TWISTED PAIR CABLE (CABO DE PAR TRANÇADO) 	HEAVY DUTY RELAY CONTACT (CONTATO DE ALTA CORRENTE) 	NON VITAL RELAY (RELÉ NÃO VITAL) 	TEST LINK (CONECTOR DE TESTE) 	TWISTED PAIR (PAR TRANÇADO) 			
INSULATED JOINT (JUNTA ISOLANTE) 	ELECTRICAL CONTACTOR (DISJUNTOR ELÉTRICO) 	HEAVY DUTY MAGNETIC BLOWOUT RELAY CONTACT (CONTATO DE ALTA CORRENTE MAGNÉTICO) 	FLASHER RELAY (RELÉ PISCA) 	CONNECTOR (CONECTOR) 	AC POWER DROP (FONTE DE ENERGIA AC) 			
END JOINT (JUNTA DE FIM DE SINALIZAÇÃO) 	SINGLE POLE SWITCH (INTERRUPTOR DE PÓLO ÚNICO) 	MOTOR CONTROL CONTACTS (CONTATO DE OPERAÇÃO DE MÁQUINA DE CHAVE) 	TOGGLE SWITCH (INTERRUPTOR TOGGLE) 	INTERFACE CONNECTOR (CONECTOR DE INTERFACE) 	MOTOR (MOTOR) 			
SIGNAL POST (SINALEIRO)  R=RED (VERMELHO) Y=YELLOW (AMARELO) G=GREEN (VERDE)	ENERGIZED FRONT CONTACT (CONTATO FRONT ENERGIZADO) 	HAND THROW CIRCUIT CONTACT (CONTATO DE OPERAÇÃO MANUAL DE MÁQUINA DE CHAVE) 	LIGHTNING ARRESTER (PÁRA–RAIOS) 	GROUND (TERRA) 	FIXED IMPEDANCE WITH IRON CORE (IMPEDÂNCIA FIXA COM NÚCLEO DE FERRO) 			
DUAL CONTROL POWER SWITCH (MÁQUINA DE CHAVE ELÉTRICA) 	DE–ENERGIZED FRONT CONTACT (CONTATO FRONT DESENERGIZADO) 	OPEN SWITCH CIRCUIT CONTROLLER CONTACT (CONTATO DO CIRCUITO DE INDICAÇÃO DA MAQUINA DE CHAVE) 	EQUALIZER (EQUALIZADOR) 	NOTES (ANOTAÇÕES) 	VARIABLE RESISTOR (RESISTOR VARIÁVEL) 			
HAND THROW SWITCH WITH ELECTRIC LOCK (MÁQUINA DE CHAVE COM TRAVADOR ELÉTRICO) 	ENERGIZED BACK CONTACT (CONTATO BACK ENERGIZADO) 	VITAL RELAY PLUG TYPE (RELÉ VITAL TIPO PLUG) 	TERMINAL (TERMINIAS) 	DIODE (DIODO) 	5 OHM FIXED RESISTOR (5 OHM RESISTOR FIXO) 			
SHADED ARROW SHOWS NORMAL ALIGNMENT (AMV; SETA SOMBREADA MOSTRA O ALINHAMENTO NORMAL) 	DE–ENERGIZED BACK CONTACT (CONTATO BACK DESENERGIZADO) 	BIASED RELAY (RELÉ POLARIZADO) 	TEST LINK (CONECTOR DE TESTE) CONNECTOR (CONECTOR) 	LAMP, LED MAY BE G, Y, OR R IN COLOR (LAMP, LED PODE SER G, Y, OU R) 				
HOUSE, DIMENSION USUALLY SHOWN ON PLAN AS 4'X 4', 6'X 6', 8'X 6' ETC. (HOUSE, DIMENSÃO GERALMENTE MOSTRADO NO PLANO COM 4'X 4', 6'X 6', 8'X 6' ETC.) 	POLAR CONTACT (CONTATO POLAR) 	VITAL RELAY SHELF TYPE (RELÉ VITAL TIPO DE PRATELEIRA) 	TERMINAL POST (TERMINAIS) 	LED (LED) 				

MRS LOGISTICA S.A.

DESCRIÇÃO:	SÍMBOLOS		
LOCAÇÃO:	P2–04A (1)		
DESIGN POR:	XORAIL	REVISÃO: 1	DATA: 22–JUN–11
CAD POR:	XORAIL	ARQUIVO:	EE–SD–FA–0FIN–116.01A

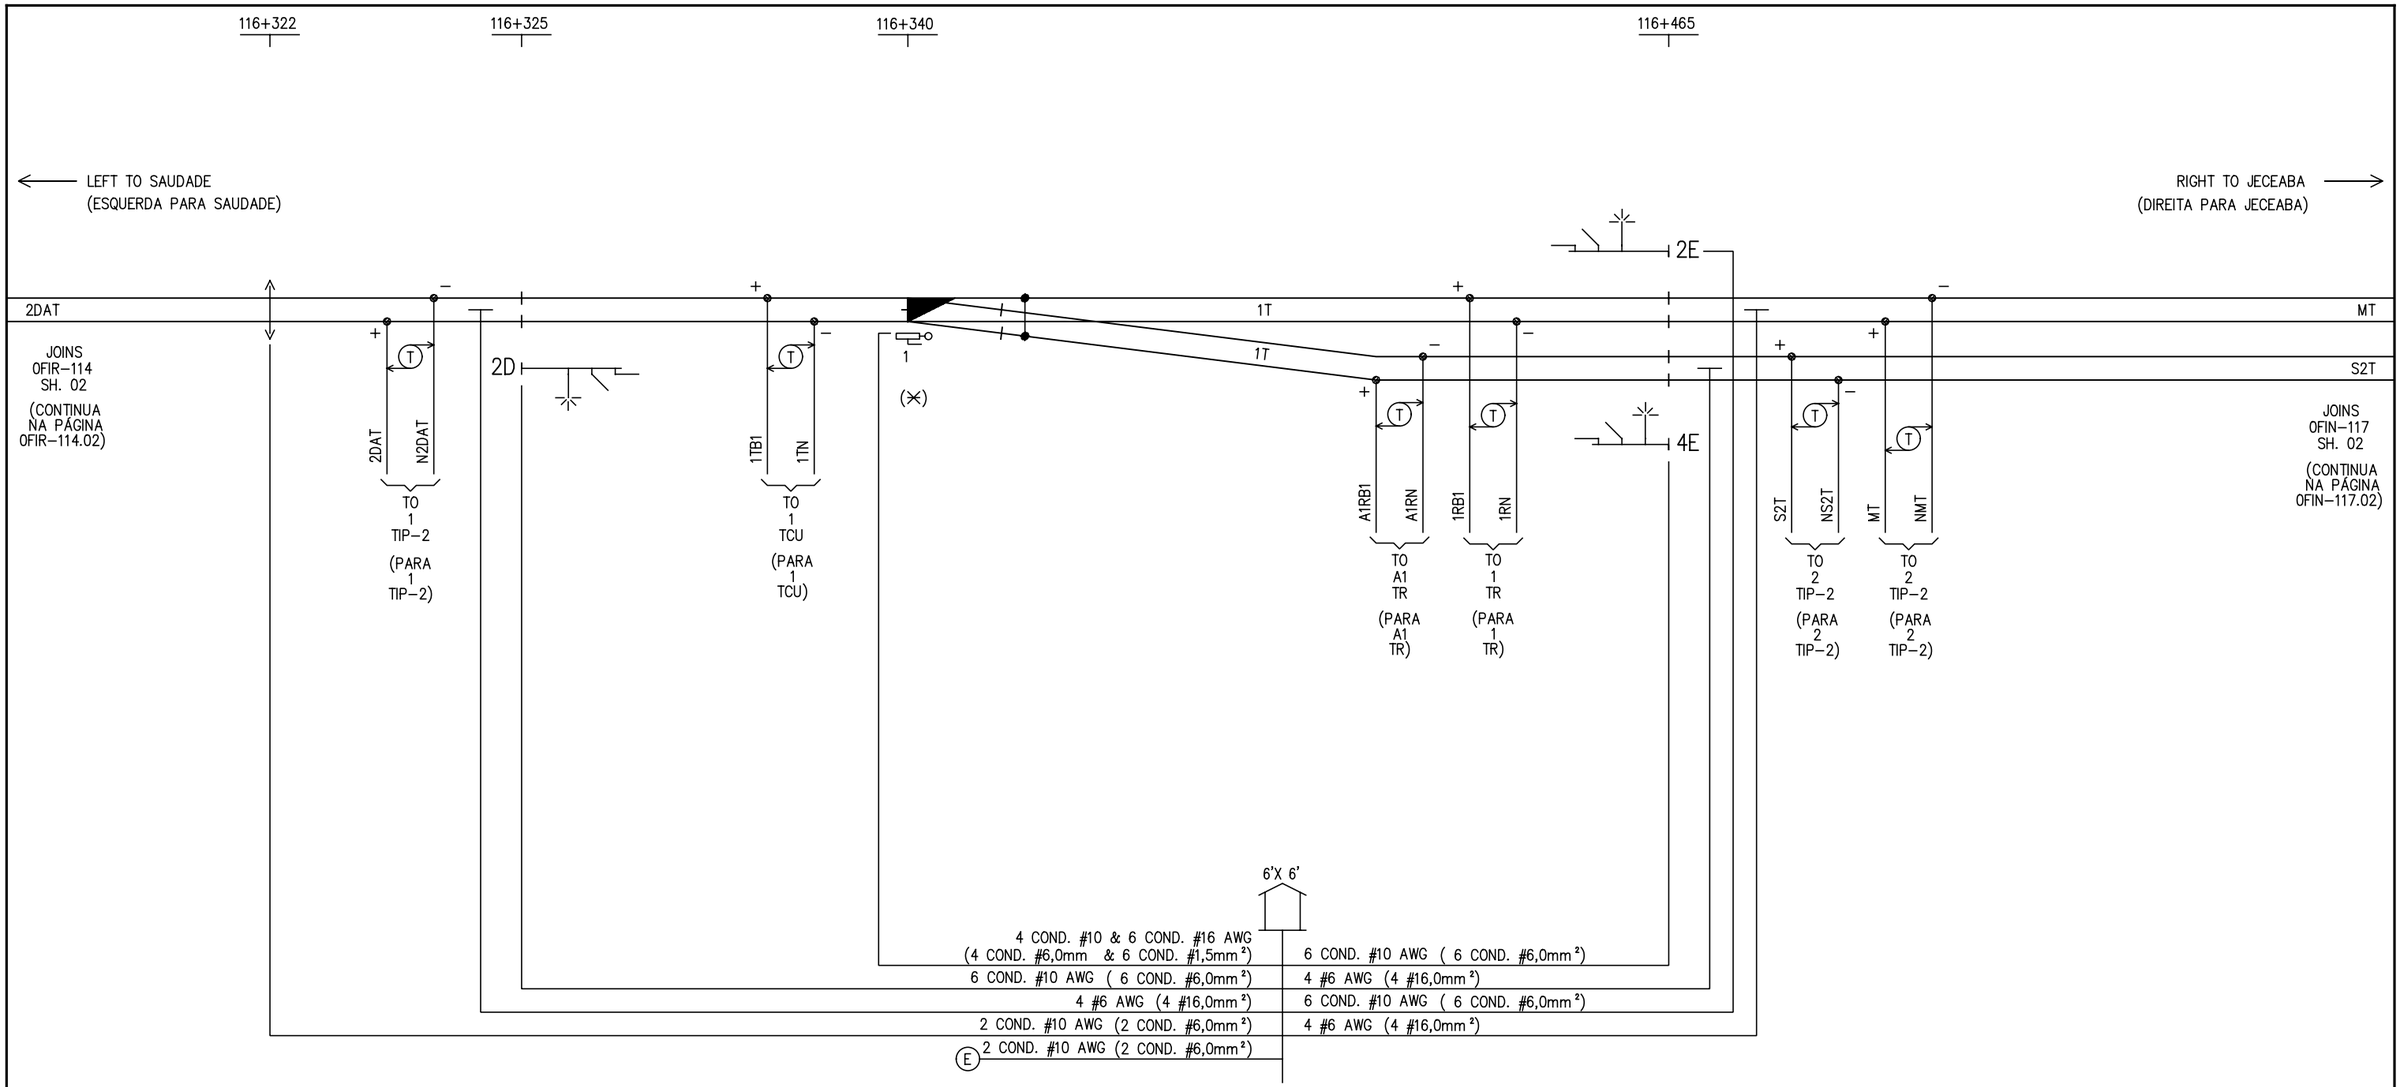

NOTES (ANOTAÇÕES):

1. (✕) = LOCATION OF HOUSE (LOCALIZAÇÃO DA HOUSE)

MRS LOGISTICA S.A.


DESCRIÇÃO:	PLANO DE VIA E SINAL COM CABOS		
LOCAÇÃO:	P2–04A (1)		
DESIGN POR: XORAIL	REVISÃO: 1	DATA: 22–JUN–11	
CAD POR: XORAIL	ARQUIVO: EE–SD–FA–0FIN–116.02		

LOCATION P2–04A (1)

116+322 | 116+325 | 116+340 | 116+465

← LEFT TO SAUDADE
(ESQUERDA PARA SAUDADE)

RIGHT TO JECEABA →
(DIREITA PARA JECEABA)

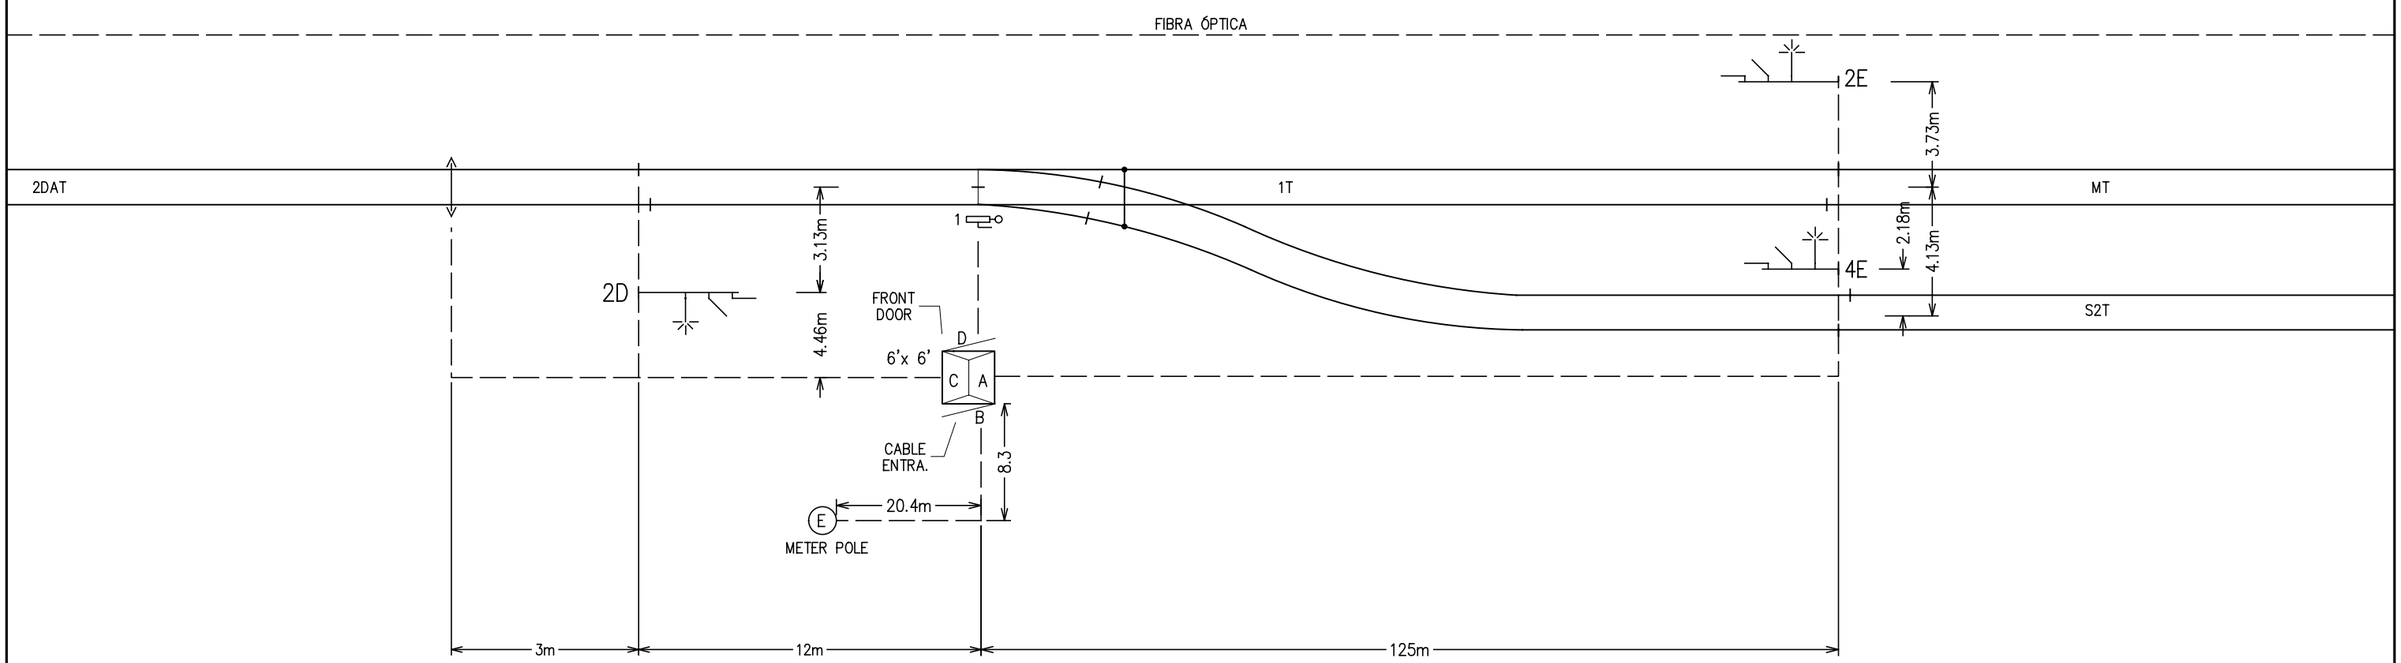

NOTES (OBSERVAÇÕES):

1. DESIGN NOT TO SCALE (PROJETO PARA NÃO ESCALA)

MRS LOGISTICA S.A.

DESCRIÇÃO:	ESQUEMA DE COLOCAÇÃO DE CABOS		
LOCAÇÃO:	P2–04A (1)		
DESIGN POR:	XORAIL	REVISÃO: 1	DATA: 22–JUN–11
CAD POR:	XORAIL	ARQUIVO:	EE–SD–FA–0FIN–116.02A

OFFICE SETTINGS
(CONFIGURAÇÃO)

ITEM (ITEM)	SETTING (CONFIGURAÇÃO)
SITE ID (ID DO SITE)	UNDEFINED (INDEFINIDO)
CHASSIS ID (ID DO CHASSI)	40

VITAL APPLICATION INFORMATION
(INFORMAÇÕES DO APLICATIVO VITAL)

ITEM (ITEM)	SETTING (CONFIGURAÇÃO)
NAME (NOME)	004A_116340V
INDEX (INDICE)	001
EPT CRC	5158
EPT CHECKSUM	F071

NON–VITAL APPLICATION INFORMATION
(INFORMAÇÕES DO APLICATIVO NÃO VITAL)

ITEM (ITEM)	SETTING (CONFIGURAÇÃO)
NAME (NOME)	004A_116340NV
INDEX (INDICE)	001
EPT CRC	D200
EPT CHECKSUM	4DCE

GENESYS SETUP AND
IP CONFIGURATION INFORMATION
(CONFIGURAÇÃO DO PROTOCOLO GENESYS E IP)

ITEM (ITEM)	SETTING (CONFIGURAÇÃO)
STATION NAME (NOME DA ESTAÇÃO)	P2–04A (1)
GENESYS ADDRESS (ENDEREÇO DO GENESYS)	11
UDP PORT	10011
SUBNET	192.168.151.176
SUBNET MASK	255.255.255.240
GATEWAY	192.168.151.177
CTC GENESYS IP	192.168.151.178

CIO–1A DIAGNOSTIC PORT SETTINGS
(CONFIGURAÇAO DA PORTA DIAGNOSTICA CIO–1A)

ITEM (ITEM)	SETTING (CONFIGURAÇÃO)	
BAUD RATE (TAXA DE BAUDE)	57600	✳
PARITY (PARIDADE)	NONE (NENHUM)	✳
DATA BITS (BITS DE DADOS)	8	✳
STOP BITS (BITS DE PARADA)	1	✳
FLOW CONTROL (CONTROLE DE FLUXO)	DISABLED (INVÁLIDO)	✳

VITAL TIMERS
(TEMPORIZADORES VITAL)

NAME (NOME)	SETTING (CONFIGURAÇÃO)	
2DTER LSR TIMER (TEMPORIZADOR 2DLSR)	3 MIN 14 SEC (SEG.)	✳
2ETER LSR TIMER (TEMPORIZADOR 2ELSR)	3 MIN 14 SEC (SEG.)	✳
4ETER LSR TIMER (TEMPORIZADOR 4ELSR)	3 MIN 14 SEC (SEG.)	✳

VITAL CONFIGURATION SETUP
(CONFIGURAÇÃO VITAL)

#	NAME (NOME)	STATE (ESTADO)
1	BLK CLR SET (BLOCO LIVRE CONF.)	FALSE (FALSA)

VITAL SELECT SHUNTS
(CONFIGURAÇÃO SHUNTS VITAL)

#	NAME (NOME)	STATE (ESTADO)
1	BLK CLR DIP (BLOCO LIVRE DIP)	INTACT (INTACTO)

NOTES (OBSERVAÇÕES):

✳ = STATUS SET/CHANGED USING THE CDU–1
ALL OTHERS SET USING THE ACE PROGRAM.
(STATUS ESTABELECIDOS/MODIFICADO USANDO O CDU–1. OS OUTROS SÃO MODIFICADOS USANDO O PROGRAMA ACE.)

MRS LOGISTICA S.A.

DESCRIÇÃO:	PROGRAMA DO ELECTROLOGIXS		
LOCAÇÃO:	P2–04A (1)		
DESIGN POR:	XORAIL	REVISÃO: 1	DATA: 22–JUN–11
CAD POR:	XORAIL	ARQUIVO:	EE–SD–FA–0FIN–116.03

GETS ELECTROLOGIXS WIU SETUP	
LOCATION NAME: P2-04A(1 SWITCH)	
GENERAL ETHERNET SETTINGS	
ETHERNET PORT 1	
IP ADDRESS	10.100.1.1
SUBNET MASK	255.255.255.0
ETHERNET PORT 2	
IP ADDRESS	10.200.1.1
SUBNET MASK	255.255.255.0
ELX APPLICATION DATA	
APPLICATION NAME	004A_116340
APPLICATION REV.	1.0
APP. CHECKSUM/CRC	724F/375A
PTC APPLICATION DATA	
APPLICATION NAME	XXXXX
APPLICATION REV.	1.0
APPLICATION CRC	XXXX/XXXX

GENERAL WIU SETTINGS	
WIU ADDRESS	7.RRR.LLL.GGG.SS
ENCRYPTED HMAC KEY	0X12345678123456781234567812345678123456781234567812345678
CONTINUOUS BEACON	FALSE
BEACON RATE	1000 MSEC (1 SEC)
BEACON BIT TIME	300 SEC
BEACON END TIME	120 SEC
MAX BEACON INTERVAL	900 SEC (15 MIN)
BEACON ON CHANGE	TRUE
EMP SETTINGS	
SOURCE ADDRESS	RR.W.LLL.GGG.SS:WIU
DESTINATION ADDRESS	TBD
TTL (TIMED BEACON)	12 SEC
QOS (TIMED BEACON)	1
TTL (RESPONSE TO GET WIU STATUS)	12 SEC
QOS (RESPONSE TO GET WIU STATUS)	1
CLASS D SETTINGS	
DESTINATION IP ADDRESS	10.255.255.210
DESTINATION IP PORT	3001
LOG TRAFFIC	FALSE
KEEP ALIVE INTERVAL	30000 MSEC (30 SEC)
KEEP ALIVE ACK TIMEOUT	25000 MSEC (25 SEC)
DATA ACK ENABLED	TRUE
CONNECTION TIMEOUT	30000 MSEC (30 SEC)
CONNECTION DELAY	60000 MSEC (60 SEC)
NAK RETRY LIMIT	3
CONNECTION RETRY LIMIT	3
RECONNECT RETRY LIMIT	3

MRS LOGISTICA S.A.

DESCRIÇÃO:	PROGRAMA PTC DO ELECTROLOGIXS		
LOCAÇÃO:	P2-04A (1)		
DESIGN POR:	XORAIL	REVISÃO: 1	DATA: 22-JUN-11
CAD POR:	XORAIL	ARQUIVO:	EE-SD-FA-0FIN-116.04

INDICATIONS (INDICAÇÕES)

1NWK = 1 NORMAL SWITCH INDICATION	(1NWK = MAQUINA DE CHAVE 1 NORMAL)
1RWK = 1 REVERSE SWITCH INDICATION	(1RWK = MAQUINA DE CHAVE 1 REVERSA)
1LK = 1 SWITCH LOCK INDICATION	(1LK = MAQUINA DE CHAVE 1 LOCKED)
1WCBPK = 1 SWITCH BACKCHECK INDICATION	(1WCBPK = MAQUINA DE CHAVE 1 BACKCHECK INDICAÇÃO)
1WLPK = 1 SWITCH HAND THROW INDICATION	(1WLPK = MAQUINA DE CHAVE 1 EM MANUAL)
2DGZK = 2D SIGNAL REQUEST INDICATION	(2DGZK = SINAL 2D REQUISIÇÃO INDICAÇÃO)
2DGK = 2D SIGNAL INDICATION	(2DGK = SINAL 2D INDICAÇÃO)
2EGZK = 2E SIGNAL REQUEST INDICATION	(2EGZK = SINAL 2E REQUISIÇÃO INDICAÇÃO)
2EGK = 2E SIGNAL INDICATION	(2EGK = SINAL 2E INDICAÇÃO)
4EGZK = 4E SIGNAL REQUEST INDICATION	(4EGZK = SINAL 4E REQUISIÇÃO INDICAÇÃO)
4EGK = 4E SIGNAL INDICATION	(4EGK = SINAL 4E INDICAÇÃO)
2D–2E–4E TEK = SIGNAL IN TIME INDICATION	(2D–2E–4E TEK = SINAL NO TEMPO INDICAÇÃO)
2DBCK = 2D BLOCK CLEAR INDICATION	(2DBCK = BLOCO LIVRE 2D)
2DBCGK = 2D BLOCK CLEAR SIGNAL INDICATION	(2DBCGK = INDICAÇÃO BLOCO LIVRE SINAL 2D)
2EBCK = 2E BLOCK CLEAR INDICATION	(2EBCK = BLOCO LIVRE 2E)
2EBCGK = 2E BLOCK CLEAR SIGNAL INDICATION	(2EBCGK = INDICAÇÃO BLOCO LIVRE SINAL 2E)
4EBCK = 4E BLOCK CLEAR INDICATION	(4EBCK = BLOCO LIVRE 4E)
4EBCGK = 4E BLOCK CLEAR SIGNAL INDICATION	(4EBCGK = INDICAÇÃO BLOCO LIVRE SINAL 4E)
1TK = DETECTOR TRACK INDICATION	(1TK = SEÇÃO DETECTORA)
2DAK = 2D APPROACH TRACK INDICATION	(2DAK = VIA DE APROXIMAÇÃO 2D)
2DBK = 2D ADVANCE APPROACH TRACK INDICATION	(2DBK = VIA AVANÇADA DE APROXIMAÇÃO 2D)
MAK = MAIN TRACK INDICATION	(MAK = INDICAÇÃO LINHA PRINCIPAL)
S2AK = SIDING 2 TRACK INDICATION	(S2AK = INDICAÇÃO LINHA SECUNDARIA 2)
1TBK = DETECTOR TRACK BLOCK INDICATION	(1TBK = SEÇÃO DETECTORA BLOQUEADA)
1SBK = 1 SWITCH BLOCK INDICATION	(1SBK = MAQUINA DE CHAVE 1 BLOQUEADA)
2DTBK = 2D TRACK BLOCK INDICATION	(2DTBK = VIA DE APROXIMAÇÃO 2D BLOQUEADA)
2ETBK = 2E TRACK BLOCK INDICATION	(2ETBK = VIA DE APROXIMAÇÃO 2E BLOQUEADA)
4ETBK = 4E TRACK BLOCK INDICATION	(4ETBK = VIA DE APROXIMAÇÃO 4E BLOQUEADA)
DOOR ALRMK = DOOR ALARM INDICATION	(DOOR ALRMK = ALARME DE PORTA)
DD1K = DERAIL DETECTOR TRACK 1 INDICATION	(DD1K = DETECTOR DE DESCARRILHAMENTO 1)
DD2K = DERAIL DETECTOR TRACK 2 INDICATION	(DD2K = DETECTOR DE DESCARRILHAMENTO 2)
POK = POWER OFF INDICATION	(POK = FALTA DE ENERGIA)
MOK = MANUAL OPERATE INDICATION	(MOK = OPERAÇÃO EM MANUAL)
2DLOK = 2D SIGNAL LAMP OUT INDICATION	(2DLOK = LAMPADA QUEIMADA 2D)
2ELOK = 2E SIGNAL LAMP OUT INDICATION	(2ELOK = LAMPADA QUEIMADA 2E)
4ELOK = 4E SIGNAL LAMP OUT INDICATION	(4ELOK = LAMPADA QUEIMADA 4E)
BLKPOK = BLOCK POWER OUT INDICATION	(BLKPOK = FALTA DE ENERGIA NO BLOCO)
HEALTHK = ELGX MODULE FAILURE	(HEALTHK = FALHA DO MÓDULO DO ELGX)

CONTROLS (CONTROLES)

1NWS = 1 SWITCH NORMAL CONTROL	(1NWS = MAQUINA DE CHAVE 1 NORMAL)
1RWS = 1 SWITCH REVERSE CONTROL	(1RWS = MAQUINA DE CHAVE 1 REVERSA)
2DGS = 2D SIGNAL REQUEST	(2DGS = REQUISIÇÃO SINAL 2D)
2EGS = 2E SIGNAL REQUEST	(2EGS = REQUISIÇÃO SINAL 2E)
4EGS = 4E SIGNAL REQUEST	(4EGS = REQUISIÇÃO SINAL 4E)
2D–2E–4E STOP = ALL SIGNAL STOP REQUEST	(2D–2E–4E STOP = FECHAR TODOS OS SINAIS)
2DBCS = 2D BLOCK CLEAR REQUEST	(2DBCS = REQUISIÇÃO BLOCO LIVRE 2D)
2EBCS = 2E BLOCK CLEAR REQUEST	(2EBCS = REQUISIÇÃO BLOCO LIVRE 2E)
4EBCS = 4E BLOCK CLEAR REQUEST	(4EBCS = REQUISIÇÃO BLOCO LIVRE 4E)
DD1S = DERAIL DETECTOR OVERRIDE 1	(DD1S = IGNORAR DETECTOR DE DESCARRILHAMENTO 1)
DD2S = DERAIL DETECTOR OVERRIDE 2	(DD2S = IGNORAR DETECTOR DE DESCARRILHAMENTO 2)
1TBN = DETECTOR TRACK BLOCK ON	(1TBN = SEÇÃO DETECTORA BLOQUEADA)
1TBF = DETECTOR TRACK BLOCK OFF	(1TBF = SEÇÃO DETECTORA NÃO BLOQUEADA)
1SBN = 1 SWITCH BLOCK ON	(1SBN = MAQUINA DE CHAVE BLOQUEADA)
1SBF = 1 SWITCH BLOCK OFF	(1SBF = MAQUINA DE CHAVE NÃO BLOQUEADA)
2DTBN = 2D TRACK BLOCK ON	(2DTBN = VIA DE APROXIMAÇÃO 2D BLOQUEADA)
2DTBF = 2D TRACK BLOCK OFF	(2DTBF = VIA DE APROXIMAÇÃO 2D NÃO BLOQUEADA)
2ETBN = 2E TRACK BLOCK ON	(2ETBN = VIA DE APROXIMAÇÃO 2E BLOQUEADA)
2ETBF = 2E TRACK BLOCK OFF	(2ETBF = VIA DE APROXIMAÇÃO 2E NÃO BLOQUEADA)
4ETBN = 4E TRACK BLOCK ON	(4ETBN = VIA DE APROXIMAÇÃO 4E BLOQUEADA)
4ETBF = 4E TRACK BLOCK OFF	(4ETBF = VIA DE APROXIMAÇÃO 4E NÃO BLOQUEADA)

OFFICE TO ELECTROLOGIXS COMMUNICATION MODULE
SERIAL COMMUNICATION BITS
(MODULO DE COMUNICAÇÃO ENTRE CCO E ELECTROLOGIXS
BITS DE COMUNICAÇÃO SERIAL)

CONTROLS FROM OFFICE (CONTROLES DO CCO)


WORD (PALAVRA)	1	2	3	4	5	6	7	8
1	1 NWS	1 RWS			2D GS	2E GS	4E GS	2D–2E–4E STOP
2	2D BCS	2E BCS	4E BCS		DD1S	DD2S	1 TBN	1 TBF
3	1 SBN	1 SBF	2D TBN	2D TBF	2E TBN	2E TBF	4E TBN	4E TBF
4								


INDICATIONS TO OFFICE (INDICAÇÕES PARA O CCO)


WORD (PALAVRA)	1	2	3	4	5	6	7	8
1	1 NWK	1 RWK	1 LK	1 WCBPK	1 WLPK	2D GZK	2D GK	2E GZK
2	2E GK	4E GZK	4E GK	2D–2E–4E TEK	2D BCK	2D BCGK	2E BCK	2E BCGK
3	4E BCK	4E BCGK	1 TK	2D AK	2D BK	M AK		S2 AK
4	1 TBK	1 SBK	2D TBK	2E TBK	4E TBK	DOOR ALRMK	DD 1K	DD 2K
5	POK	MOK	2D LOK	2E LOK	4E LOK	BLK POK		HEALTHK
6								

MRS LOGISTICA S.A.

DESCRIÇÃO:	CIRCUITOS DE CONTROLE E INDICAÇÃO DO CCO		
LOCAÇÃO:	P2–04A (1)		
DESIGN POR:	XORAIL	REVISÃO: 1	DATA: 22–JUN–11
CAD POR:	XORAIL	ARQUIVO:	EE–SD–FA–0FIN–116.05

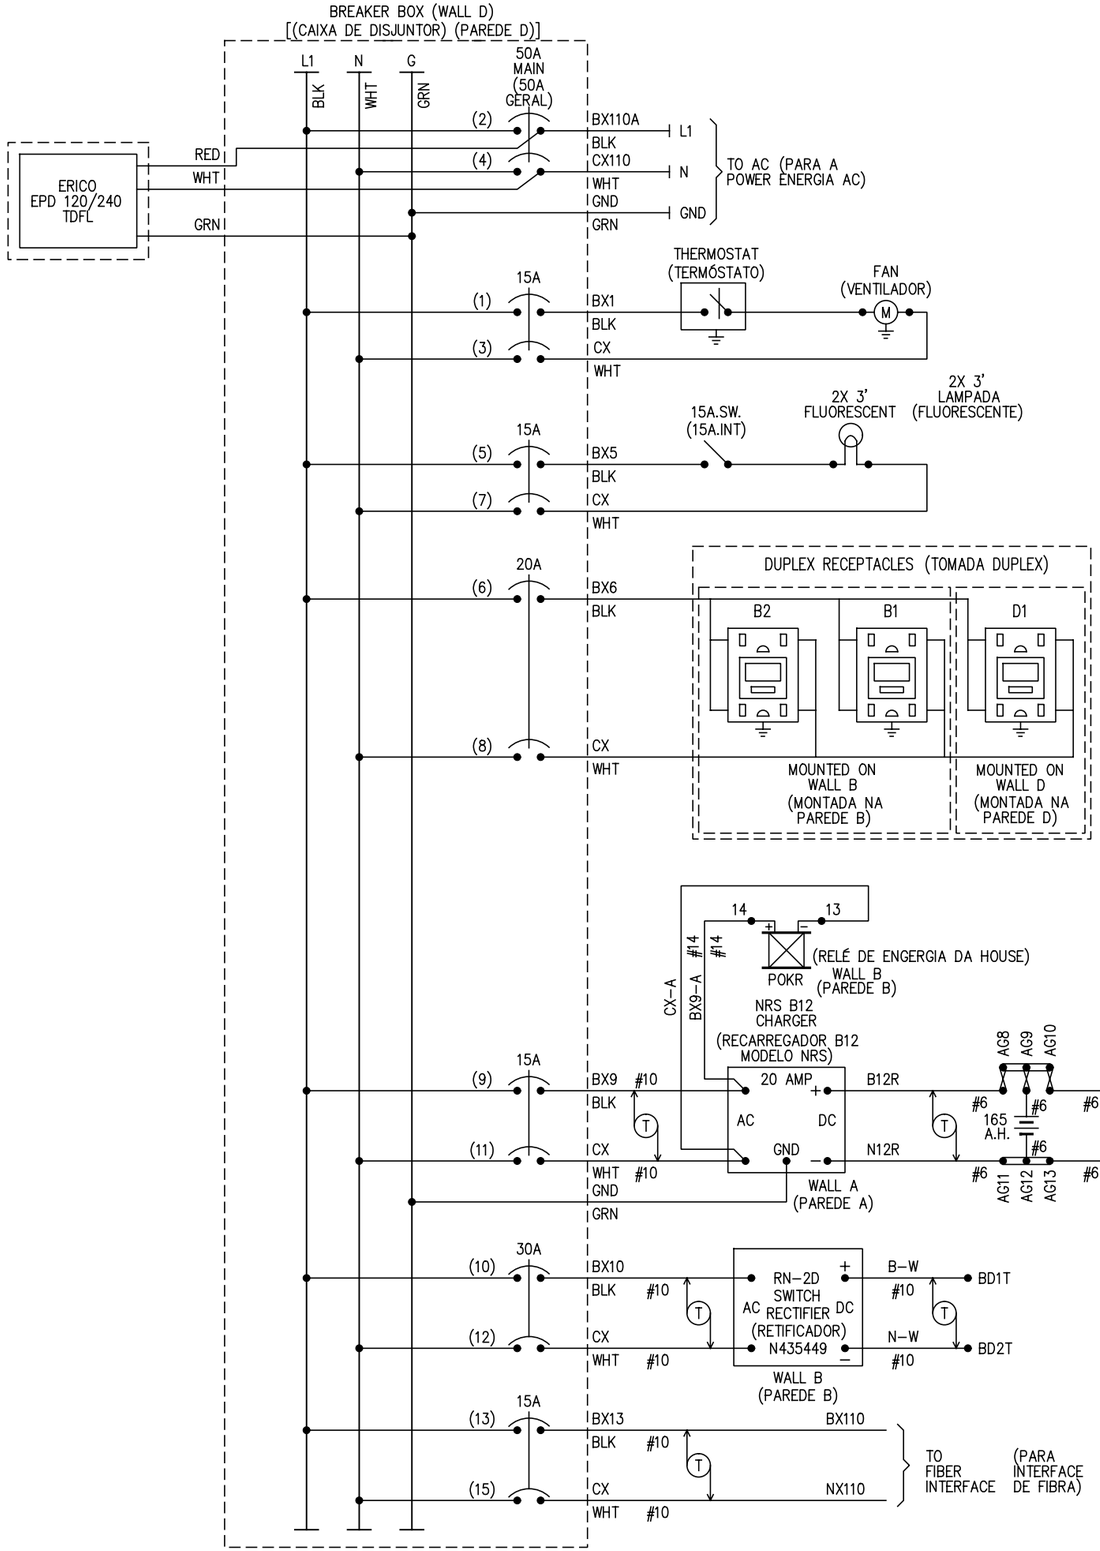

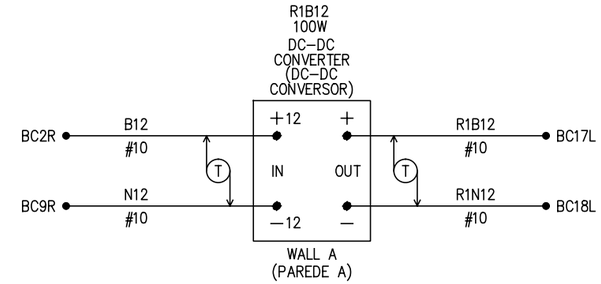

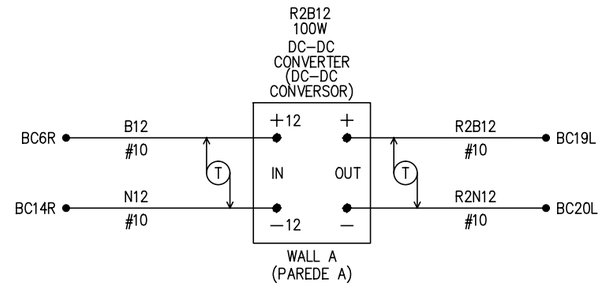


NOTES (OBSERVAÇÕES):

1. (T)= TWISTED (TRANÇADO)
2. BREAKER BOX WIRING TO BE #10 UNLESS NOTED (PORT) (CABO PARA A CAIXA DE DISJUNTOR SERÀ #6,0mm² A MENOS INDICADO)
3. #14 WIRING (CABO #1.5mm²)
4. #6 WIRING (CABO #16,0mm²)


MRS LOGISTICA S.A.

DESCRIÇÃO:	DISTRIBUIÇÃO DE ENERGIA		
LOCAÇÃO:	P2–04A (1)		
DESIGN POR:	XORAIL	REVISÃO: 1	DATA: 22–JUN–11
CAD POR:	XORAIL	ARQUIVO:	EE–SD–FA–0FIN–116.06

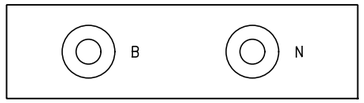


CIO–1A MODULE DIAGNOSTIC AND OFFICE PORT PIN ASSIGNMENT		(C10–1A ATRIBUIÇÃO DOS PINOS PORTA DE DIAGNÓSTICO E DE OFFICE)	
PIN (PINOS)	SIGNAL (SINAL)	SIGNAL NAME	(NOME DO SINAL)
1	CD	CARRIER DETECT	(CARRIER DETETOR)
2	RX	RECEIVE DATA	(RECEBE DADOS)
3	TX	TRANSMIT DATA	(ENVIA DADOS)
4	DTR	DTE	(DTE)
5	GND	COMMON SIGNAL RETURN	(SINAL COMUM DE RETORNO)
6	DSR	DCE	(DCE)
7	RTS	REQUEST TO SEND	(PEDIDO DE ENVIO)
8	CTS	CLEAR TO SEND	(LIVRE PARA ENVIAR)
9	RI	RING INDICATOR	(INDICADOR DE TOQUE)

TYPICAL INSTALLATION OF EPROM & DIP SHUNT (INSTALAÇÃO TIPICA DE EPROM & DIP SHUNT)

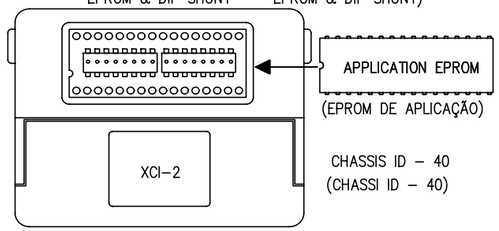


CHASSIS ID DIP SHUNTS LOCATED ON BACKPLANE UNDERNEATH XCI–2 MODULE (DIP SHUNTS DE ID CHASSI LOCALIZADA NA PLACA TRASEIRA EMBAIXO DO MÓDULO XCI–2)

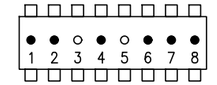


○ = TAB INTACT (MADE) (TAB INTACTO)
● = TAB PUNCHED OUT (BROKEN) (TAB QUEBRADO)

VITAL SELECTION ID–N/A (SELEÇÃO VITAL ID–N/A)

VITAL SELECTION DIP SHUNTS LOCATED INSIDE XCI–2 MODULE UNDERNEATH EPROM (SELEÇÃO VITAL DIP SHUNTS LOCALIZADA DENTRO DO MÓDULO XCI–2 EMBAIXO DO EPROM)

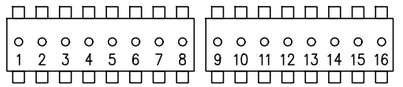

○ = TAB INTACT (MADE) (TAB INTACTO)
● = TAB PUNCHED OUT (BROKEN) (TAB QUEBRADO)

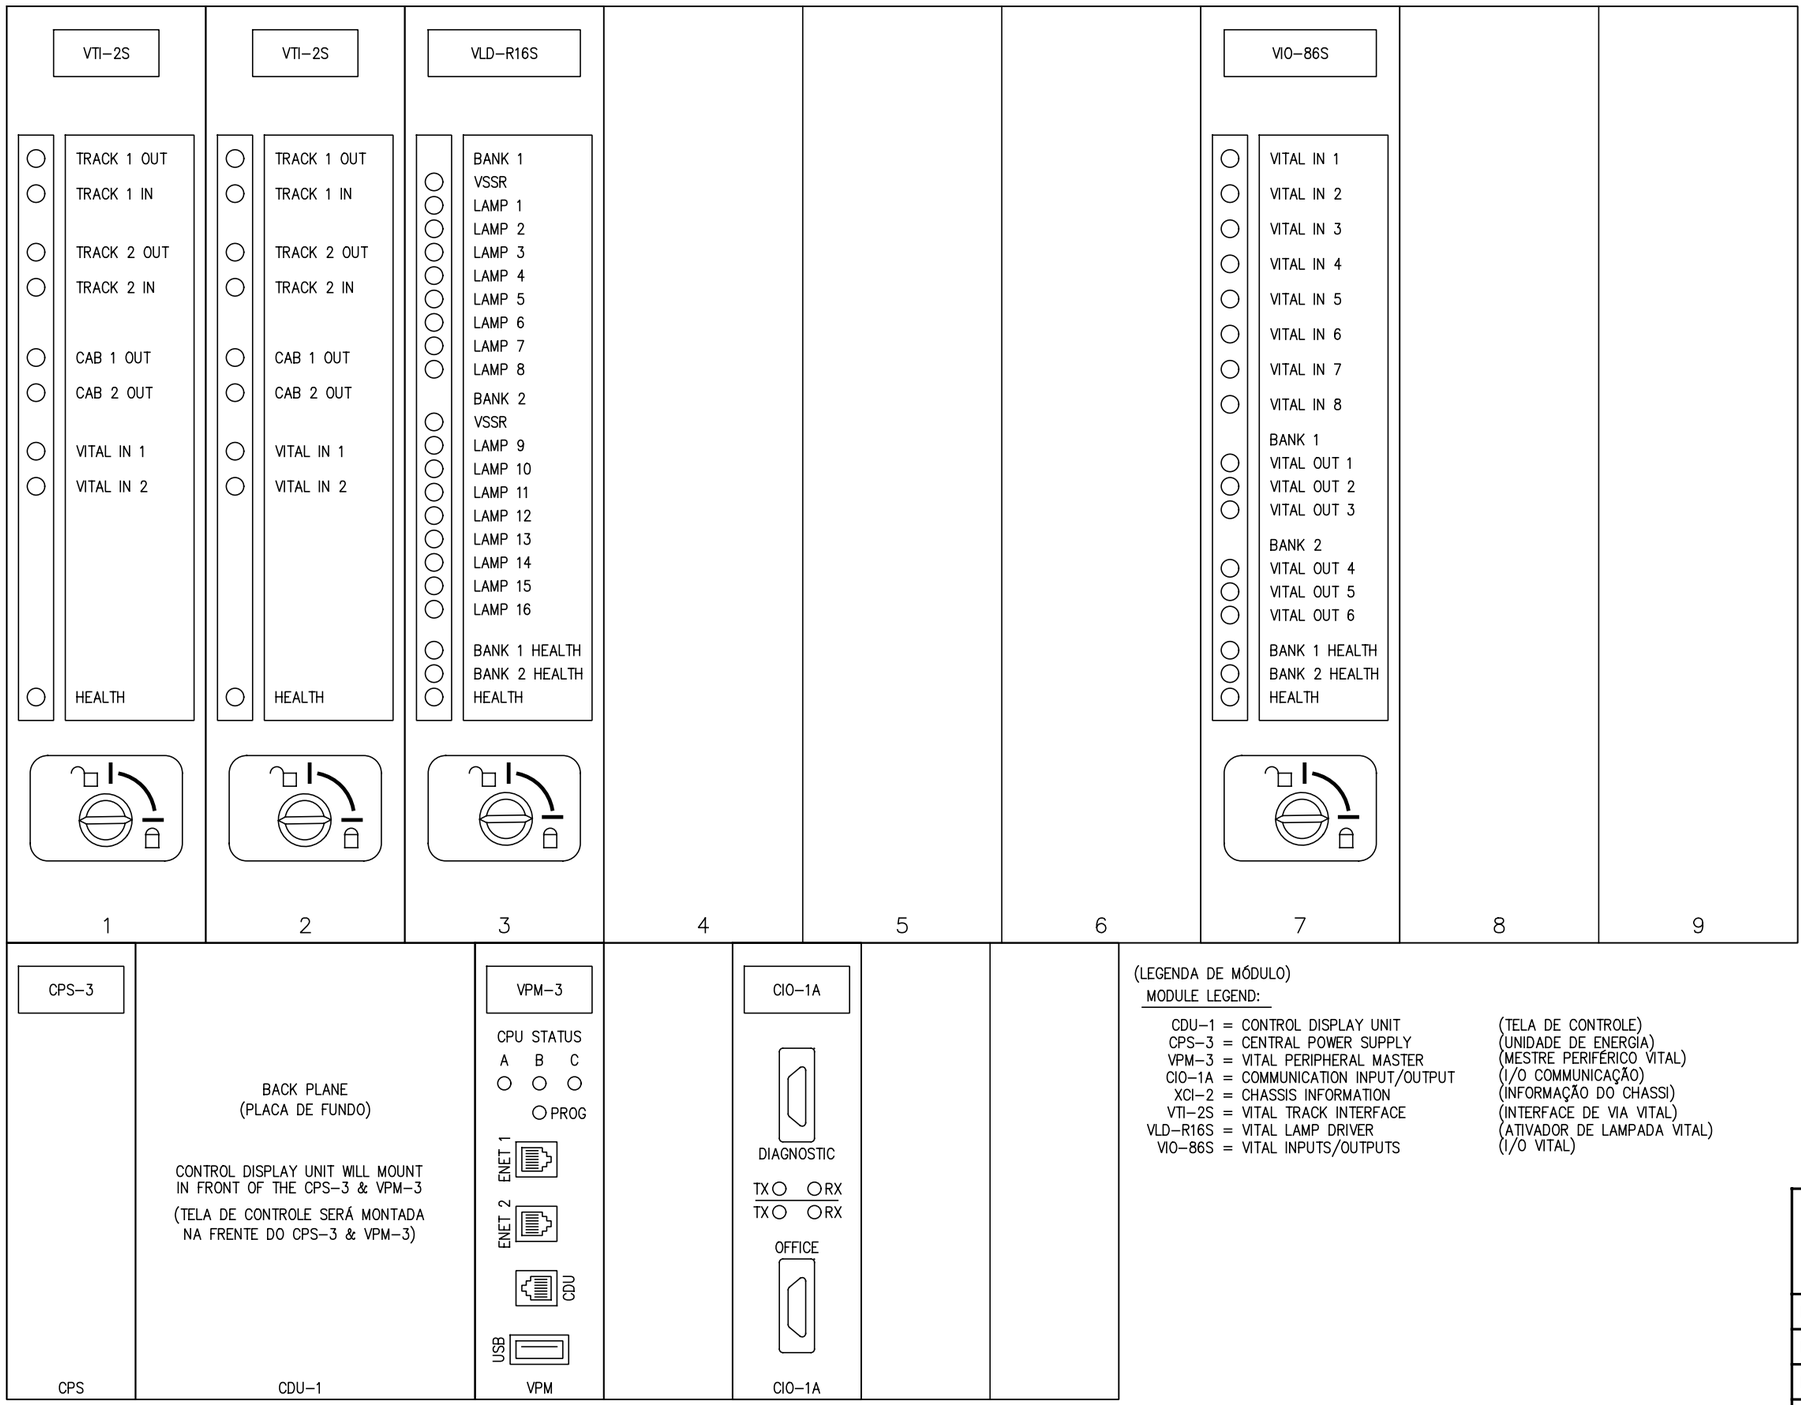


(LEGENDA DE MÓDULO)
MODULE LEGEND:

CDU–1	= CONTROL DISPLAY UNIT	(TELA DE CONTROLE)
CPS–3	= CENTRAL POWER SUPPLY	(UNIDADE DE ENERGIA)
VPM–3	= VITAL PERIPHERAL MASTER	(MESTRE PERIFÉRICO VITAL)
CIO–1A	= COMMUNICATION INPUT/OUTPUT	(I/O COMMUNICAÇÃO)
XCI–2	= CHASSIS INFORMATION	(INFORMAÇÃO DO CHASSI)
VTI–2S	= VITAL TRACK INTERFACE	(INTERFACE DE VIA VITAL)
VLD–R16S	= VITAL LAMP DRIVER	(ATIVADOR DE LAMPADA VITAL)
VIO–86S	= VITAL INPUTS/OUTPUTS	(I/O VITAL)

MRS LOGISTICA S.A.

DESCRIÇÃO:	CONFIGURAÇÃO DO MÓDULO ELECTROLOGIXS		
LOCAÇÃO:	P2–04A (1)		
DESIGN POR:	XORAIL	REVISÃO: 1	DATA: 22–JUN–11
CAD POR:	XORAIL	ARQUIVO:	EE–SD–FA–0FIN–116.07

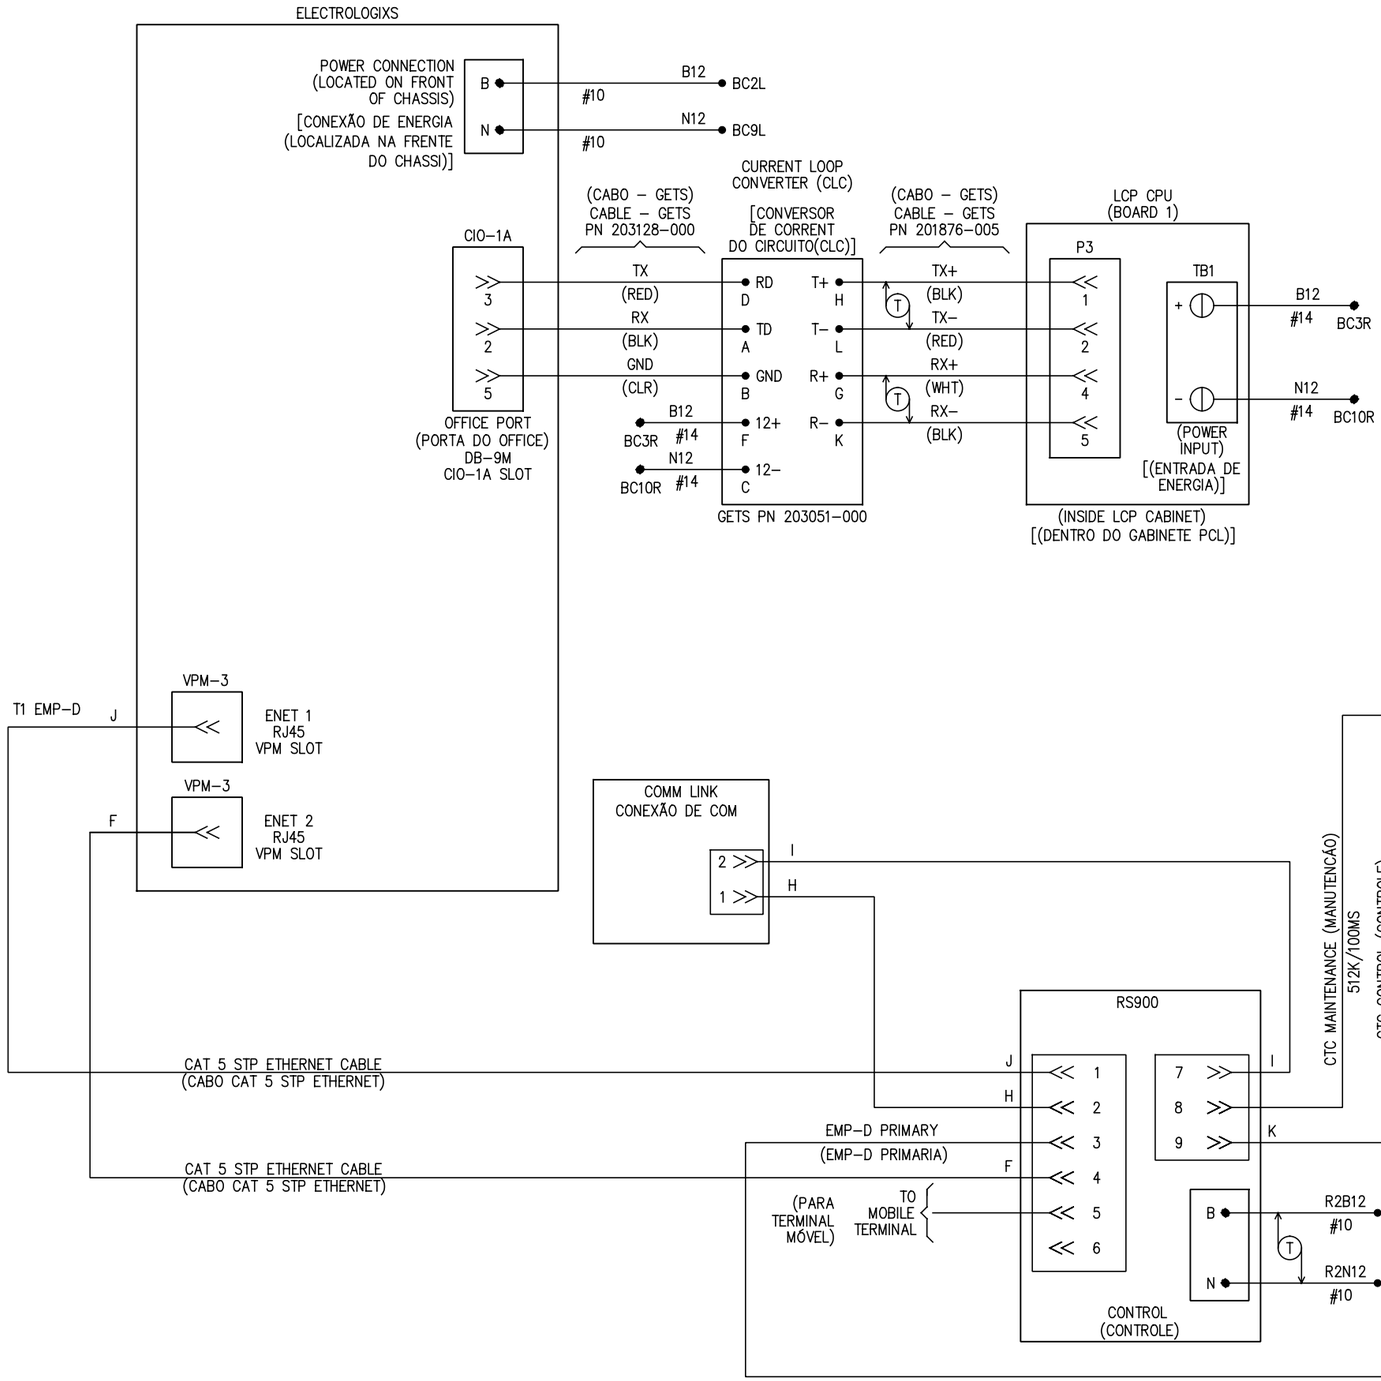


NOTES (OBSERVAÇÕES):

1. (T) = TWISTED (TRANÇADO)
2. #14 WIRING (CABO #1.5mm²)
3. #10 WIRING (CABO #6,0mm²)

MRS LOGISTICA S.A.

DESCRIÇÃO:	CIRCUITOS DE COMUNICAÇÃO DO ELECTROLOGIXS		
LOCAÇÃO:	P2–04A (1)		
DESIGN POR:	XORAIL	REVISÃO: 1	DATA: 22–JUN–11
CAD POR:	XORAIL	ARQUIVO:	EE–SD–FA–0FIN–116.08

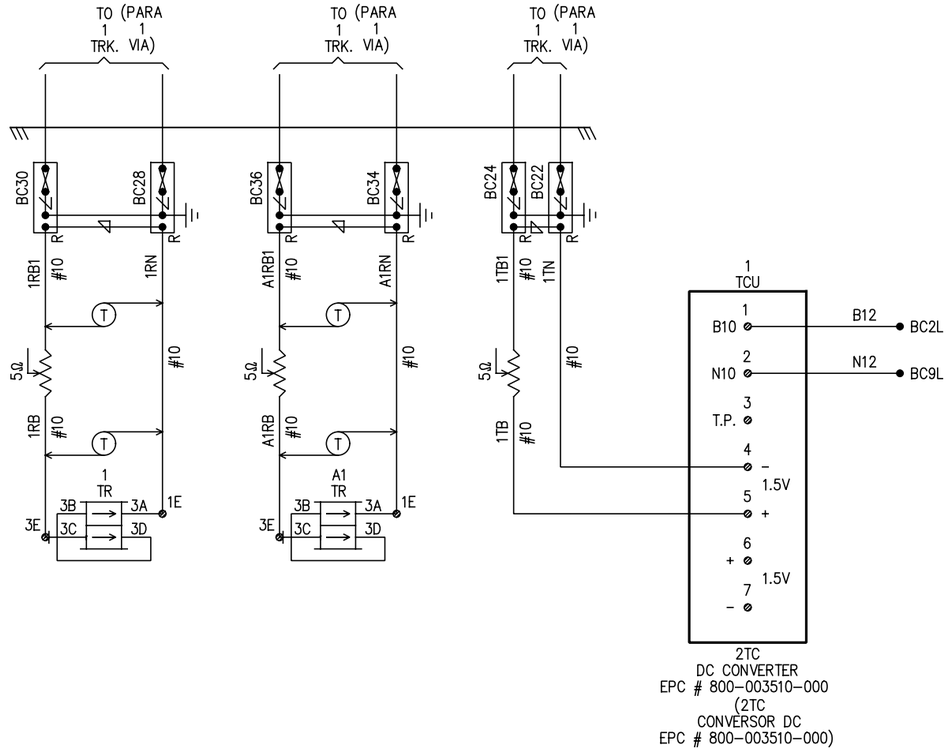


NOTES (OBSERVAÇÕES):

1. ∠= ARRESTER (SUPRESSOR)
2. ⊿= EQUALIZER (EQUALIZADOR)
3. ALL HOUSE WIRING #14 UNLESS NOTED
   (TODOS CABOS DA HOUSE #1,5mm² A MENOS INDICADO.)
4. #10 WIRING (CABO #6,0mm²)

MRS LOGISTICA S.A.

DESCRIÇÃO:	CIRCUITOS DE VIA		
LOCAÇÃO:	P2–04A (1)		
DESIGN POR:	XORAIL	REVISÃO: 1	DATA: 22–JUN–11
CAD POR:	XORAIL	ARQUIVO:	EE–SD–FA–0FIN–116.09

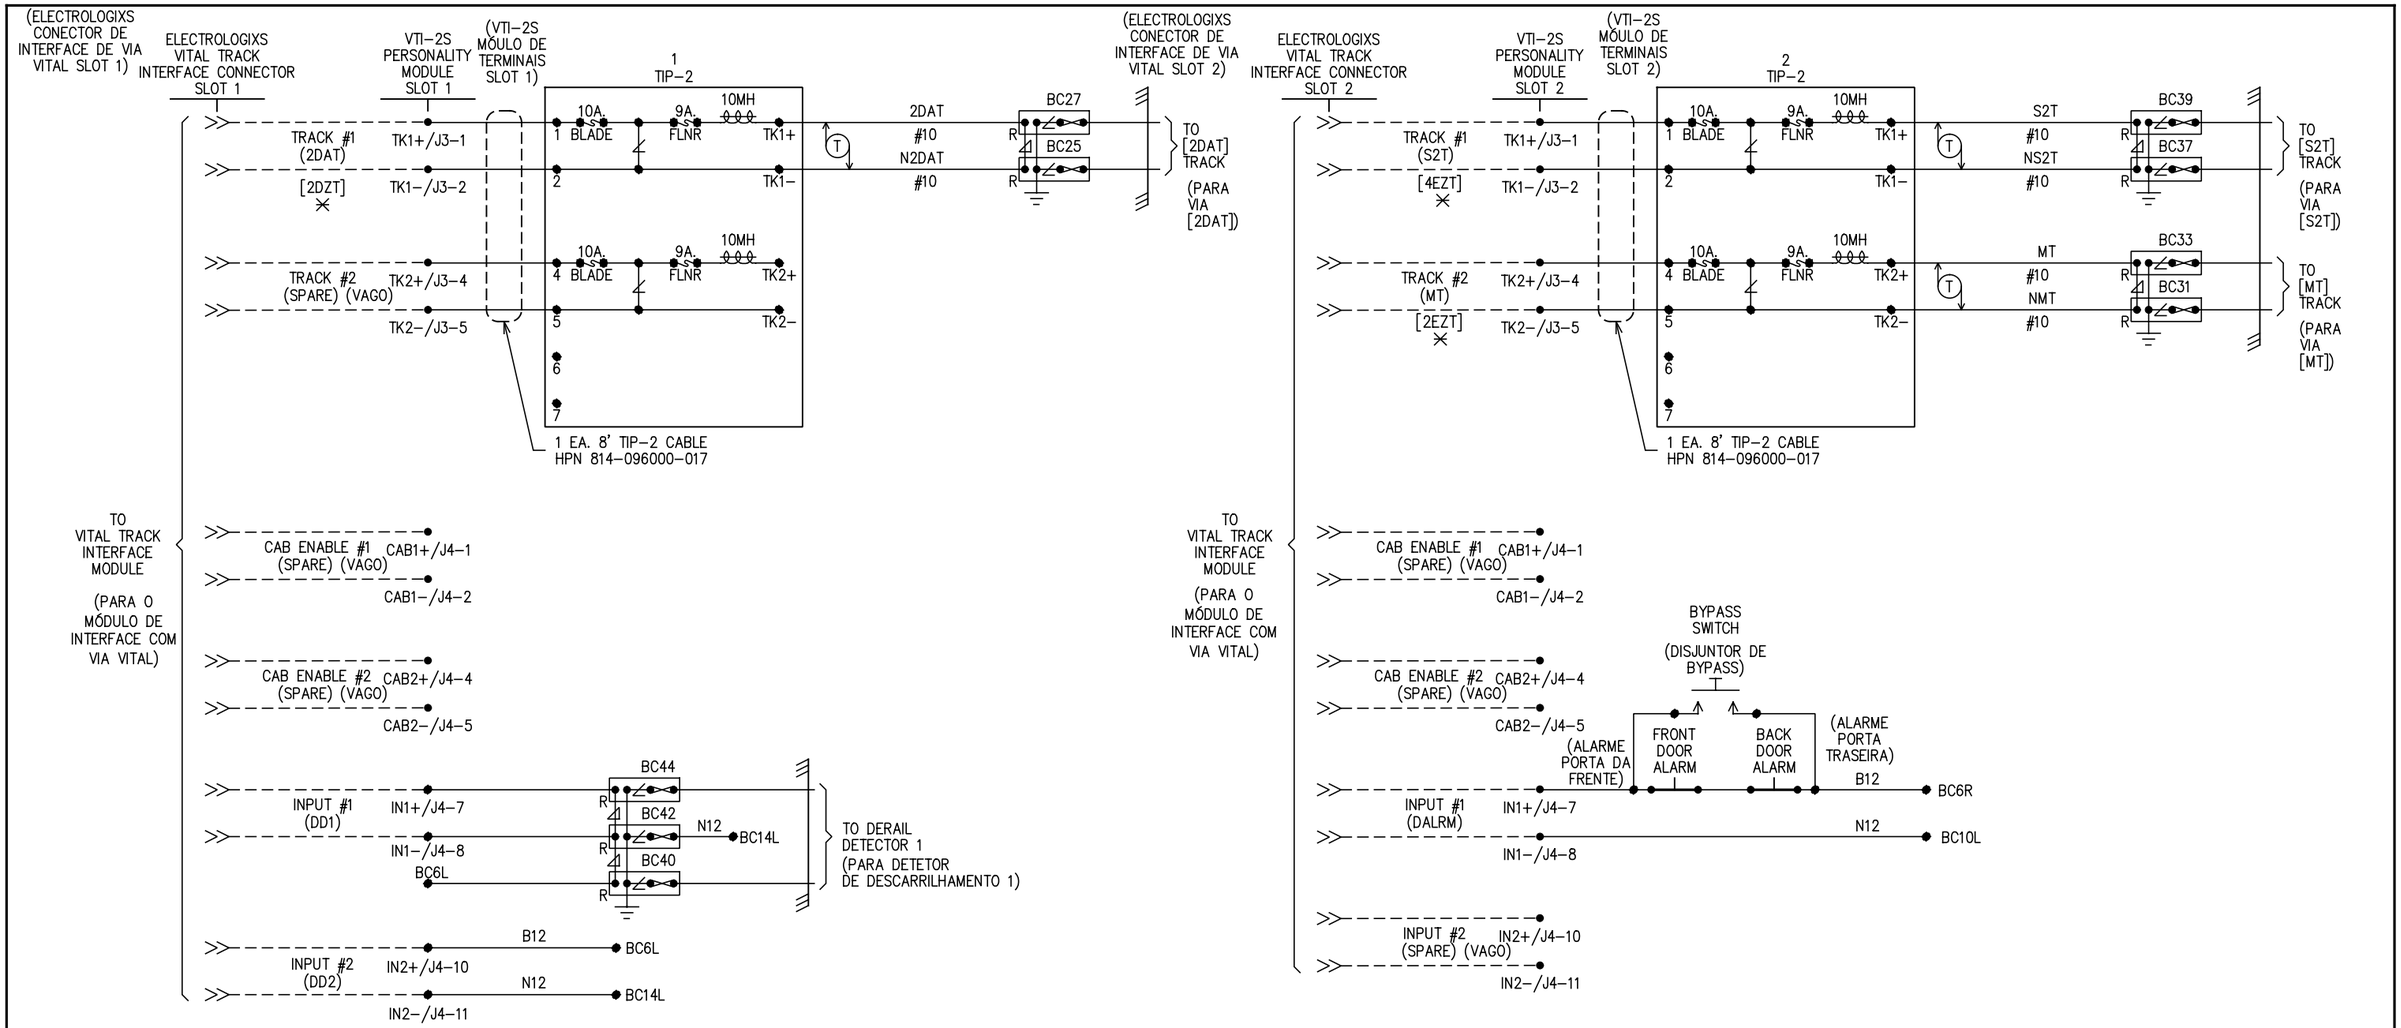

VTI-2S PERSONALITY MODULE SLOT 1 PLUG CONNECTORS
(VTI-2S MÓDULO DE TERMINAIS SLOT 1 CONECTORES PLUG)

TK1+	■	1	CAB1+	□	1
TK1-	■	2	CAB1-	□	2
—	□	3	—	□	3
TK2+	■	4	CAB2+	□	4
TK2-	■	5	CAB2-	□	5
—	□	6	—	□	6
—	□	7	IN1+	■	7
		J3	IN1-	■	8
			—	□	9
			IN2+	■	10
			IN2-	■	11
				J4	

■ = WIRE PRESENT (FIO PRESENTE)

VTI-2S PERSONALITY MODULE SLOT 2 PLUG CONNECTORS
(VTI-2S MÓDULO DE TERMINAIS SLOT 2 CONECTORES PLUG)

TK1+	■	1	CAB1+	□	1
TK1-	■	2	CAB1-	□	2
—	□	3	—	□	3
TK2+	■	4	CAB2+	□	4
TK2-	■	5	CAB2-	□	5
—	□	6	—	□	6
—	□	7	IN1+	■	7
		J3	IN1-	■	8
			—	□	9
			IN2+	□	10
			IN2-	□	11
				J4	


■ = WIRE PRESENT (FIO PRESENTE)


NOTES (OBSERVAÇÕES):


1. ∠= ARRESTER (SUPRESSOR)
2. ⊿= EQUALIZER (EQUALIZADOR)
3. ---- = INTERNAL CONNECTION (CONEXÃO INTERNA)
4. ALL HOUSE WIRING #14 UNLESS NOTED. (TODOS CABOS DA HOUSE #1,5mm² A MENOS INDICADO.)
5. #10 WIRING (CABO #6,0mm²)
6. (✕) = SOFTWARE NOMENCLATURE ONLY (NOMENCLATURA NO PROGRAMA DE APLICAÇÃO.)


MRS LOGISTICA S.A.

DESCRIÇÃO:	I/O DE VIA E VITAL DO ELECTROLOGIXS		
LOCAÇÃO:	P2-04A (1)		
DESIGN POR:	XORAIL	REVISÃO: 1	DATA: 22-JUN-11
CAD POR:	XORAIL	ARQUIVO:	EE-SD-FA-0FIN-116.10

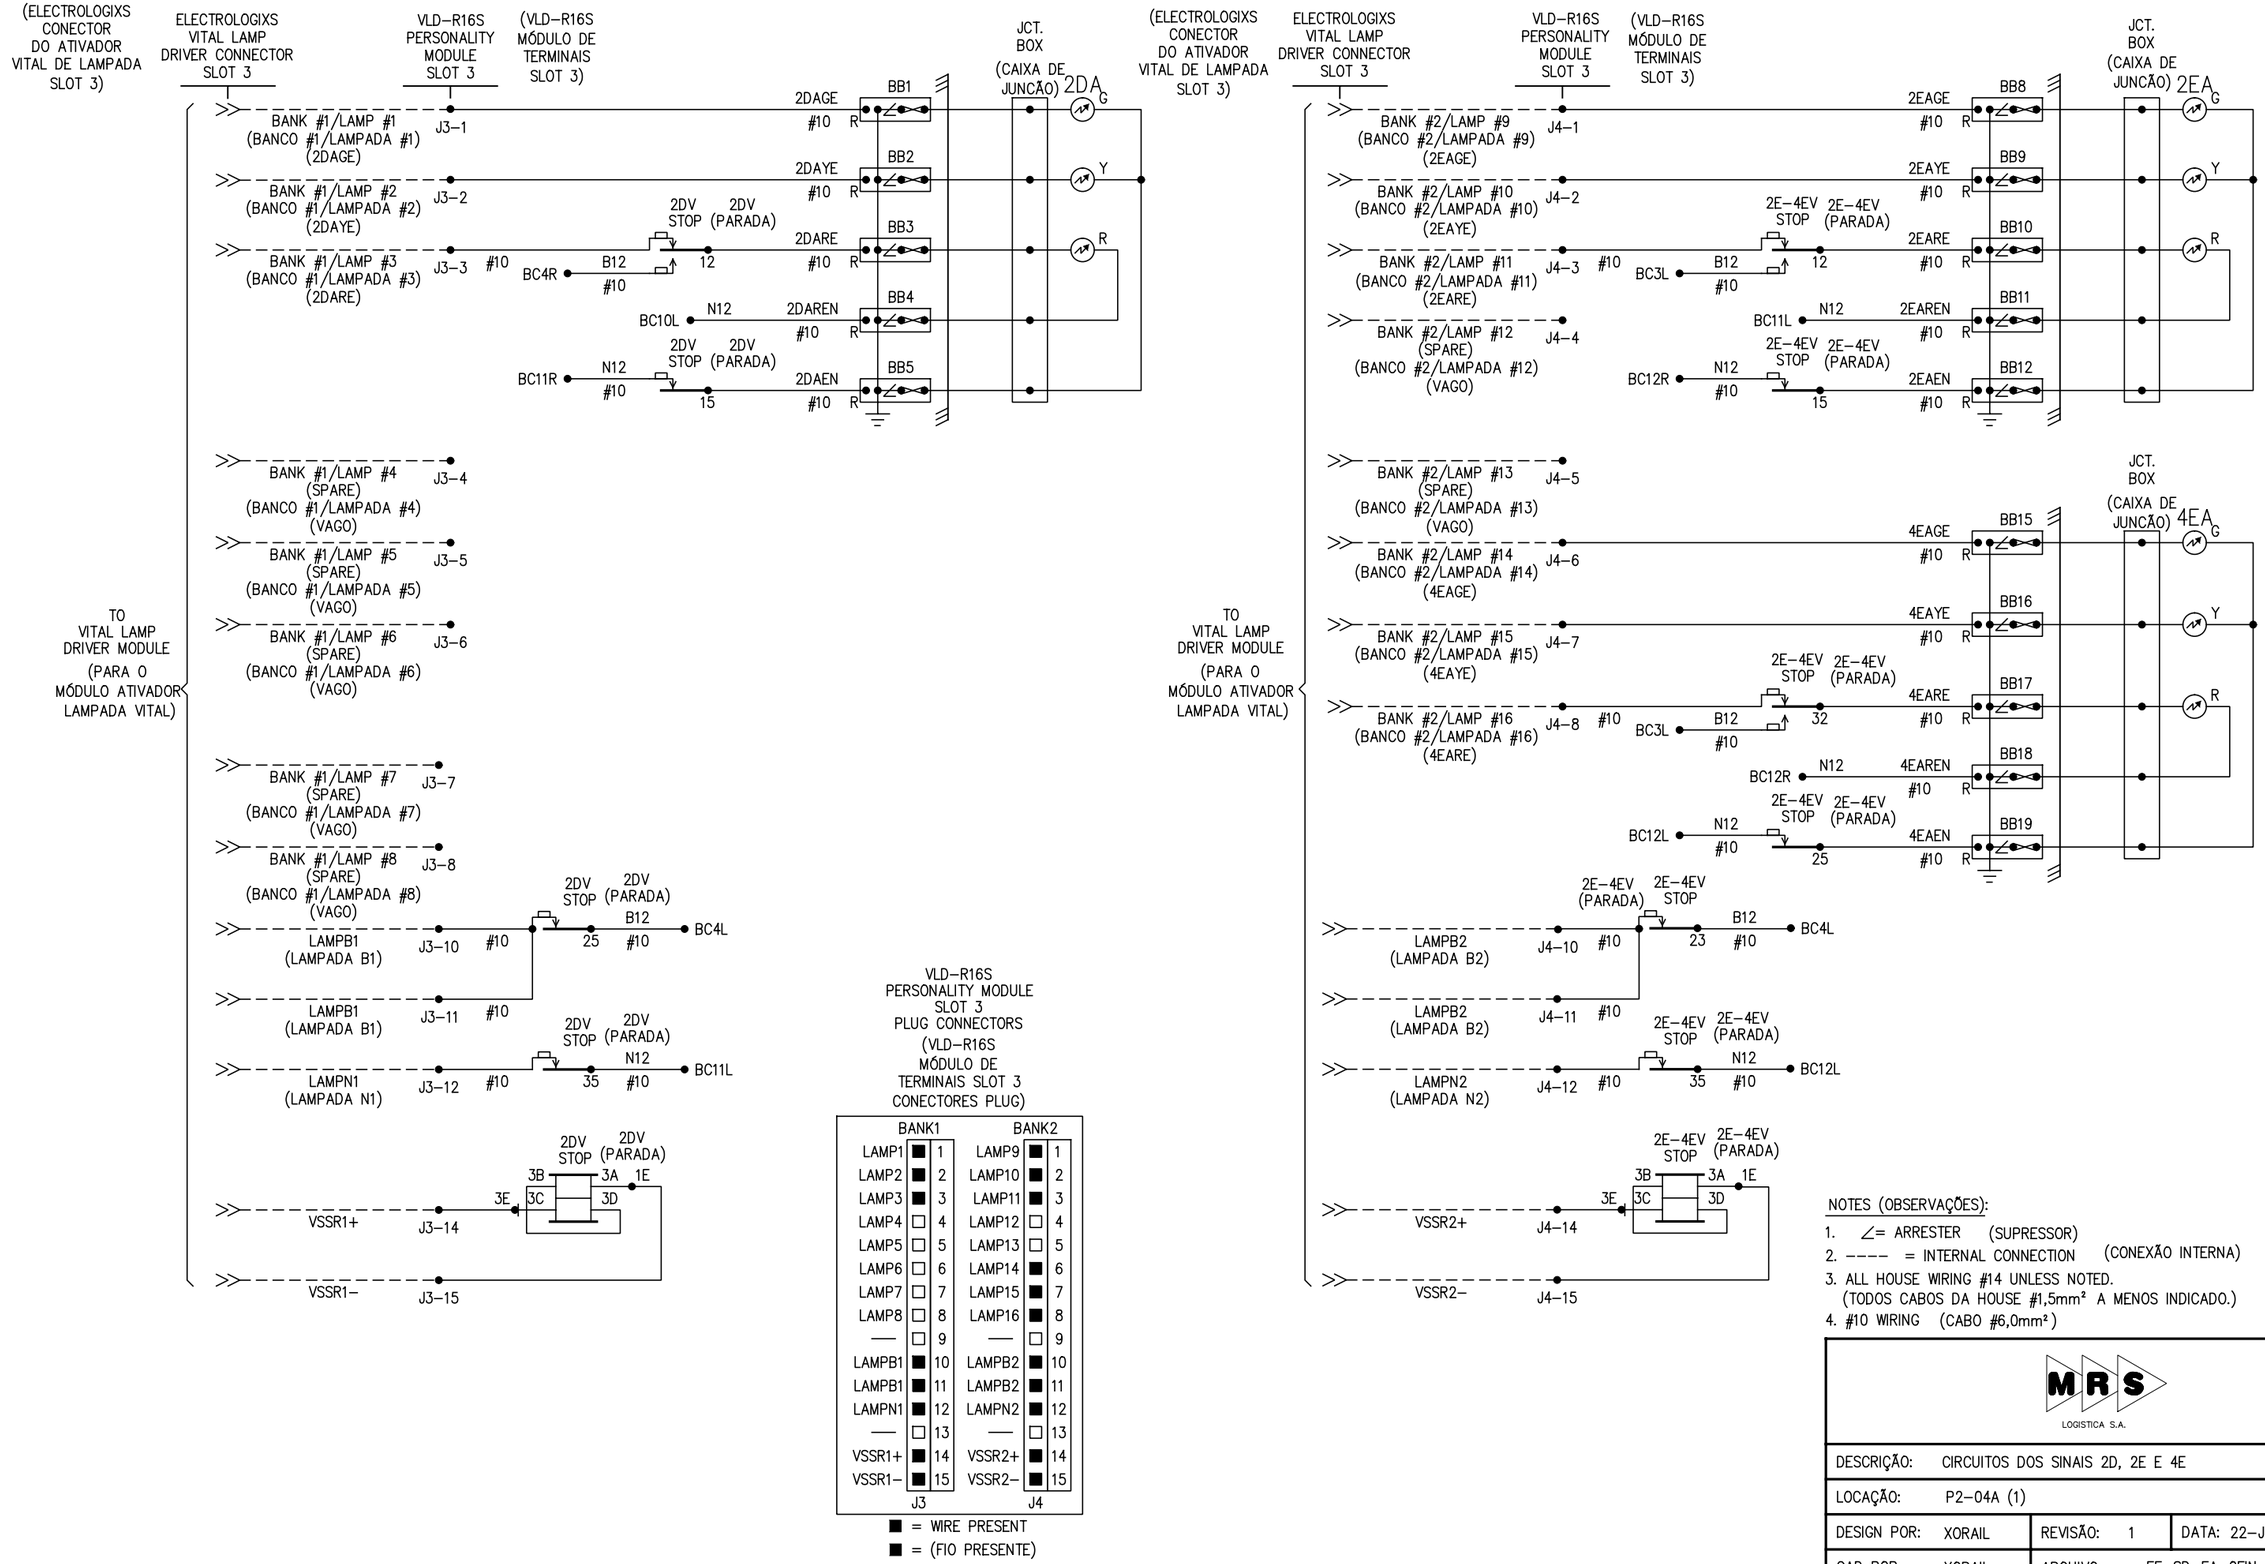
(ELECTROLOGIXS CONECTOR DO ATIVADOR VITAL DE LAMPADA SLOT 3)
ELECTROLOGIXS VITAL LAMP DRIVER CONNECTOR SLOT 3
VLD-R16S PERSONALITY MODULE SLOT 3
(VLD-R16S MÓDULO DE TERMINAIS SLOT 3)
JCT. BOX (CAIXA DE JUNÇÃO) 2DA
BANK #1/LAMP #1 (BANCO #1/LAMPADA #1) (2DAGE)
BANK #1/LAMP #2 (BANCO #1/LAMPADA #2) (2DAYE)
BANK #1/LAMP #3 (BANCO #1/LAMPADA #3) (2DARE)
BANK #1/LAMP #4 (SPARE) (BANCO #1/LAMPADA #4) (VAGO)
BANK #1/LAMP #5 (SPARE) (BANCO #1/LAMPADA #5) (VAGO)
BANK #1/LAMP #6 (SPARE) (BANCO #1/LAMPADA #6) (VAGO)
BANK #1/LAMP #7 (SPARE) (BANCO #1/LAMPADA #7) (VAGO)
BANK #1/LAMP #8 (SPARE) (BANCO #1/LAMPADA #8) (VAGO)
LAMPB1 (LAMPADA B1)
LAMPN1 (LAMPADA N1)
VSSR1+
VSSR1-
TO VITAL LAMP DRIVER MODULE (PARA O MÓDULO ATIVADOR LAMPADA VITAL)
2DV STOP (PARADA)
BC4R
BC10L
BC11R
BC4L
BC11L
2DAGE
2DAYE
2DARE
2DAREN
2DAEN
BB1
BB2
BB3
BB4
BB5
(ELECTROLOGIXS CONECTOR DO ATIVADOR VITAL DE LAMPADA SLOT 3)
ELECTROLOGIXS VITAL LAMP DRIVER CONNECTOR SLOT 3
VLD-R16S PERSONALITY MODULE SLOT 3
(VLD-R16S MÓDULO DE TERMINAIS SLOT 3)
JCT. BOX (CAIXA DE JUNÇÃO) 2EA
BANK #2/LAMP #9 (BANCO #2/LAMPADA #9) (2EAGE)
BANK #2/LAMP #10 (BANCO #2/LAMPADA #10) (2EAYE)
BANK #2/LAMP #11 (BANCO #2/LAMPADA #11) (2EARE)
BANK #2/LAMP #12 (SPARE) (BANCO #2/LAMPADA #12) (VAGO)
BANK #2/LAMP #13 (SPARE) (BANCO #2/LAMPADA #13) (VAGO)
BANK #2/LAMP #14 (BANCO #2/LAMPADA #14) (4EAGE)
BANK #2/LAMP #15 (BANCO #2/LAMPADA #15) (4EAYE)
BANK #2/LAMP #16 (BANCO #2/LAMPADA #16) (4EARE)
LAMPB2 (LAMPADA B2)
LAMPN2 (LAMPADA N2)
VSSR2+
VSSR2-
TO VITAL LAMP DRIVER MODULE (PARA O MÓDULO ATIVADOR LAMPADA VITAL)
2E-4EV STOP (PARADA)
BC3L
BC12R
BC12L
BC4L
BC11L
2EAGE
2EAYE
2EARE
2EAREN
2EAEN
BB8
BB9
BB10
BB11
BB12
JCT. BOX (CAIXA DE JUNÇÃO) 4EA
4EAGE
4EAYE
4EARE
4EAREN
4EAEN
BB15
BB16
BB17
BB18
BB19
VLD-R16S PERSONALITY MODULE SLOT 3 PLUG CONNECTORS (VLD-R16S MÓDULO DE TERMINAIS SLOT 3 CONECTORES PLUG)
BANK1
BANK2
LAMP1 LAMP2 LAMP3 LAMP4 LAMP5 LAMP6 LAMP7 LAMP8 — LAMPB1 LAMPB1 LAMPN1 — VSSR1+ VSSR1-
LAMP9 LAMP10 LAMP11 LAMP12 LAMP13 LAMP14 LAMP15 LAMP16 — LAMPB2 LAMPB2 LAMPN2 — VSSR2+ VSSR2-
J3
J4
■ = WIRE PRESENT
■ = (FIO PRESENTE)
NOTES (OBSERVAÇÕES):
1. ∠= ARRESTER (SUPRESSOR)
2. ----- = INTERNAL CONNECTION (CONEXÃO INTERNA)
3. ALL HOUSE WIRING #14 UNLESS NOTED. (TODOS CABOS DA HOUSE #1,5mm² A MENOS INDICADO.)
4. #10 WIRING (CABO #6,0mm²)
MRS LOGISTICA S.A.
DESCRIÇÃO: CIRCUITOS DOS SINAIS 2D, 2E E 4E
LOCAÇÃO: P2-04A (1)
DESIGN POR: XORAIL
REVISÃO: 1
DATA: 22-JUN-11
CAD POR: XORAIL
ARQUIVO: EE-SD-FA-0FIN-116.11

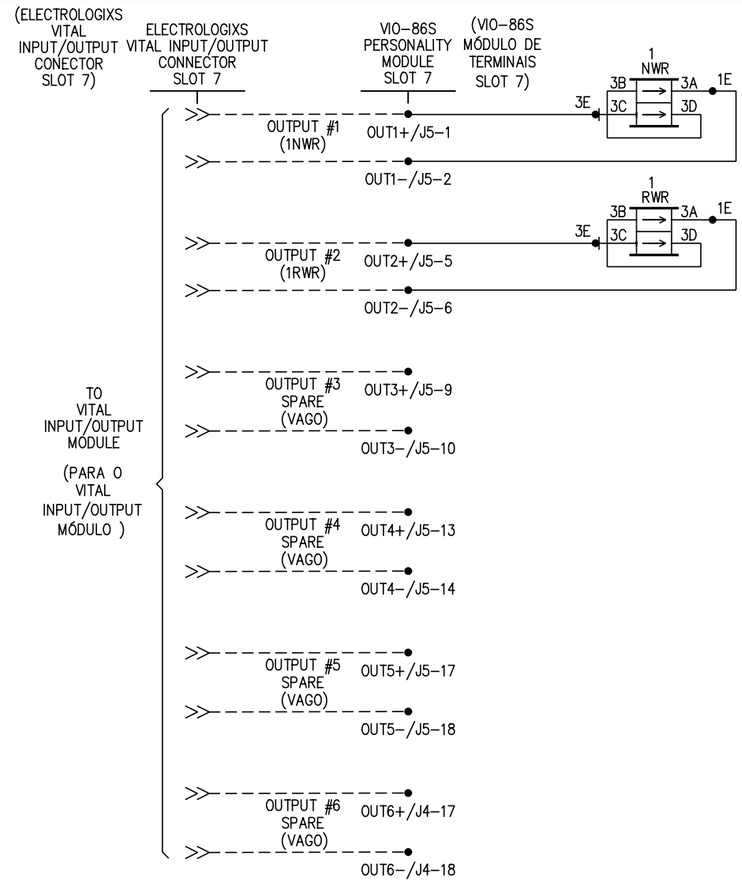

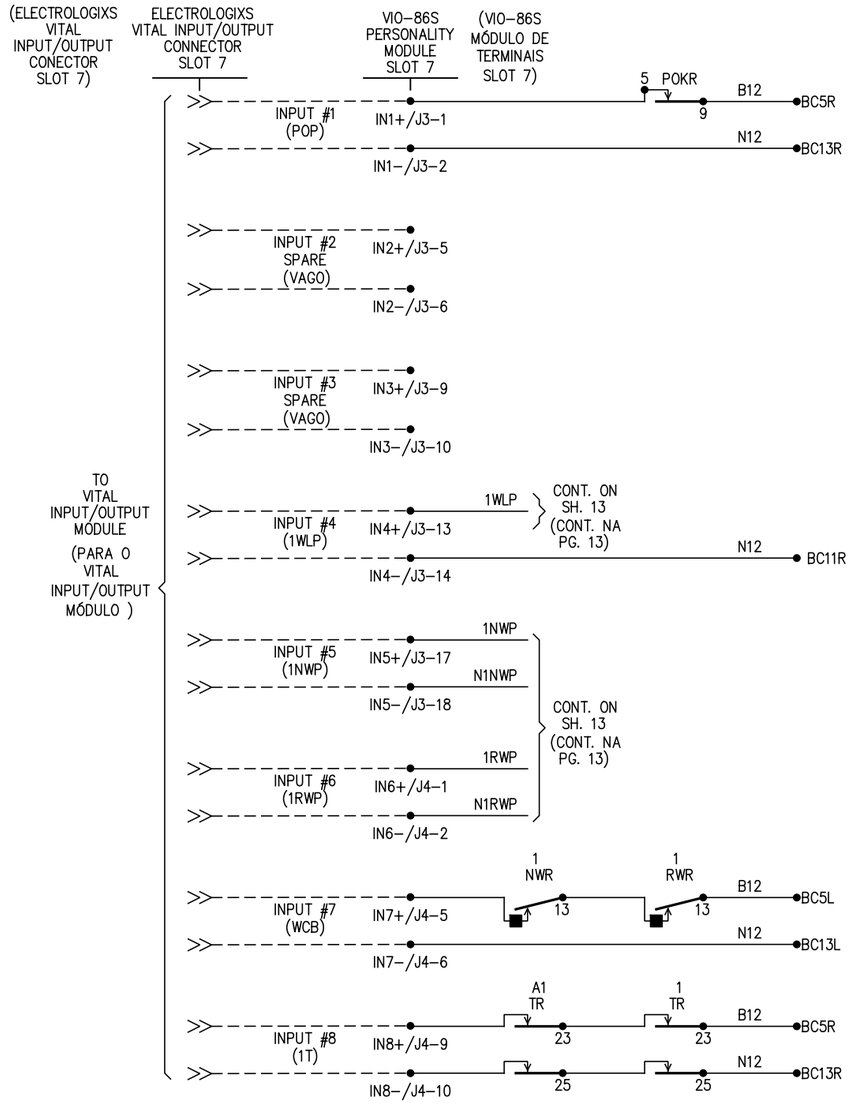

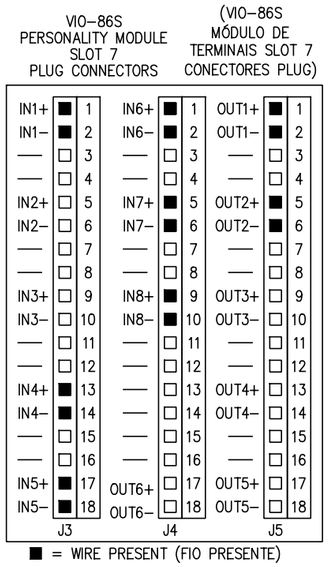


NOTES (OBSERVAÇÕES):


1. ---- = INTERNAL CONNECTION (CONEXÃO INTERNAL)
2. ALL HOUSE WIRING #14 UNLESS NOTED
   (TODOS CABOS DA HOUSE #1,5mm² A MENOS INDICADO.)

MRS LOGISTICA S.A.

DESCRIÇÃO:	CIRCUITOS I/O DO ELECTROLOGIXS		
LOCAÇÃO:	P2-04A (1)		
DESIGN POR:	XORAIL	REVISÃO: 1	DATA: 22-JUN-11
CAD POR:	XORAIL	ARQUIVO:	EE-SD-FA-0FIN-116.12

P80 SWITCH MACHINE (RH)
(P80 MAQUINA DE CHAVE DE MÃO DIREITA)
RIGHT HAND POINT CLOSED
(AGULHA DE MÃO DIREITA FECHADA)

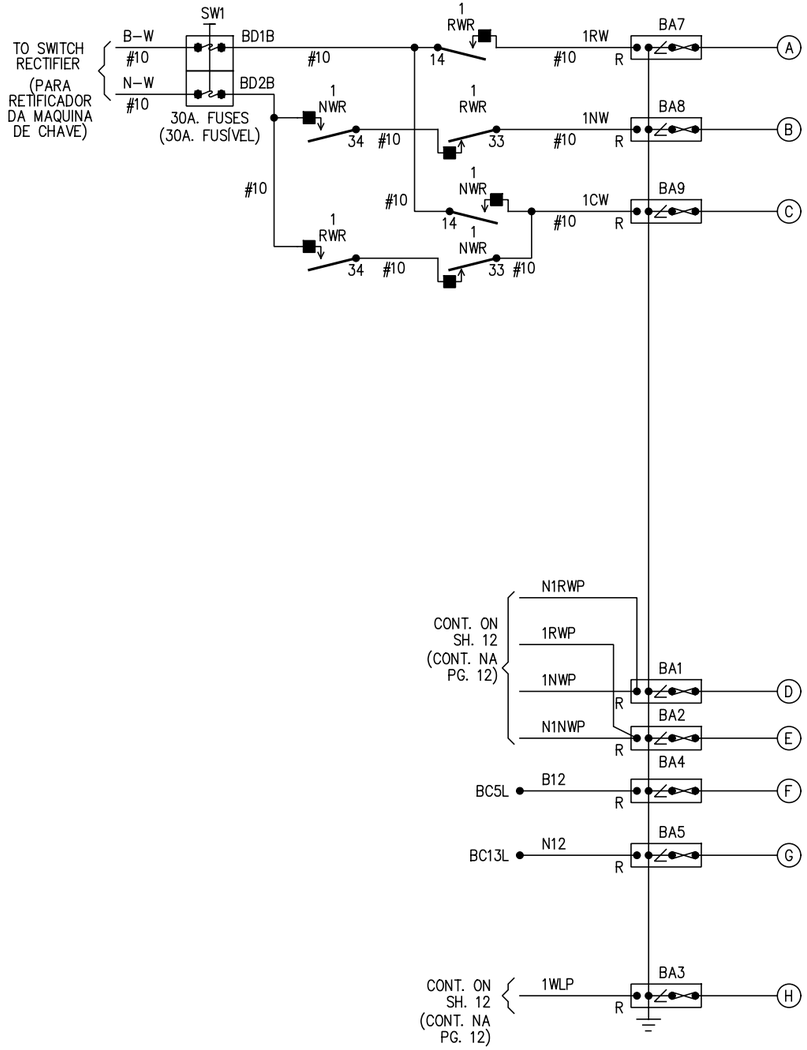

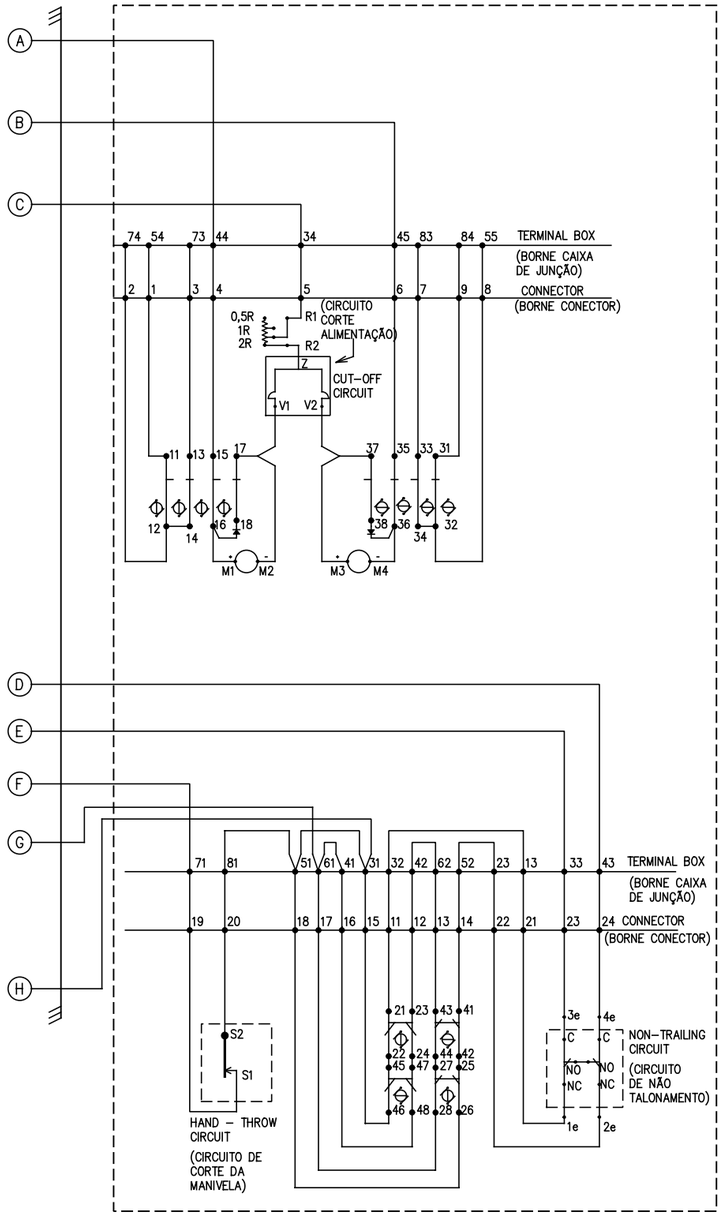

RIGHT HAND LAYOUT, RIGHT HAND POINT CLOSED.
(LAYOUT MÃO DIREITA, AGULHA DE MÃO DIREITA FECHADA)

NOTES (OBSERVAÇÕES):


1. ∠= ARRESTER (SUPRESSOR)
2. ALL HOUSE WIRING #14 UNLESS NOTED
   (TODOS CABOS DA HOUSE #1,5mm² A MENOS INDICADO)
3. #10 WIRING (CABO #6,0mm²)

MRS LOGISTICA S.A.

DESCRIÇÃO:	CIRCUITOS DA MÁQUINA DE CHAVE		
LOCAÇÃO:	P2–04A (1)		
DESIGN POR:	XORAIL	REVISÃO: 1	DATA: 22–JUN–11
CAD POR:	XORAIL	ARQUIVO:	EE–SD–FA–0FIN–116.13


P2–04A

KP 116+340

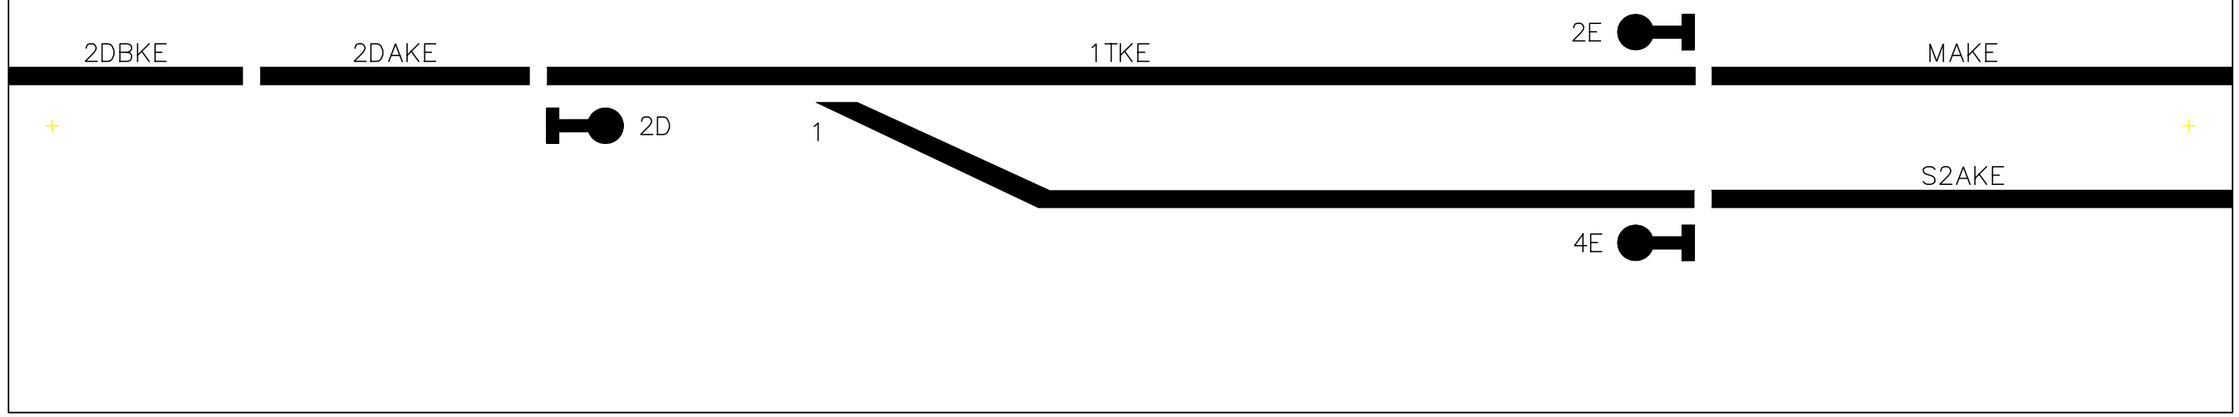

DESCRIÇÃO:	LAYOUT DO PAINEL DE CONTROLE LOCAL		
LOCAÇÃO:	P2–04A (1)		
DESIGN POR: XORAIL		REVISÃO: 1	DATA: 22–JUN–11
CAD POR: XORAIL		ARQUIVO:	EE–SD–FA–0FIN–116.14

LOCAL CONTROL PANEL
(PAINEL DE CONTROLE LOCAL)

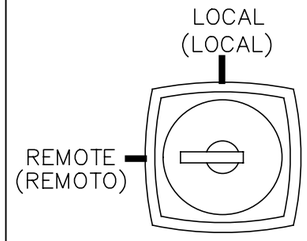

1 NORKE	1 REVKE	1 LKE	1 WLPKE	2D GKE	2E GKE	4E GKE	2D–2E–4E STOPKE	AER KE	1 TKE	2D AKE	2D BKE	M AKE		S2 AKE	
OFF															OFF
1NOR	1REV			2D SIG	2E SIG	4E SIG	2D–2E–4E STOP	AER							

LAMP TEST

START

LOCAL CONTROL PANEL EXPANSION
(PAINEL DE CONTROLE LOCAL EXPANSÃO)

1 TBK	1 SBKE	2D TBKE	2E TBKE	4E TBKE	DOOR ALRMKE	DD 1KE	DD 2KE	POKE	MOKE	2D LOKE	2E LOKE	4E LOKE	BLK POKE	LSRKE	INDKE
OFF															OFF
1TB	1SB	2DTB	2ETB	4ETB		DD1	DD2			2D BC	2E BC	4E BC		LSR RESET	IND ONLY

CONTROLS (CONTROLES)


1NOR = 1 SWITCH NORMAL CONTROL	(MAQUINA DE CHAVE 1 NORMAL)
1REV = 1 SWITCH REVERSE CONTROL	(MAQUINA DE CHAVE 1 REVERSA)
2DSIG = 2D SIGNAL REQUEST	(REQUISIÇÃO SINAL 2D)
2ESIG = 2E SIGNAL REQUEST	(REQUISIÇÃO SINAL 2E)
4ESIG = 4E SIGNAL REQUEST	(REQUISIÇÃO SINAL 4E)
2D–2E–4E STOP = ALL SIGNAL STOP REQUEST	(FECHAR TODOS OS SINAIS)
AER = ENGAGE APPROACH LIGHTING	(ACENDER SINAIS)
1TB = DETECTOR TRACK BLOCK (ON AND OFF)	(SEÇÃO DETECTORA BLOQUEADA)
1SB = 1 SWITCH BLOCK CONTROL	(MAQUINA DE CHAVE BLOQUEADA)
2DTB = 2D TRACK BLOCK CONTROL (ON AND OFF)	(VIA DE APROXIMAÇÃO 2D BLOQUEADA)
2ETB = 2E TRACK BLOCK CONTROL (ON AND OFF)	(VIA DE APROXIMAÇÃO 2E BLOQUEADA)
4ETB = 4E TRACK BLOCK CONTROL (ON AND OFF)	(VIA DE APROXIMAÇÃO 4E BLOQUEADA)
DD1 = DERAIL DETECTOR OVERRIDE 1	(IGNORAR DETECTOR DE DESCARRILHAMENTO 1)
DD2 = DERAIL DETECTOR OVERRIDE 2	(IGNORAR DETECTOR DE DESCARRILHAMENTO 2)
2DBC= 2D BLOCK CLEAR REQUEST	(REQUISIÇÃO BLOCO LIVRE 2D)
2EBC= 2E BLOCK CLEAR REQUEST	(REQUISIÇÃO BLOCO LIVRE 2E)
4EBC= 4E BLOCK CLEAR REQUEST	(REQUISIÇÃO BLOCO LIVRE 4E)
LSR RESET = LOCK STICK RELAY TIME RESET	(REINICIAR TEMPO LSR)
IND ONLY = LOCAL PANEL INDICATION ONLY	(SOMENTE INDICAÇÕES)


INDICATIONS (INDICAÇÕES)

1NORKE = 1 NORMAL SWITCH INDICATION	(MAQUINA DE CHAVE 1 NORMAL)
1REVKE = 1 REVERSE SWITCH INDICATION	(MAQUINA DE CHAVE 1 REVERSA)
1LKE = 1 SWITCH LOCK INDICATION	(MAQUINA DE CHAVE 1 LOCKED)
1WLPKE = 1 SWITCH HAND THROW INDICATION	(MAQUINA DE CHAVE 1 EM MANUAL)
2DGKE = 2D SIGNAL INDICATION	(SINAL 2D INDICAÇÃO)
2EGKE = 2E SIGNAL INDICATION	(SINAL 2E INDICAÇÃO)
4EGKE = 4E SIGNAL INDICATION	(SINAL 4E INDICAÇÃO)
2D–2E–4E STOPKE = ALL SIGNAL STOP INDICATION	(TODOS SINAIS FECHADOS)
AERKE = APPROACH LIGHTING INDICATION	(SINAIS ACENDIDOS)
1TKE = DETECTOR TRACK INDICATION	(SEÇÃO DETECTORA)
2DAKE = 2D APPROACH TRACK INDICATION	(VIA DE APROXIMAÇÃO 2D)
2DBKE = 2D ADVANCE APPROACH TRACK INDICATION	(VIA AVANÇADA DE APROXIMAÇÃO 2D)
MAKE = MAIN TRACK INDICATION	(INDICAÇÃO LINHA PRINCIPAL)
S2AKE = SIDING 2 TRACK INDICATION	(INDICAÇÃO LINHA SECUNDARIA 2)
1TBK = DETECTOR TRACK BLOCK INDICATION	(SEÇÃO DETECTORA BLOQUEADA)
1SBKE = 1 SWITCH BLOCK INDICATION	(MAQUINA DE CHAVE 1 BLOQUEADA)
2DTBKE = 2D TRACK BLOCK INDICATION	(VIA DE APROXIMAÇÃO 2D BLOQUEADA)
2ETBKE = 2E TRACK BLOCK INDICATION	(VIA DE APROXIMAÇÃO 2E BLOQUEADA)
4ETBKE = 4E TRACK BLOCK INDICATION	(VIA DE APROXIMAÇÃO 4E BLOQUEADA)
DOOR ALRMKE = DOOR ALARM INDICATION	(ALARME DE PORTA)
DD1KE = DERAIL DETECTOR 1 INDICATION	(DETECTOR DE DESCARRILHAMENTO 1)
DD2KE = DERAIL DETECTOR 2 INDICATION	(DETECTOR DE DESCARRILHAMENTO 2)
POKE = POWER OFF INDICATION	(FALTA DE ENERGIA)
MOKE = MANUAL OPERATE INDICATION	(OPERAÇÃO EM MANUAL)
2DLOKE = 2D SIGNAL LAMP OUT INDICATION	(LAMPADA QUEIMADA 2D)
2ELOKE = 2E SIGNAL LAMP OUT INDICATION	(LAMPADA QUEIMADA 2E)
4ELOKE = 4E SIGNAL LAMP OUT INDICATION	(LAMPADA QUEIMADA 4E)
BLKPOKE = BLOCK POWER OUT INDICATION	(FALTA DE ENERGIA NO BLOCO)
LSRKE = LSR RESET INDICATION	(INDICAÇÃO DO REINICIAR LSR)
INDKE = LOCAL CONTROL PANEL LED INDICATION ONLY	(SOMENTE INDICAÇÃO)

MRS LOGISTICA S.A.


DESCRIÇÃO:	PAINEL DE CONTROLE LOCAL E EXPANSÕES		
LOCAÇÃO:	P2–04A (1)		
DESIGN POR:	XORAIL	REVISÃO: 1	DATA: 22–JUN–11
CAD POR:	XORAIL	ARQUIVO:	EE–SD–FA–0FIN–116.15

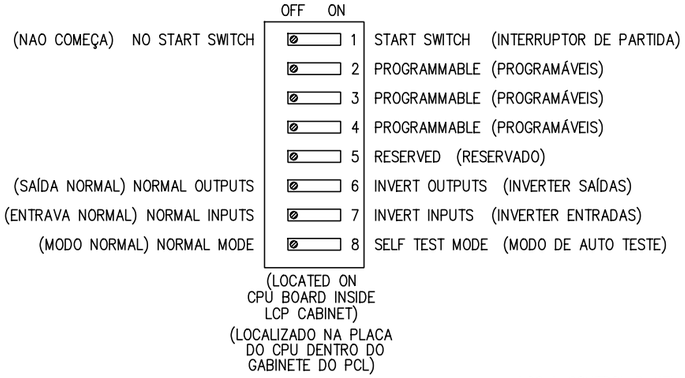


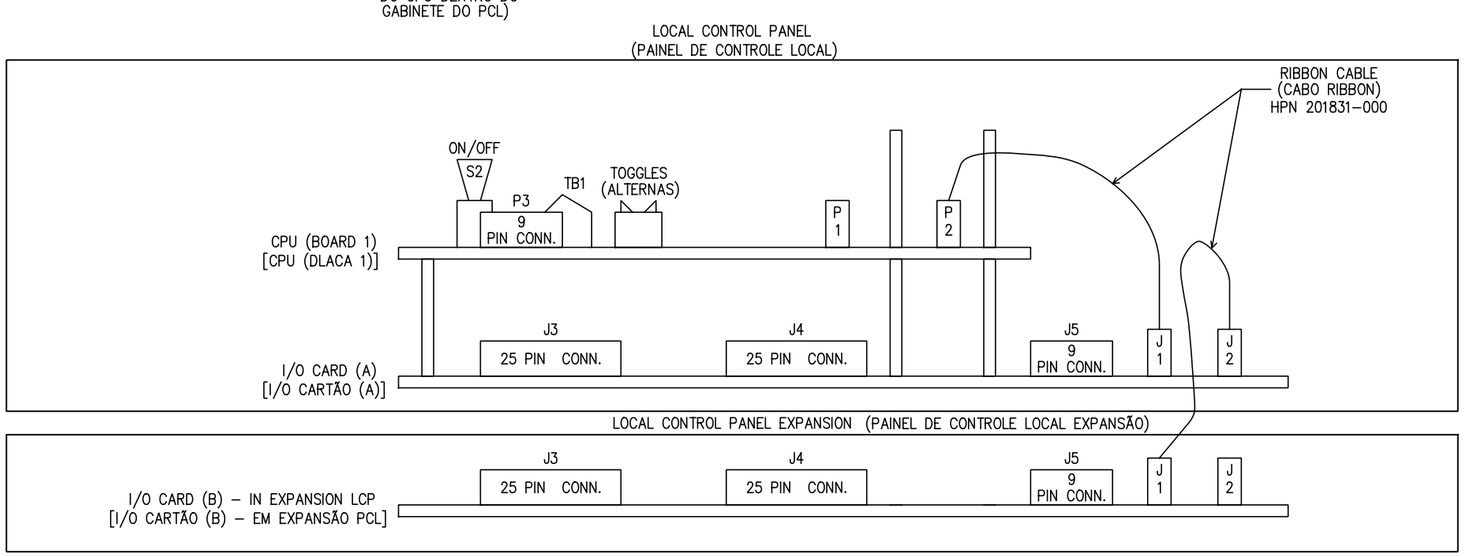

MRS LOGISTICA S.A.


DESCRIÇÃO:	MODULOS DO PAINEL DE CONTROLE LOCAL E EXPANSÕES		
LOCAÇÃO:	P2-04A (1)		
DESIGN POR:	XORAIL	REVISÃO: 1	DATA: 22-JUN-11
CAD POR:	XORAIL	ARQUIVO:	EE-SD-FA-0FIN-116.16

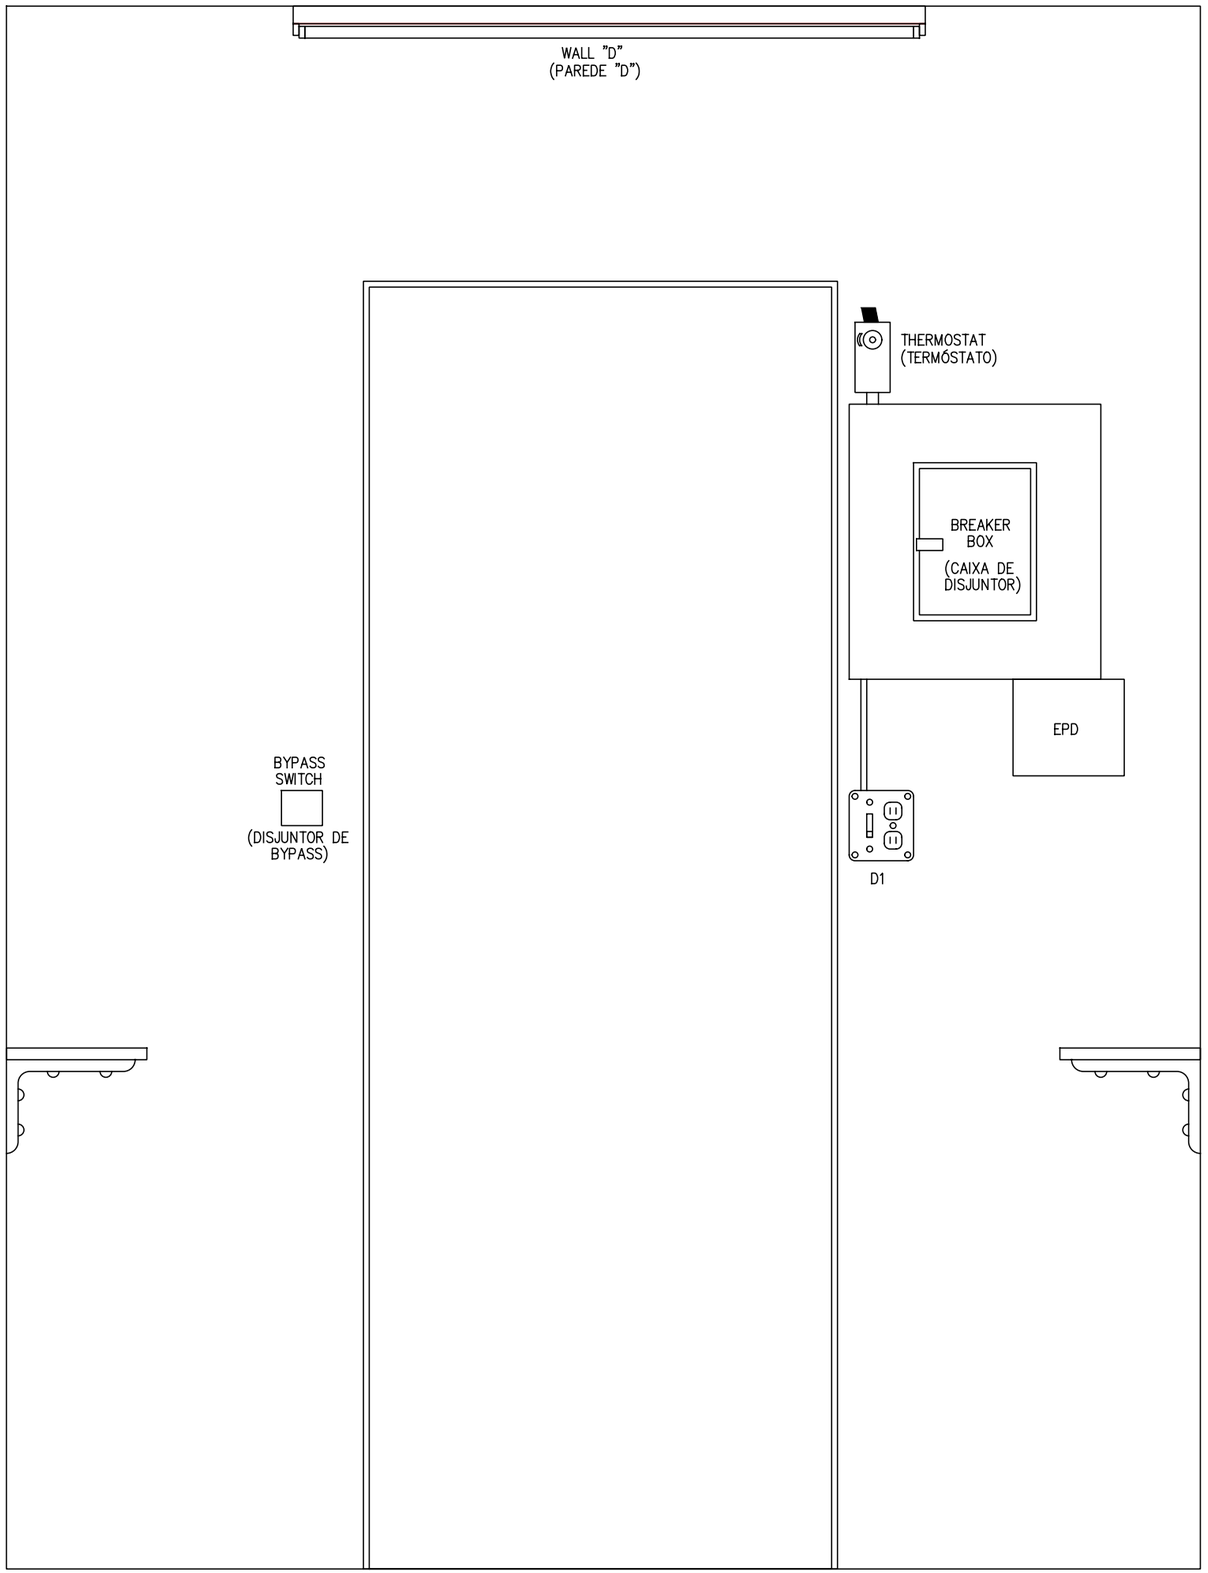

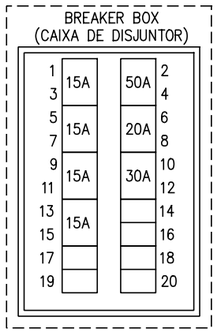


MRS LOGISTICA S.A.


DESCRIÇÃO:	HOUSE 6'X 6' LAYOUT DA PAREDE "D"		
LOCAÇÃO:	P2-04A (1)		
DESIGN POR:	XORAIL	REVISÃO: 1	DATA: 22-JUN-11
CAD POR:	XORAIL	ARQUIVO:	EE-SD-FA-0FIN-116.17

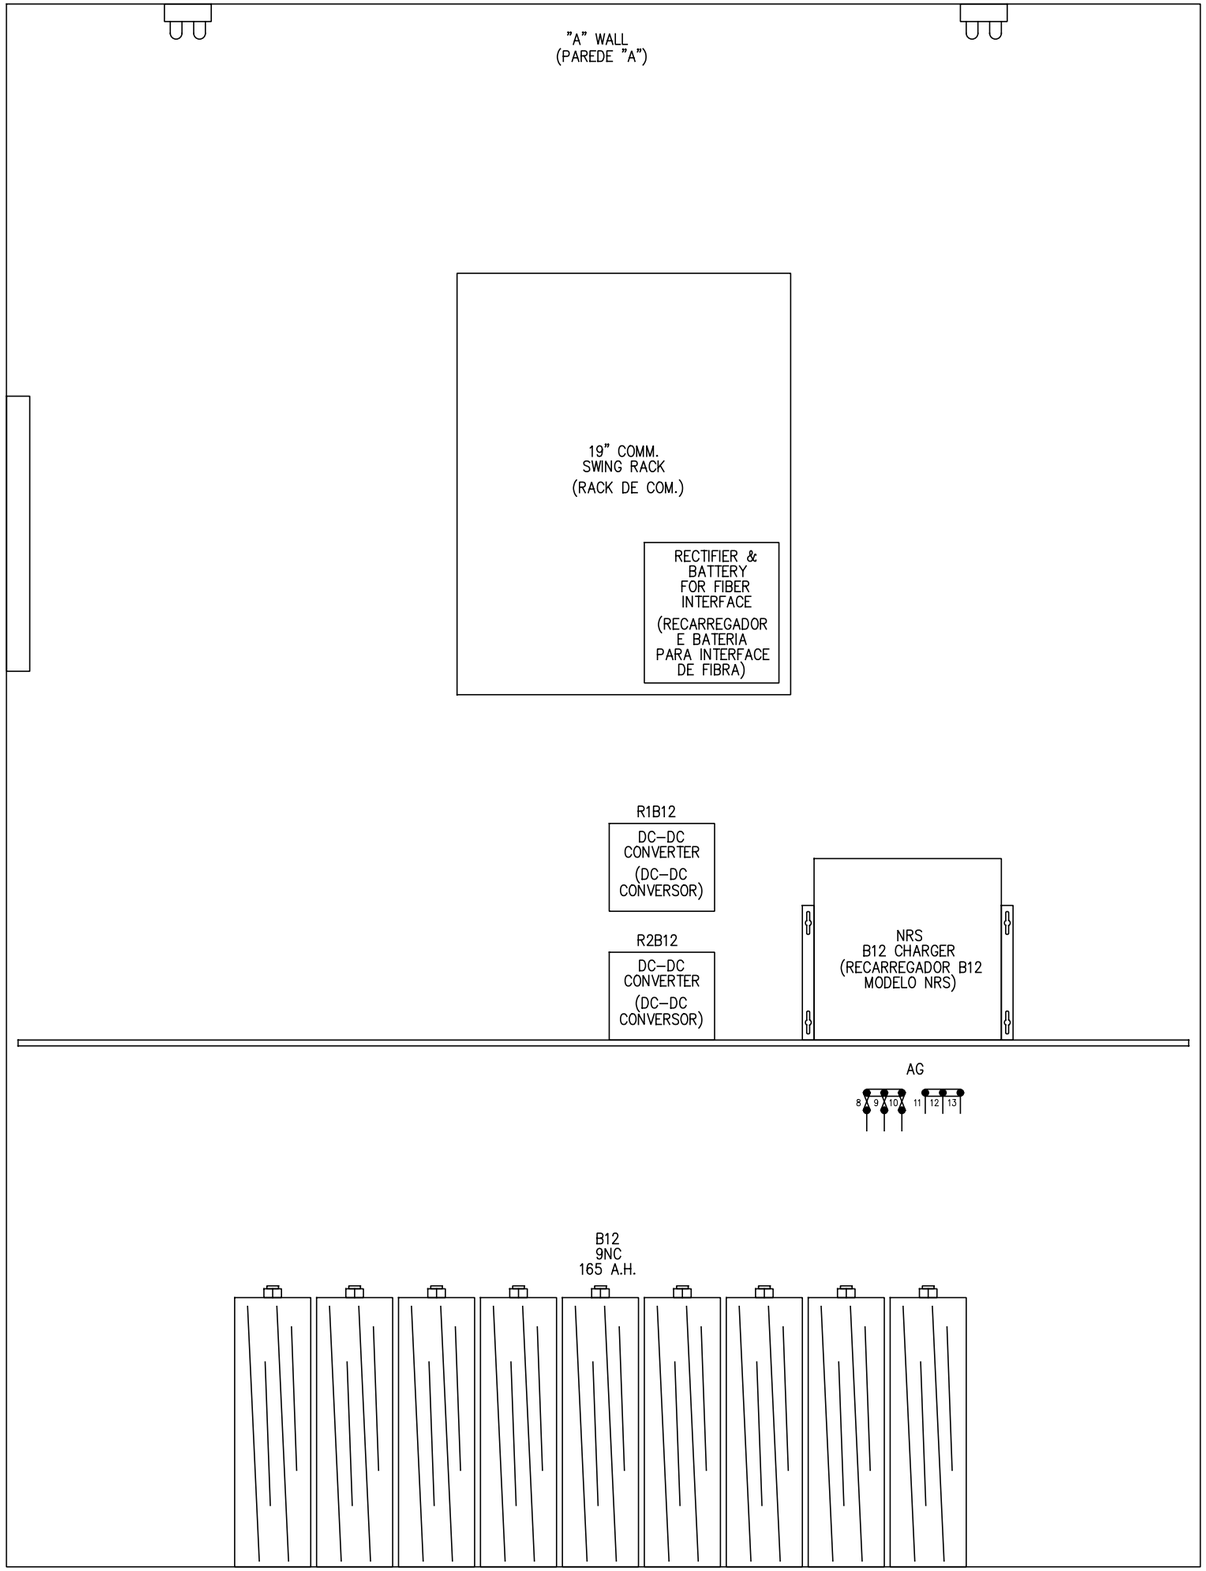

MRS LOGISTICA S.A.


DESCRIÇÃO:	HOUSE 6'X 6' LAYOUT DA PAREDE "A"		
LOCAÇÃO:	P2–04A (1)		
DESIGN POR:	XORAIL	REVISÃO: 1	DATA: 22–JUN–11
CAD POR:	XORAIL	ARQUIVO:	EE–SD–FA–0FIN–116.18

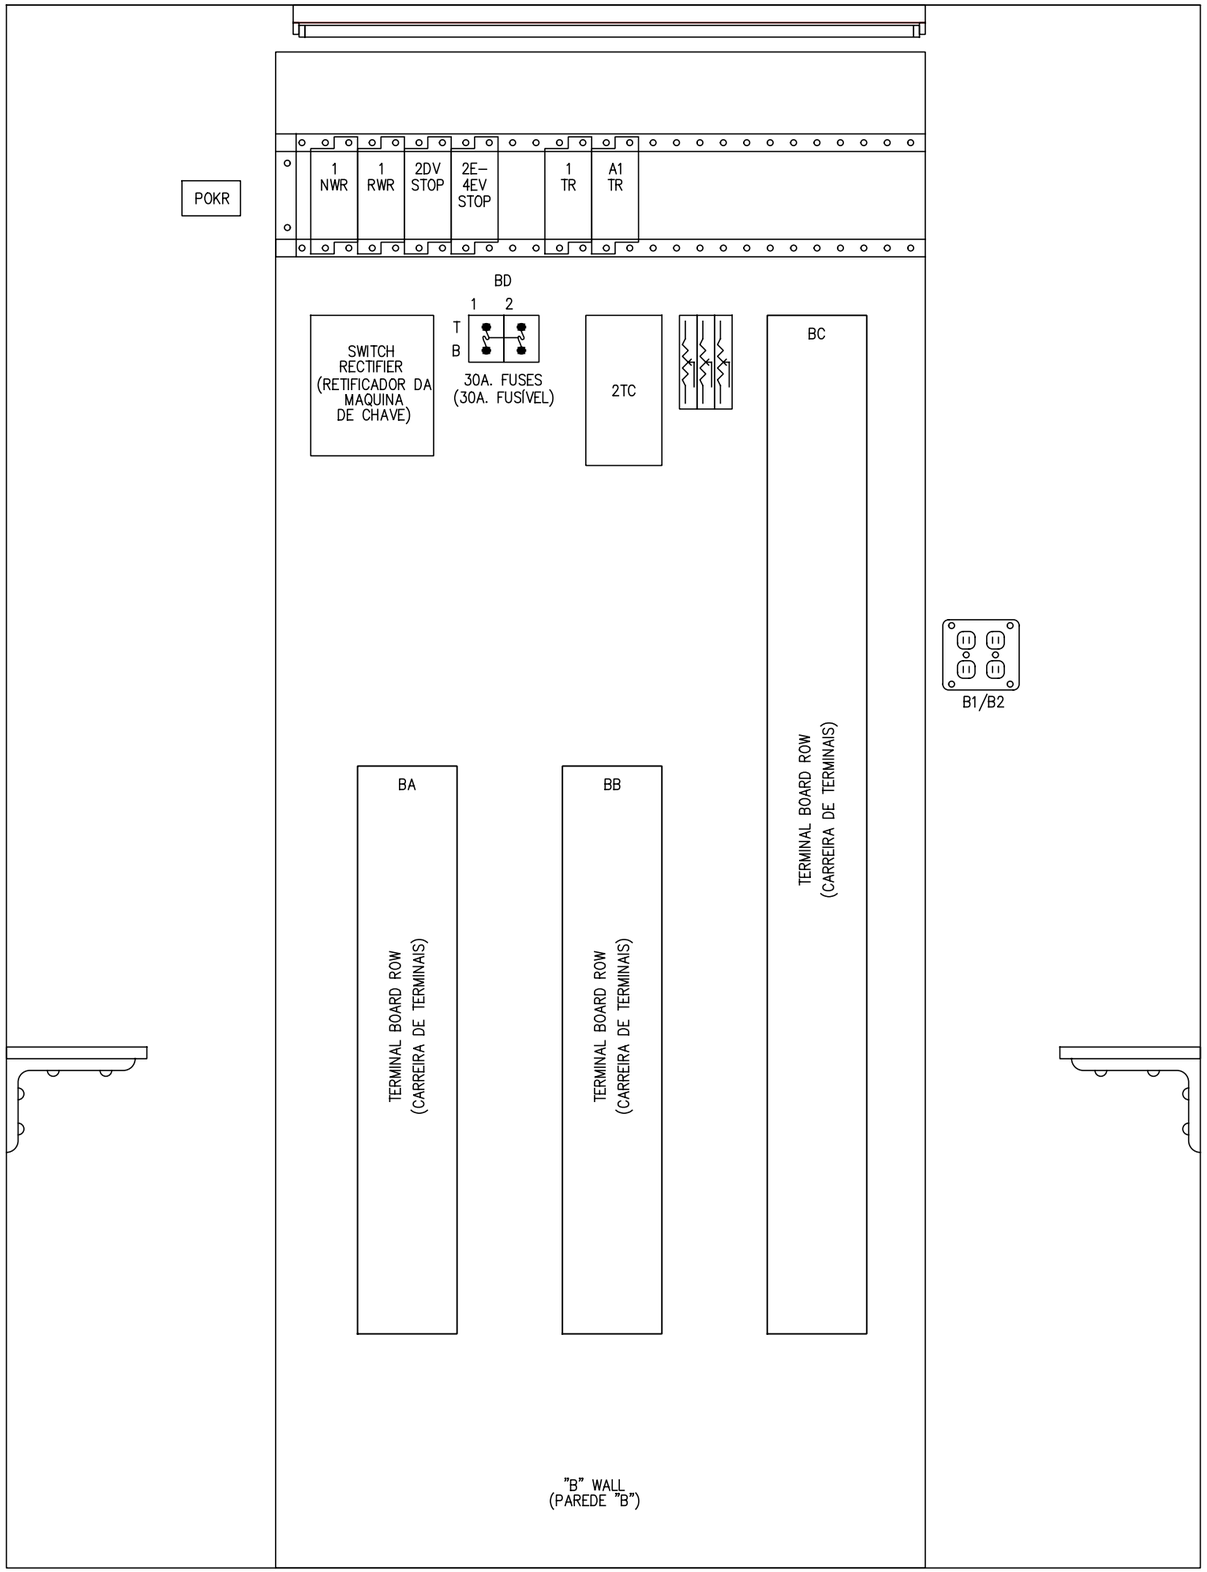

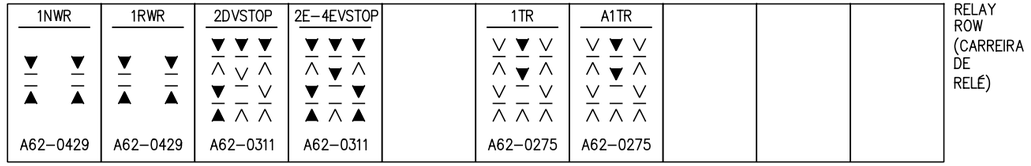

RELAY LEGEND
(LEGENDA DE RELÉ)

▼ = FRONT CONTACT USED (CONTATO FRONT UTILIZADO)
⋁ = FRONT CONTACT NOT USED (CONTATO FRONT NÃO UTILIZADO)
— = HEEL (CALCANHAR)
⋀ = BACK CONTACT NOT USED (CONTATO BACK NÃO UTILIZADO)
▲ = BACK CONTACT USED (CONTATO BACK UTILIZADO)

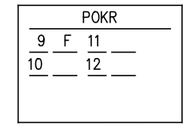

KHAU–17A12–120
27E166 WALL MOUNT
(27E166 MONTADO NA PAREDE)

MRS LOGISTICA S.A.

DESCRIÇÃO:	HOUSE 6'X 6' LAYOUT DA PAREDE "B"		
LOCAÇÃO:	P2–04A (1)		
DESIGN POR:	XORAIL	REVISÃO: 1	DATA: 22–JUN–11
CAD POR:	XORAIL	ARQUIVO:	EE–SD–FA–0FIN–116.19

"C" WALL
(PAREDE "C")

WABTEC IMG-2
&
PTC RADIO

(PTC RACK DE COM.)

1
TIP-2

2
TIP-2

CLC

RS 900

LOCAL CONTROL PANEL LAYOUT
(LAYOUT DO PAINEL DE CONTROLE LOCAL)

LOCAL CONTROL PANEL
(PAINEL DE CONTROLE LOCAL)


LOCAL CONTROL PANEL EXPANSION
(PAINEL DE EXPANSÃO DE CONTROLE LOCAL)


PERSONALITY MODULES
(MODULOS DE TERMINAIS)


1	2	3	4	5	6	7	8	9
VTI-2S	VTI-2S	VLD-R16S				VIO-86S		
CPS-3	CDU-1	VPM-3		CIO-1A			XCI-2	


MRS LOGISTICA S.A.

DESCRIÇÃO:	HOUSE 6'X 6' LAYOUT DA PAREDE "C"		
LOCAÇÃO:	P2-04A (1)		
DESIGN POR: XORAIL		REVISÃO: 1	DATA: 22-JUN-11
CAD POR: XORAIL		ARQUIVO:	EE-SD-FA-0FIN-116.20

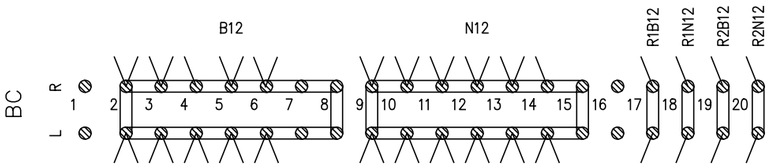

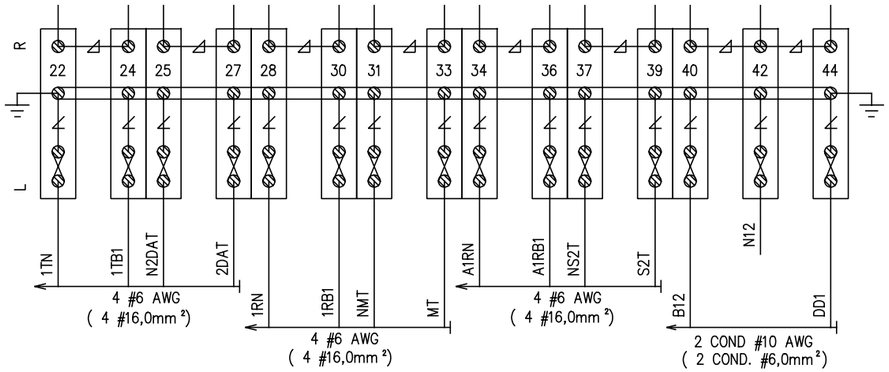

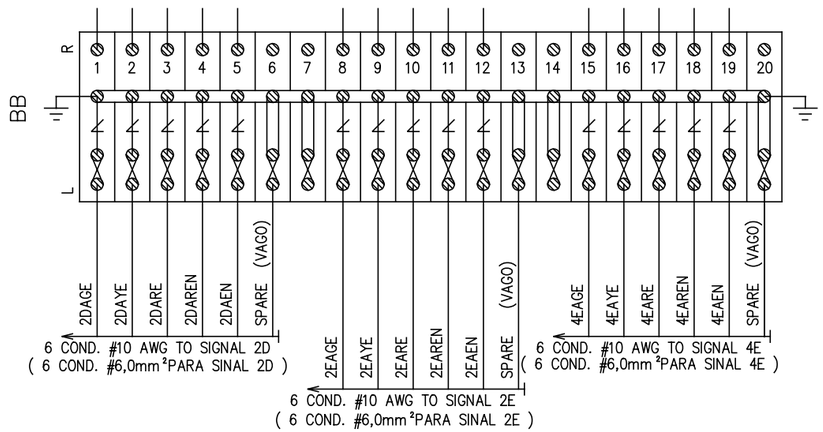

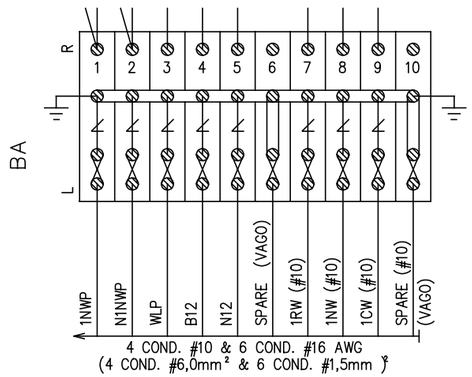

NOMENCLATURE LEGEND
(LEGENDA DE NOMENCLATURA)

L B D 4 T R

(ESQUERDA) LEFT — RIGHT (DIREITA)
(INFERIOR) BOTTOM — TOP (SUPERIOR)
(CARREIRA) ROW — TERMINAL NUMBER (NUMERO DA TERMINAL)

NOTES:

- ∠ = ARRESTER (SUPRESSOR)
- ◿ = EQUALIZER (EQUALIZADOR)
- ⊘ = TERMINAL POST (PINO DE TERMINAL)
- ⊘—⊘ = TEST LINK (LINK DE TESTE)
- ⊘═⊘ = SOLID LINK (LINK SOLIDO)
- L = LEFT (ESQUERDA)
- R = RIGHT (DIREITA)
- ⏚ = GROUND (TERRA)

MRS LOGISTICA S.A.

DESCRIÇÃO:	DETALHE DO PAINEL DE TERMINAIS [TB]		
LOCAÇÃO:	P2–04A (1)		
DESIGN POR:	XORAIL	REVISÃO: 1	DATA: 22–JUN–11
CAD POR:	XORAIL	ARQUIVO:	EE–SD–FA–0FIN–116.21