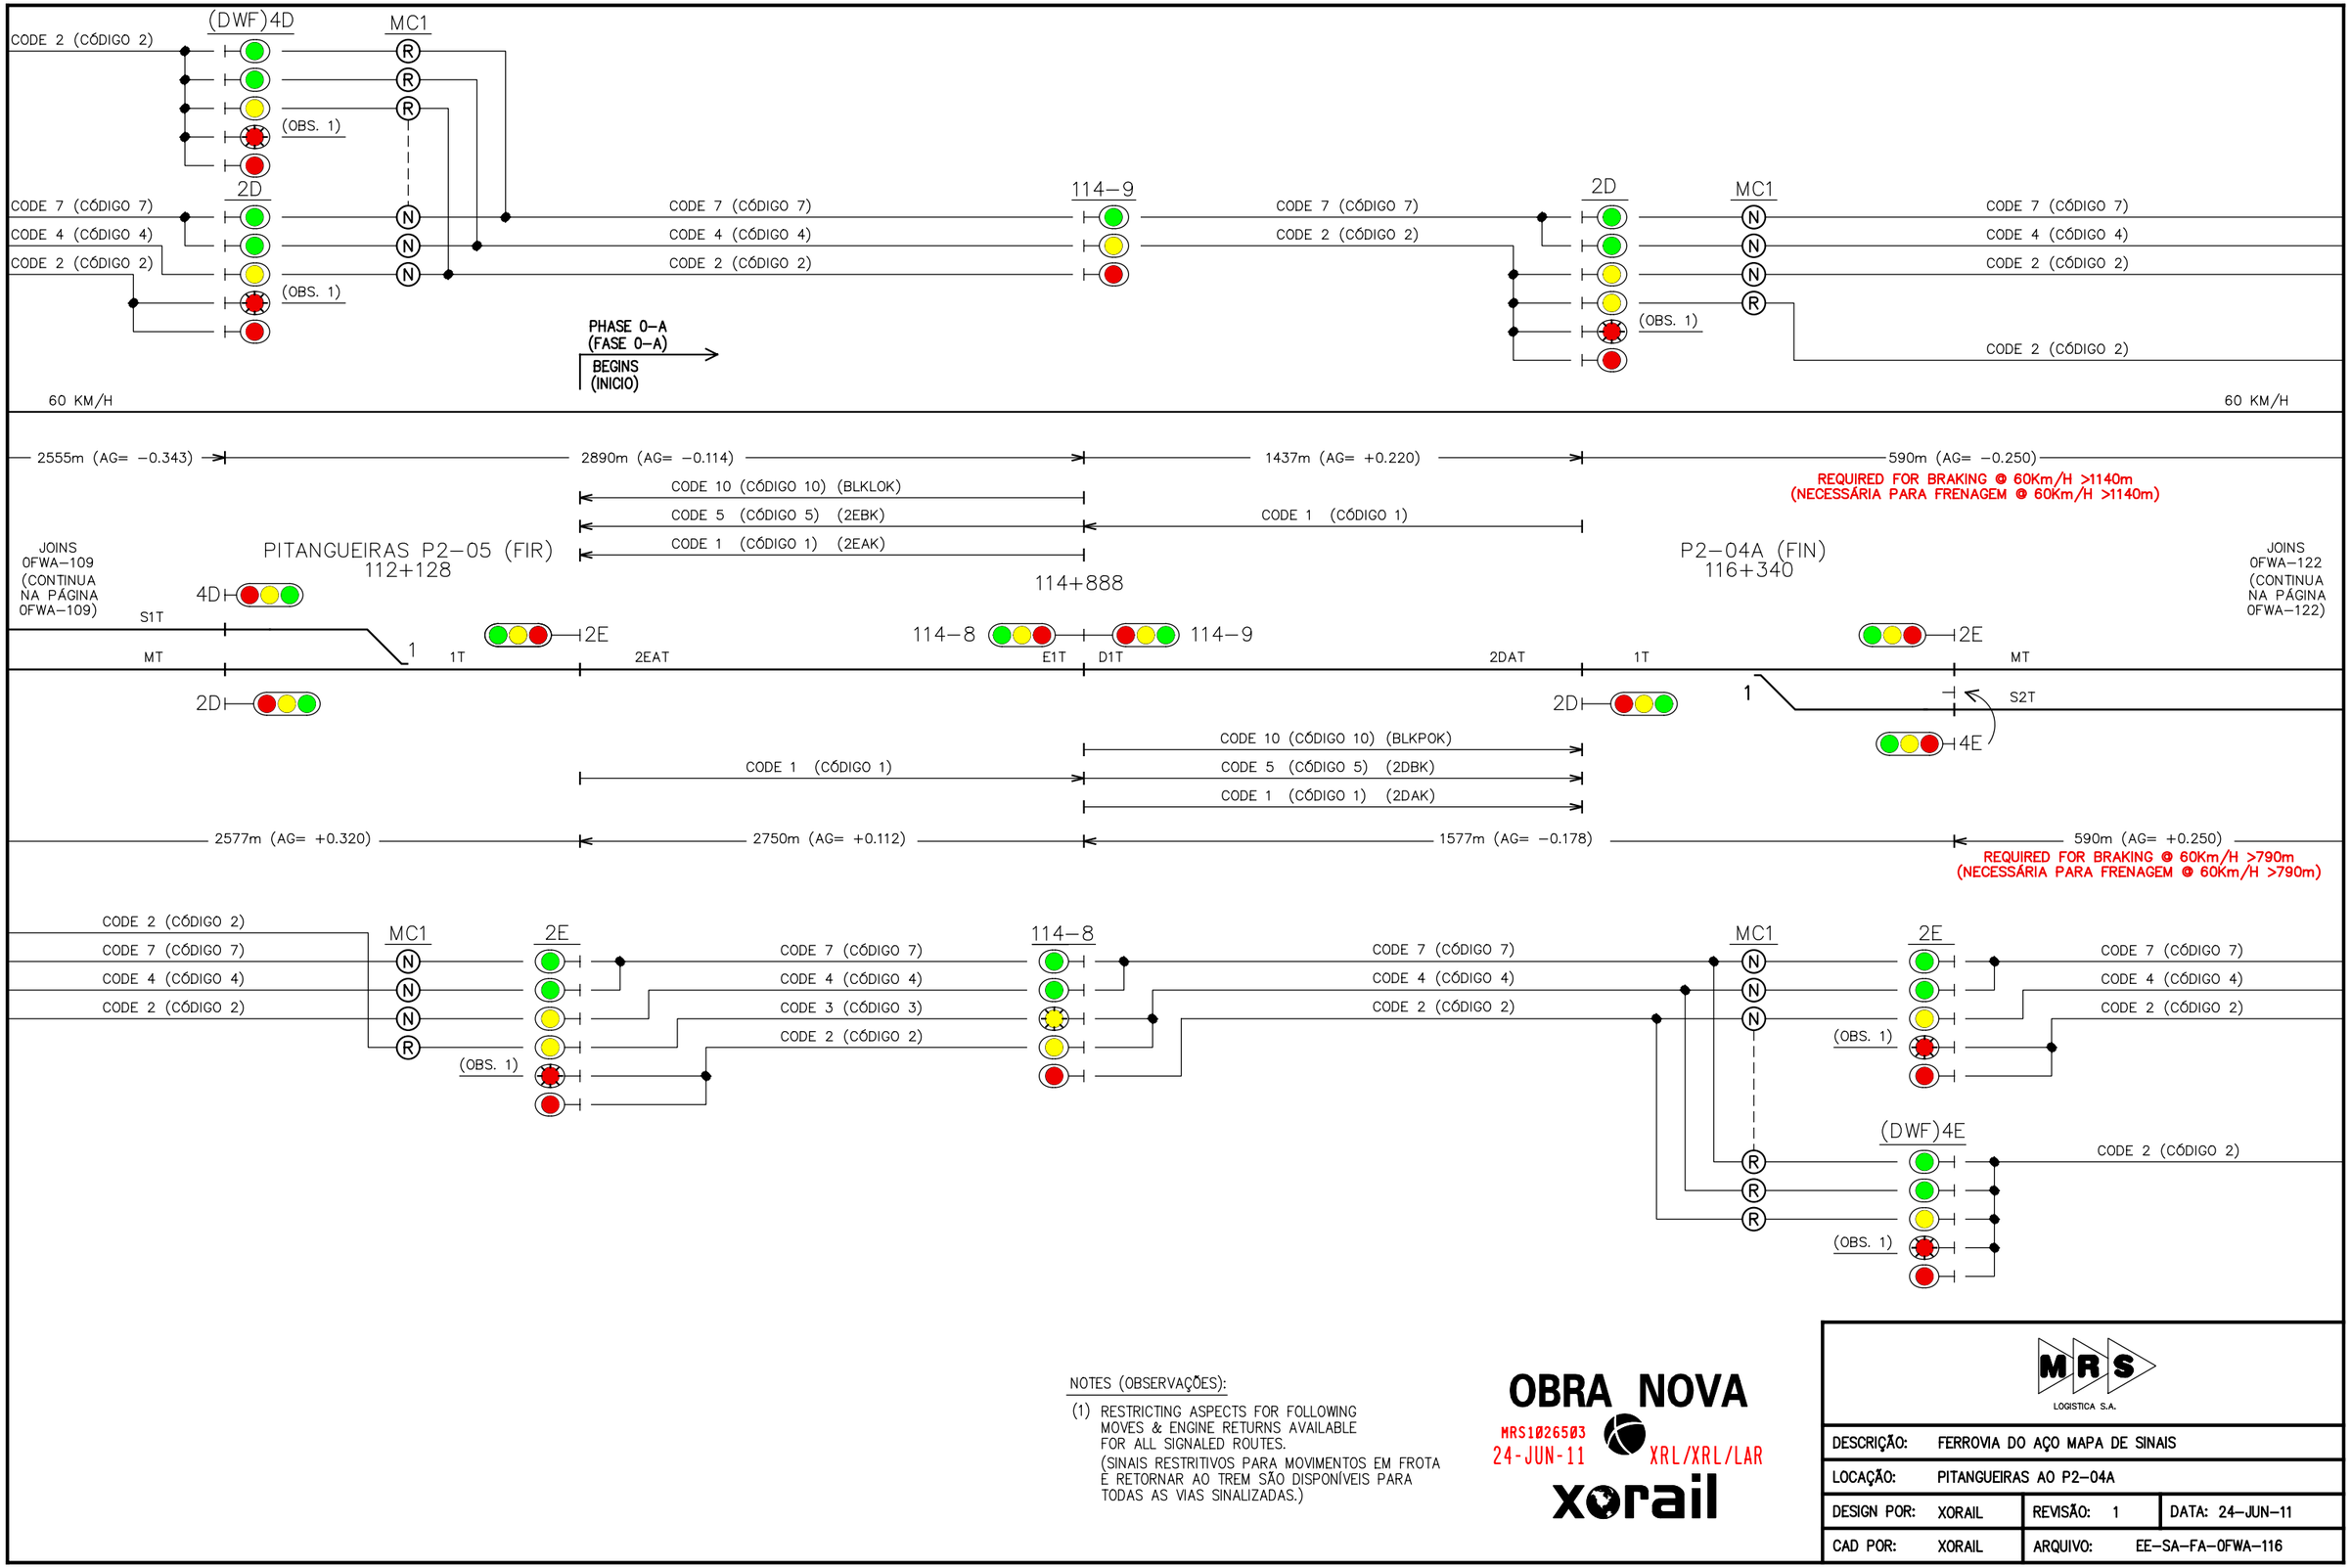


NOTES (OBSERVAÇÕES):

(1) RESTRICTING ASPECTS FOR FOLLOWING MOVES & ENGINE RETURNS AVAILABLE FOR ALL SIGNALED ROUTES.
(SINAIS RESTRITIVOS PARA MOVIMENTOS EM FROTA E RETORNAR AO TREM SÃO DISPONÍVEIS PARA TODAS AS VIAS SINALIZADAS.)


OBRA NOVA

MRS1026503
24-JUN-11 XRL/XRL/LAR

xorail

MRS LOGISTICA S.A.

DESCRIÇÃO:	FERROVIA DO AÇO MAPA DE SINAIS		
LOCAÇÃO:	PITANGUEIRAS AO P2–04A		
DESIGN POR:	XORAIL	REVISÃO: 1	DATA: 24–JUN–11
CAD POR:	XORAIL	ARQUIVO:	EE–SA–FA–0FWA–116

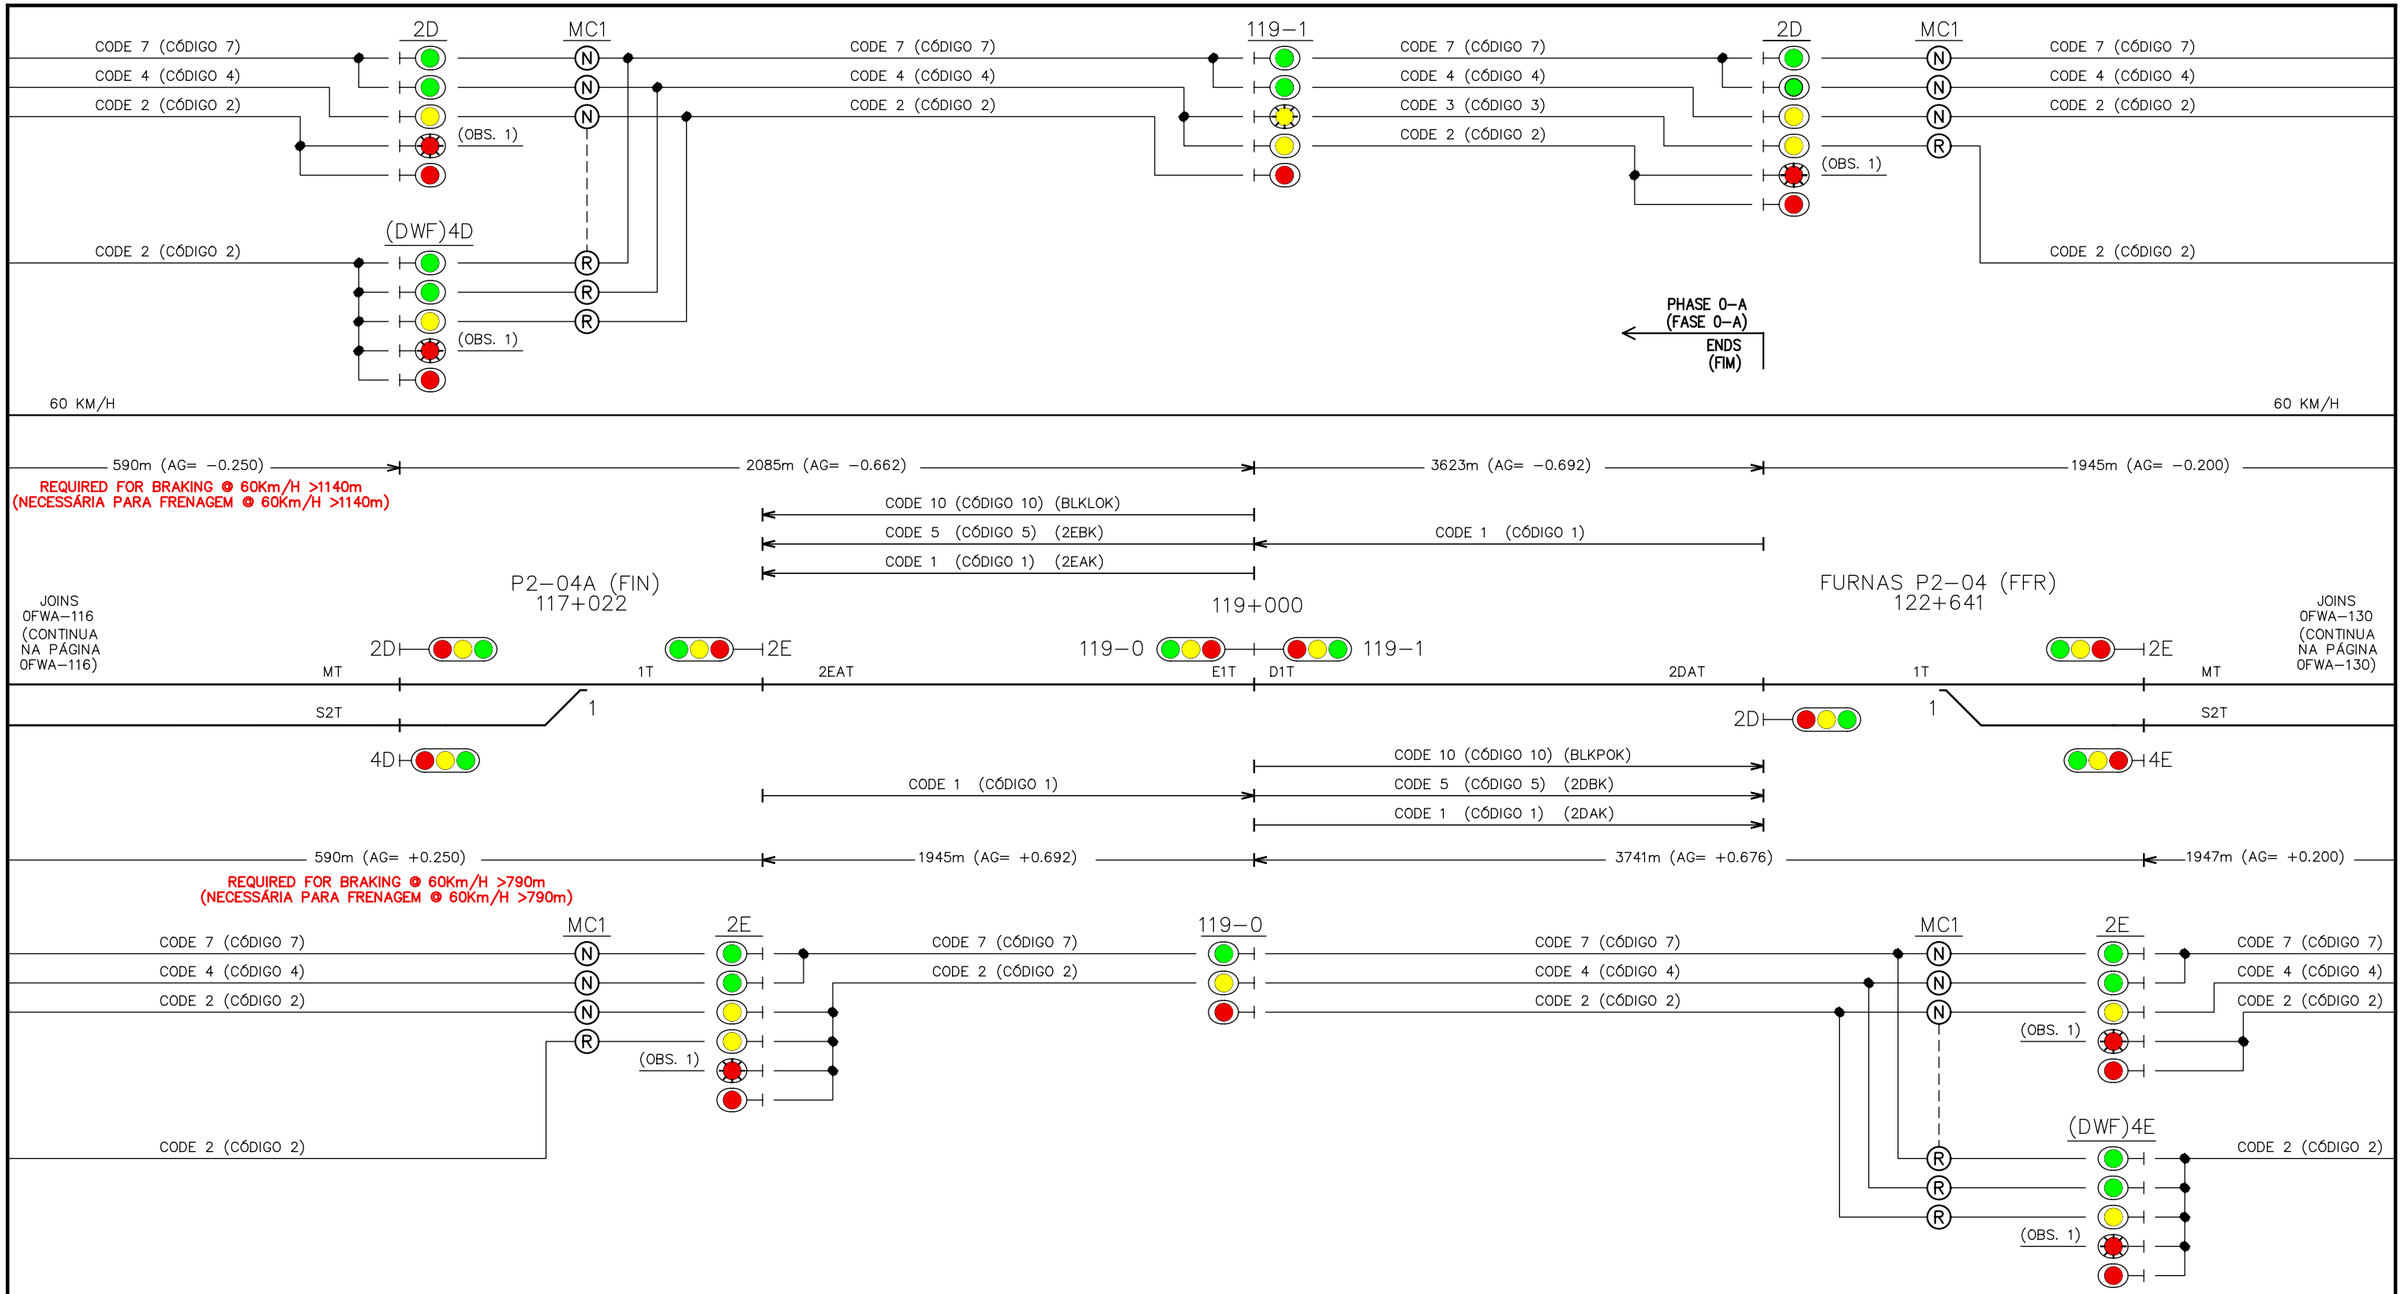

NOTES (OBSERVAÇÕES):

(1) RESTRICTING ASPECTS FOR FOLLOWING MOVES & ENGINE RETURNS AVAILABLE FOR ALL SIGNALED ROUTES.
(SINAIS RESTRITIVOS PARA MOVIMENTOS EM FROTA E RETORNAR AO TREM SÃO DISPONÍVEIS PARA TODAS AS VIAS SINALIZADAS.)

OBRA NOVA

MRS1026503
24-JUN-11 XRL/XRL/LAR

xorail

MRS LOGISTICA S.A.

DESCRIÇÃO:	FERROVIA DO AÇO MAPA DE SINAIS		
LOCAÇÃO:	P2–04A AO FURNAS		
DESIGN POR:	XORAIL	REVISÃO: 1	DATA: 24–JUN–11
CAD POR:	XORAIL	ARQUIVO:	EE–SA–FA–0FWA–122