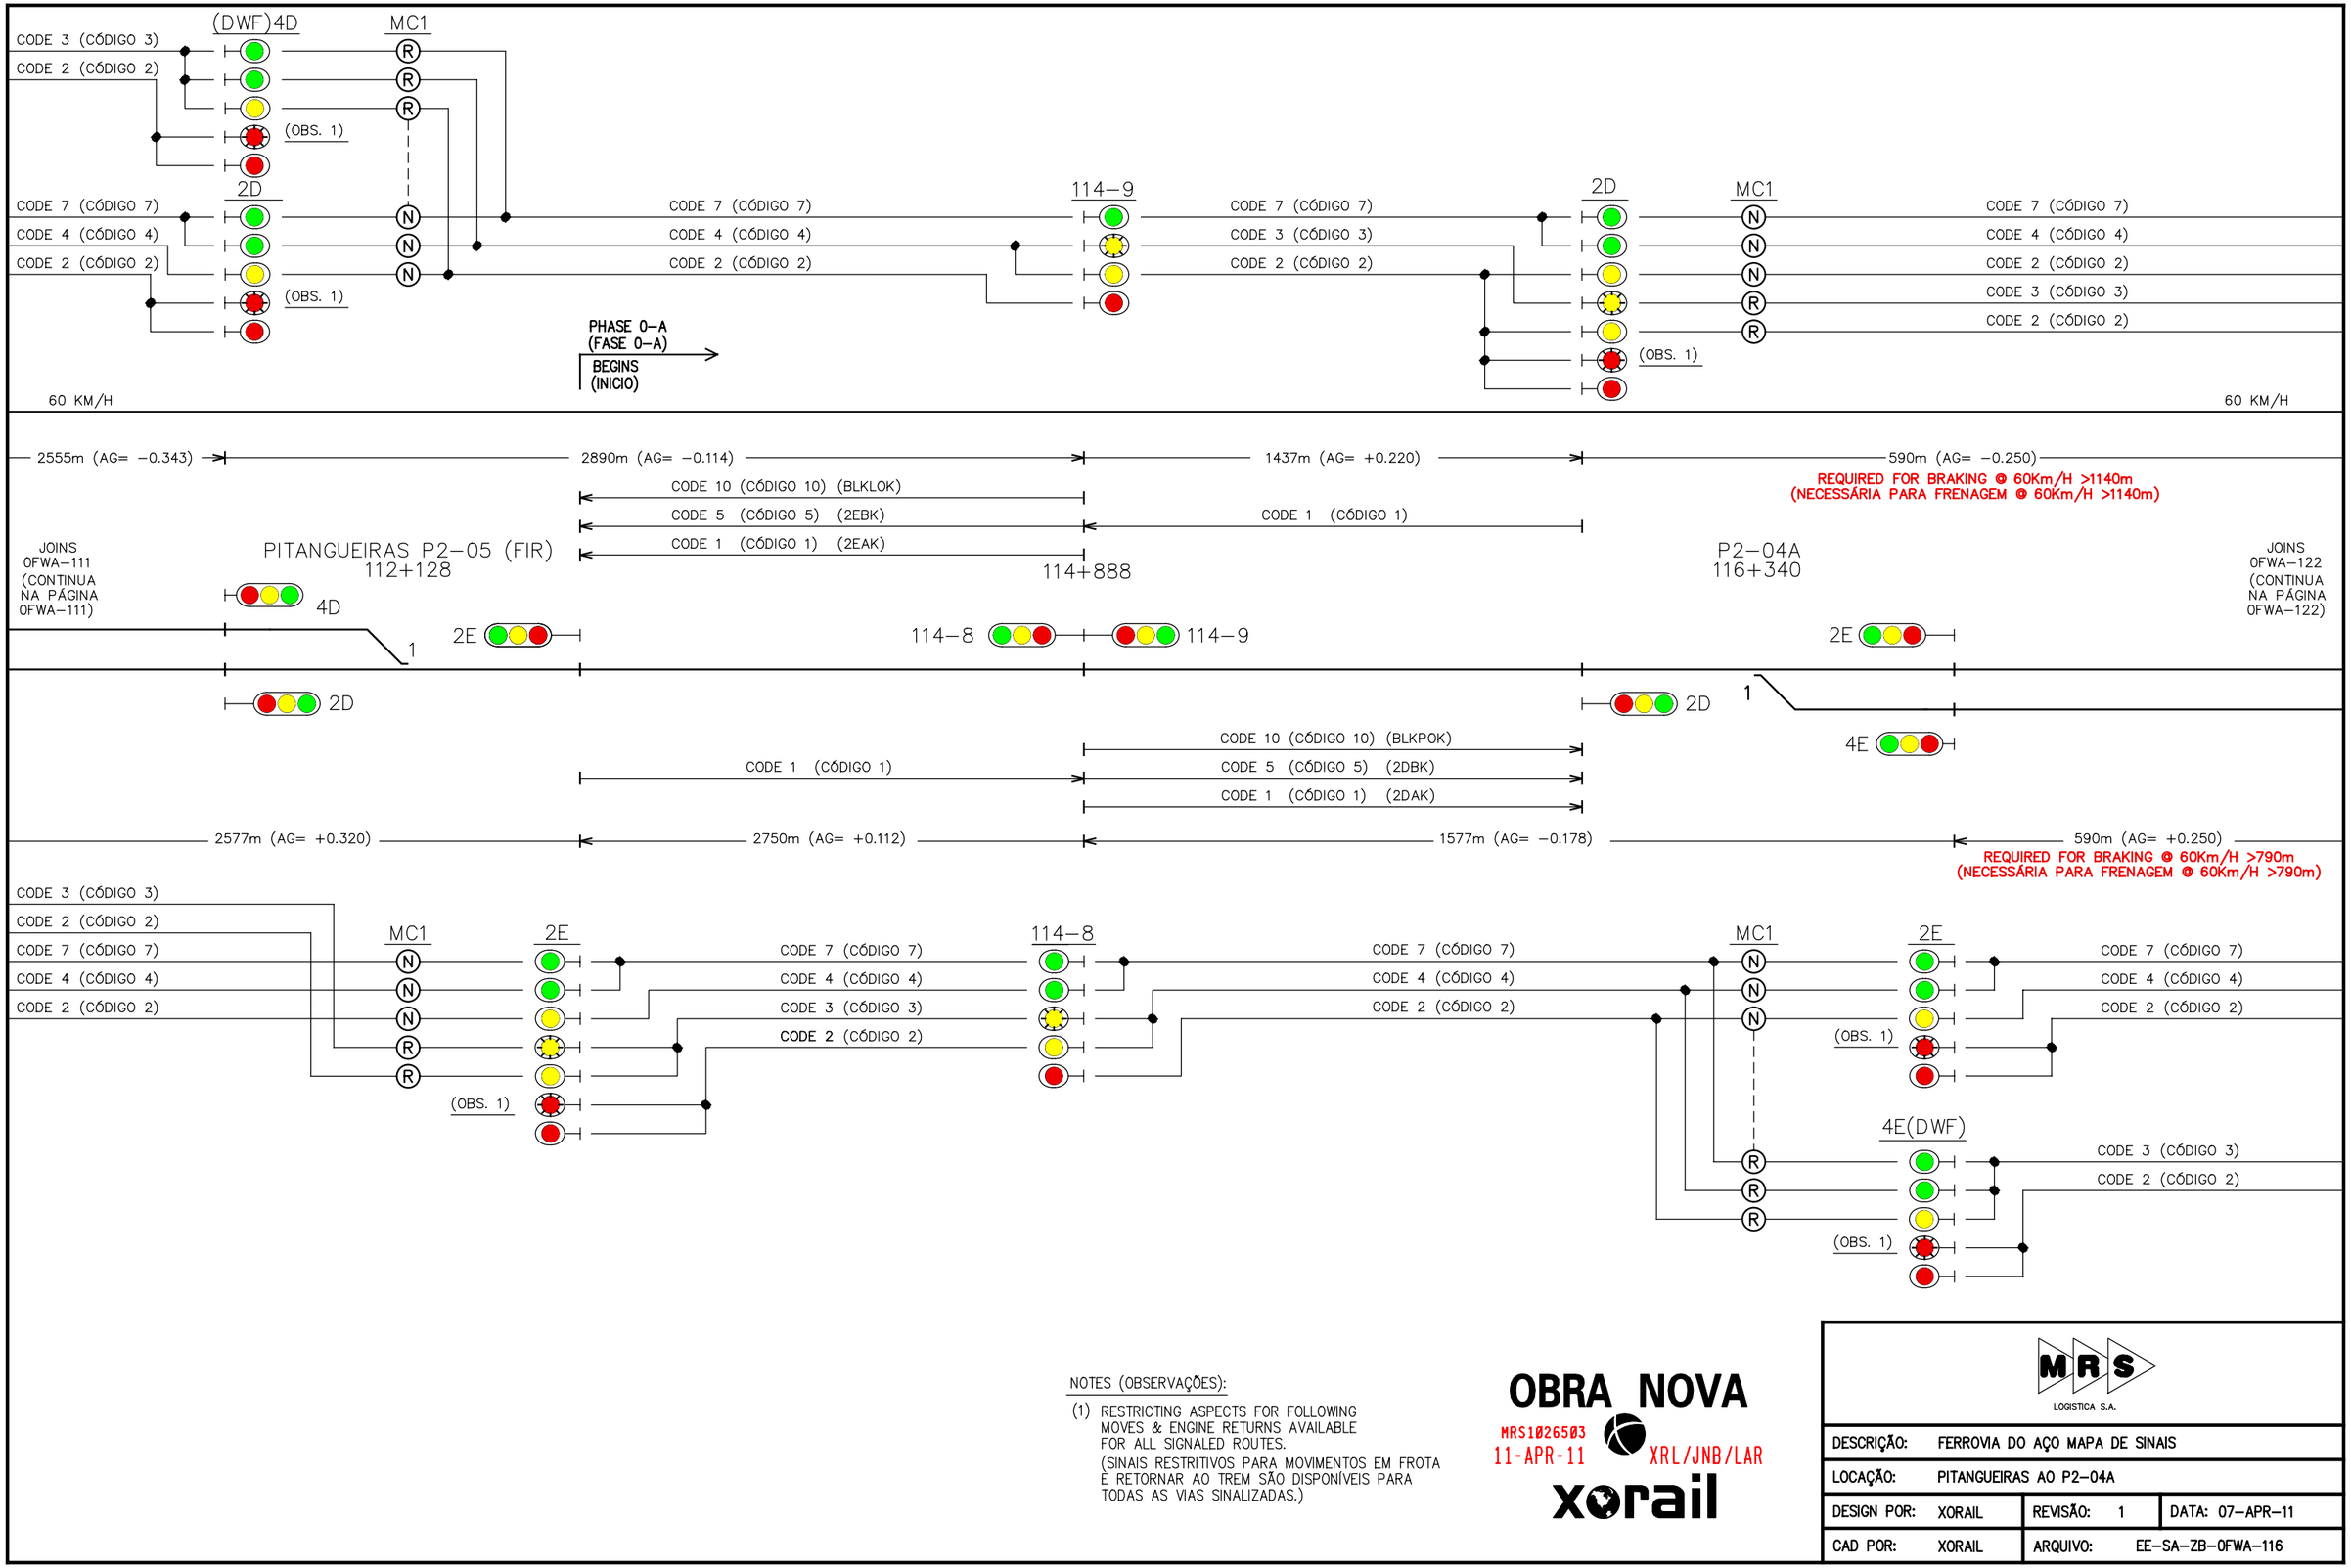


NOTES (OBSERVAÇÕES):

(1) RESTRICTING ASPECTS FOR FOLLOWING MOVES & ENGINE RETURNS AVAILABLE FOR ALL SIGNALED ROUTES.
(SINAIS RESTRITIVOS PARA MOVIMENTOS EM FROTA E RETORNAR AO TREM SÃO DISPONÍVEIS PARA TODAS AS VIAS SINALIZADAS.)


OBRA NOVA

MRS1026503
11-APR-11 XRL/JNB/LAR

xorail

MRS LOGISTICA S.A.

DESCRIÇÃO:	FERROVIA DO AÇO MAPA DE SINAIS		
LOCAÇÃO:	PITANGUEIRAS AO P2-04A		
DESIGN POR:	XORAIL	REVISÃO: 1	DATA: 07-APR-11
CAD POR:	XORAIL	ARQUIVO:	EE-SA-ZB-0FWA-116

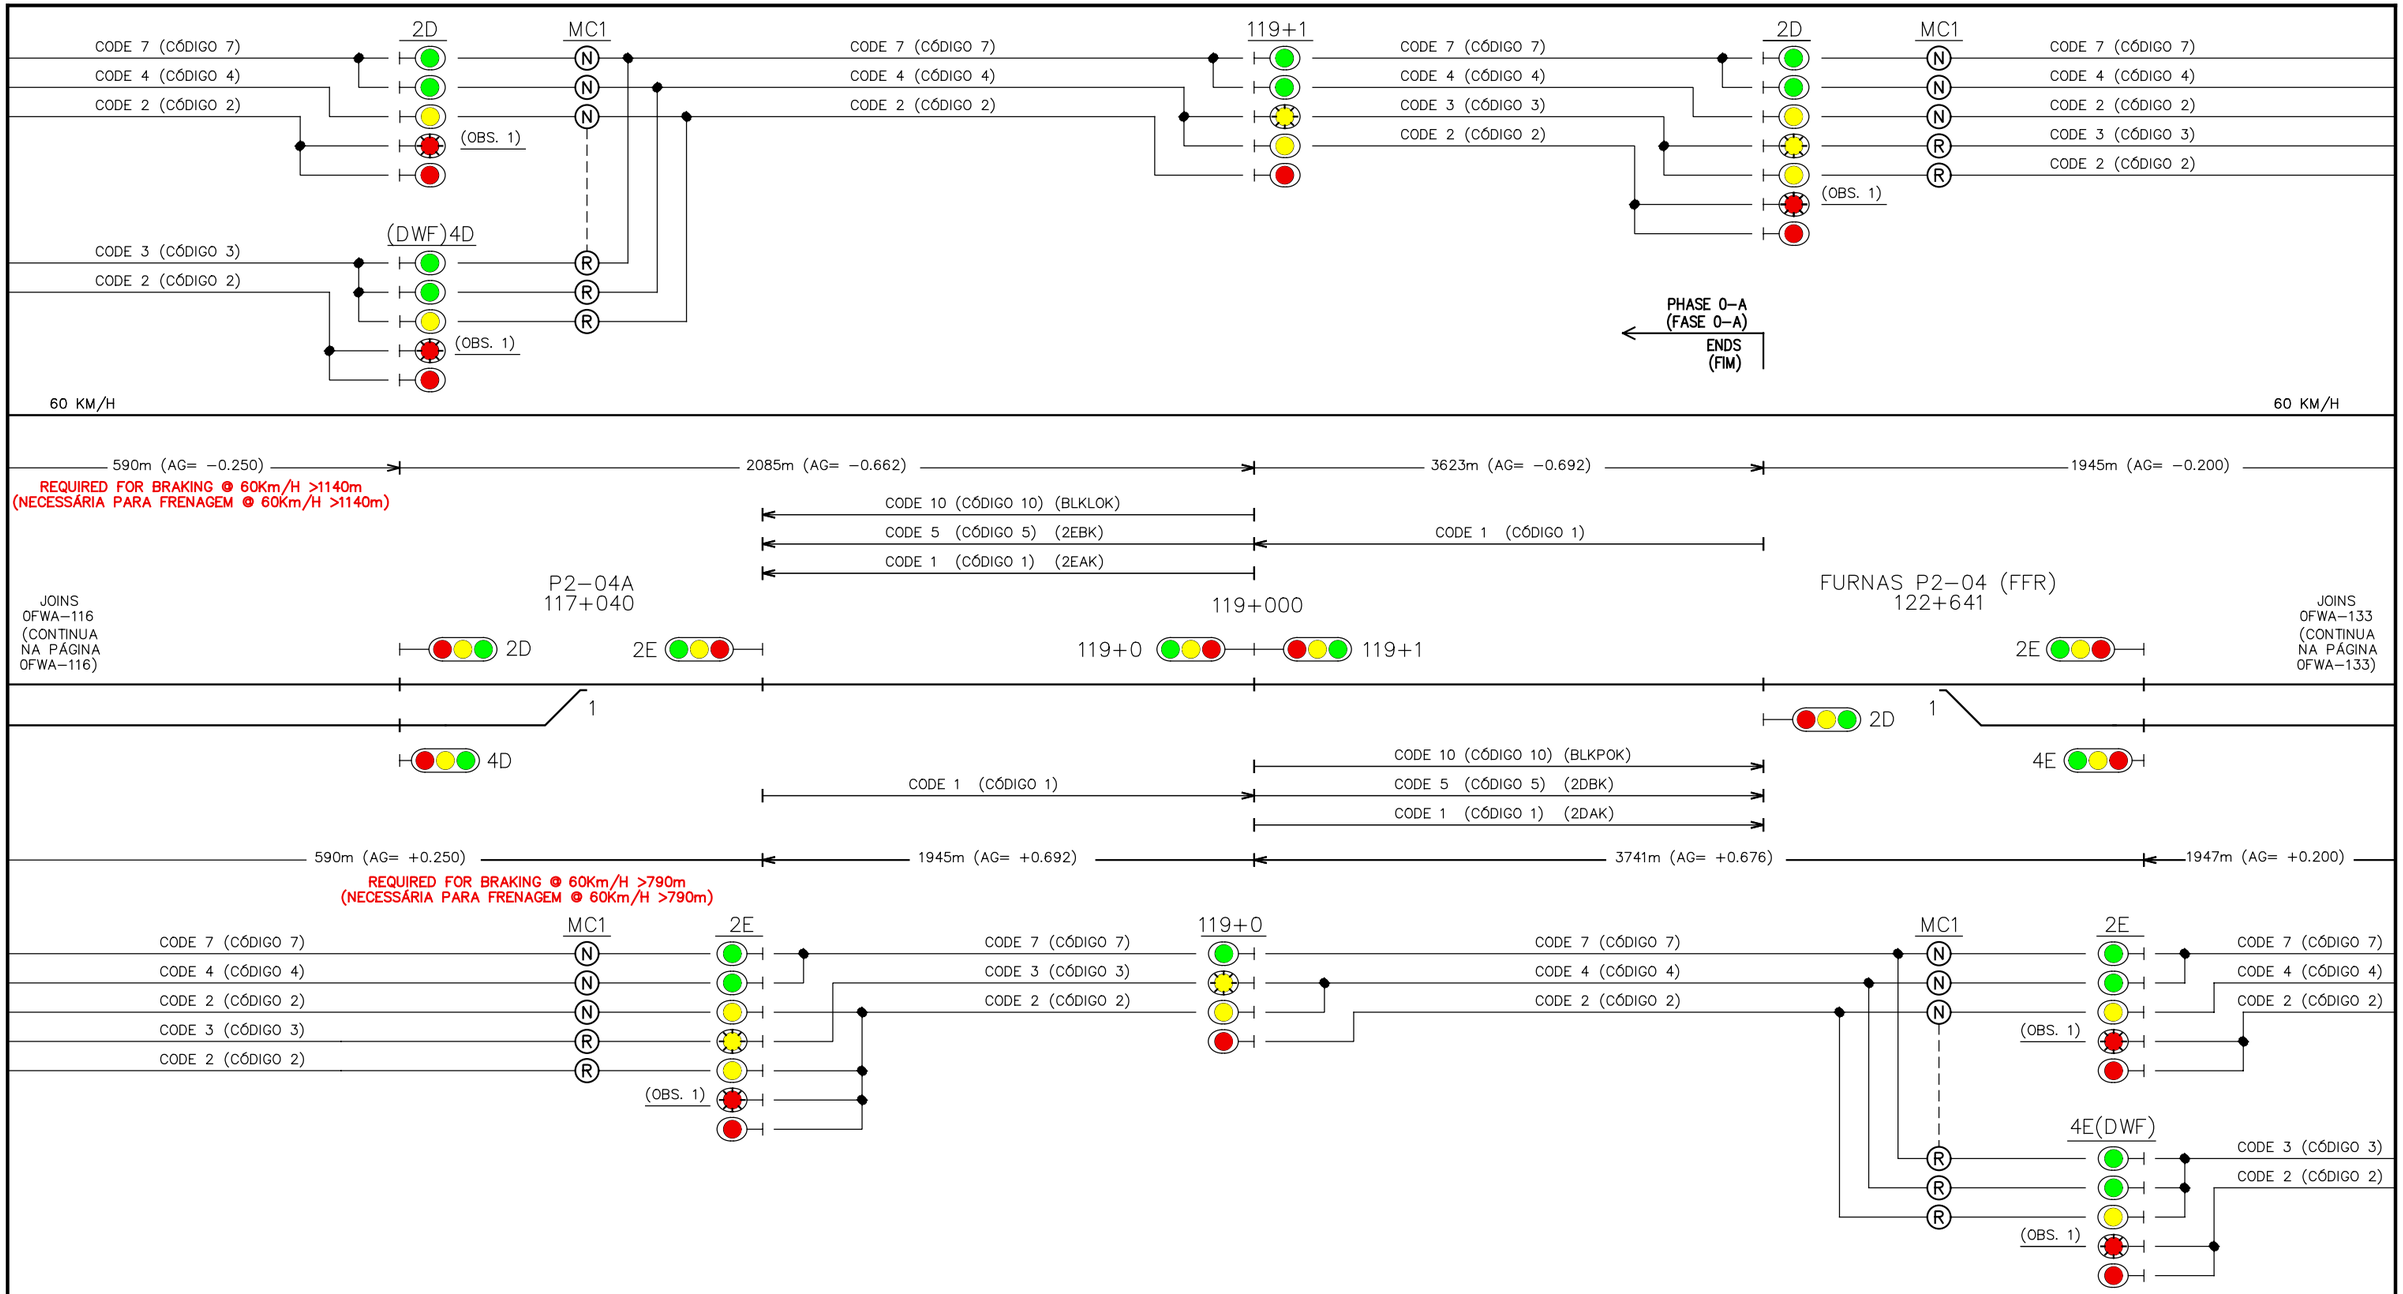

NOTES (OBSERVAÇÕES):

(1) RESTRICTING ASPECTS FOR FOLLOWING MOVES & ENGINE RETURNS AVAILABLE FOR ALL SIGNALED ROUTES.
(SINAIS RESTRITIVOS PARA MOVIMENTOS EM FROTA E RETORNAR AO TREM SÃO DISPONÍVEIS PARA TODAS AS VIAS SINALIZADAS.)


OBRA NOVA

MRS1026503
11-APR-11 XRL/JNB/LAR

xorail

MRS LOGISTICA S.A.

DESCRIÇÃO:	FERROVIA DO AÇO MAPA DE SINAIS		
LOCAÇÃO:	P2-04A AO FURNAS		
DESIGN POR: XORAIL	REVISÃO: 1	DATA: 07-APR-11	
CAD POR: XORAIL	ARQUIVO: EE-SA-ZB-0FWA-122		

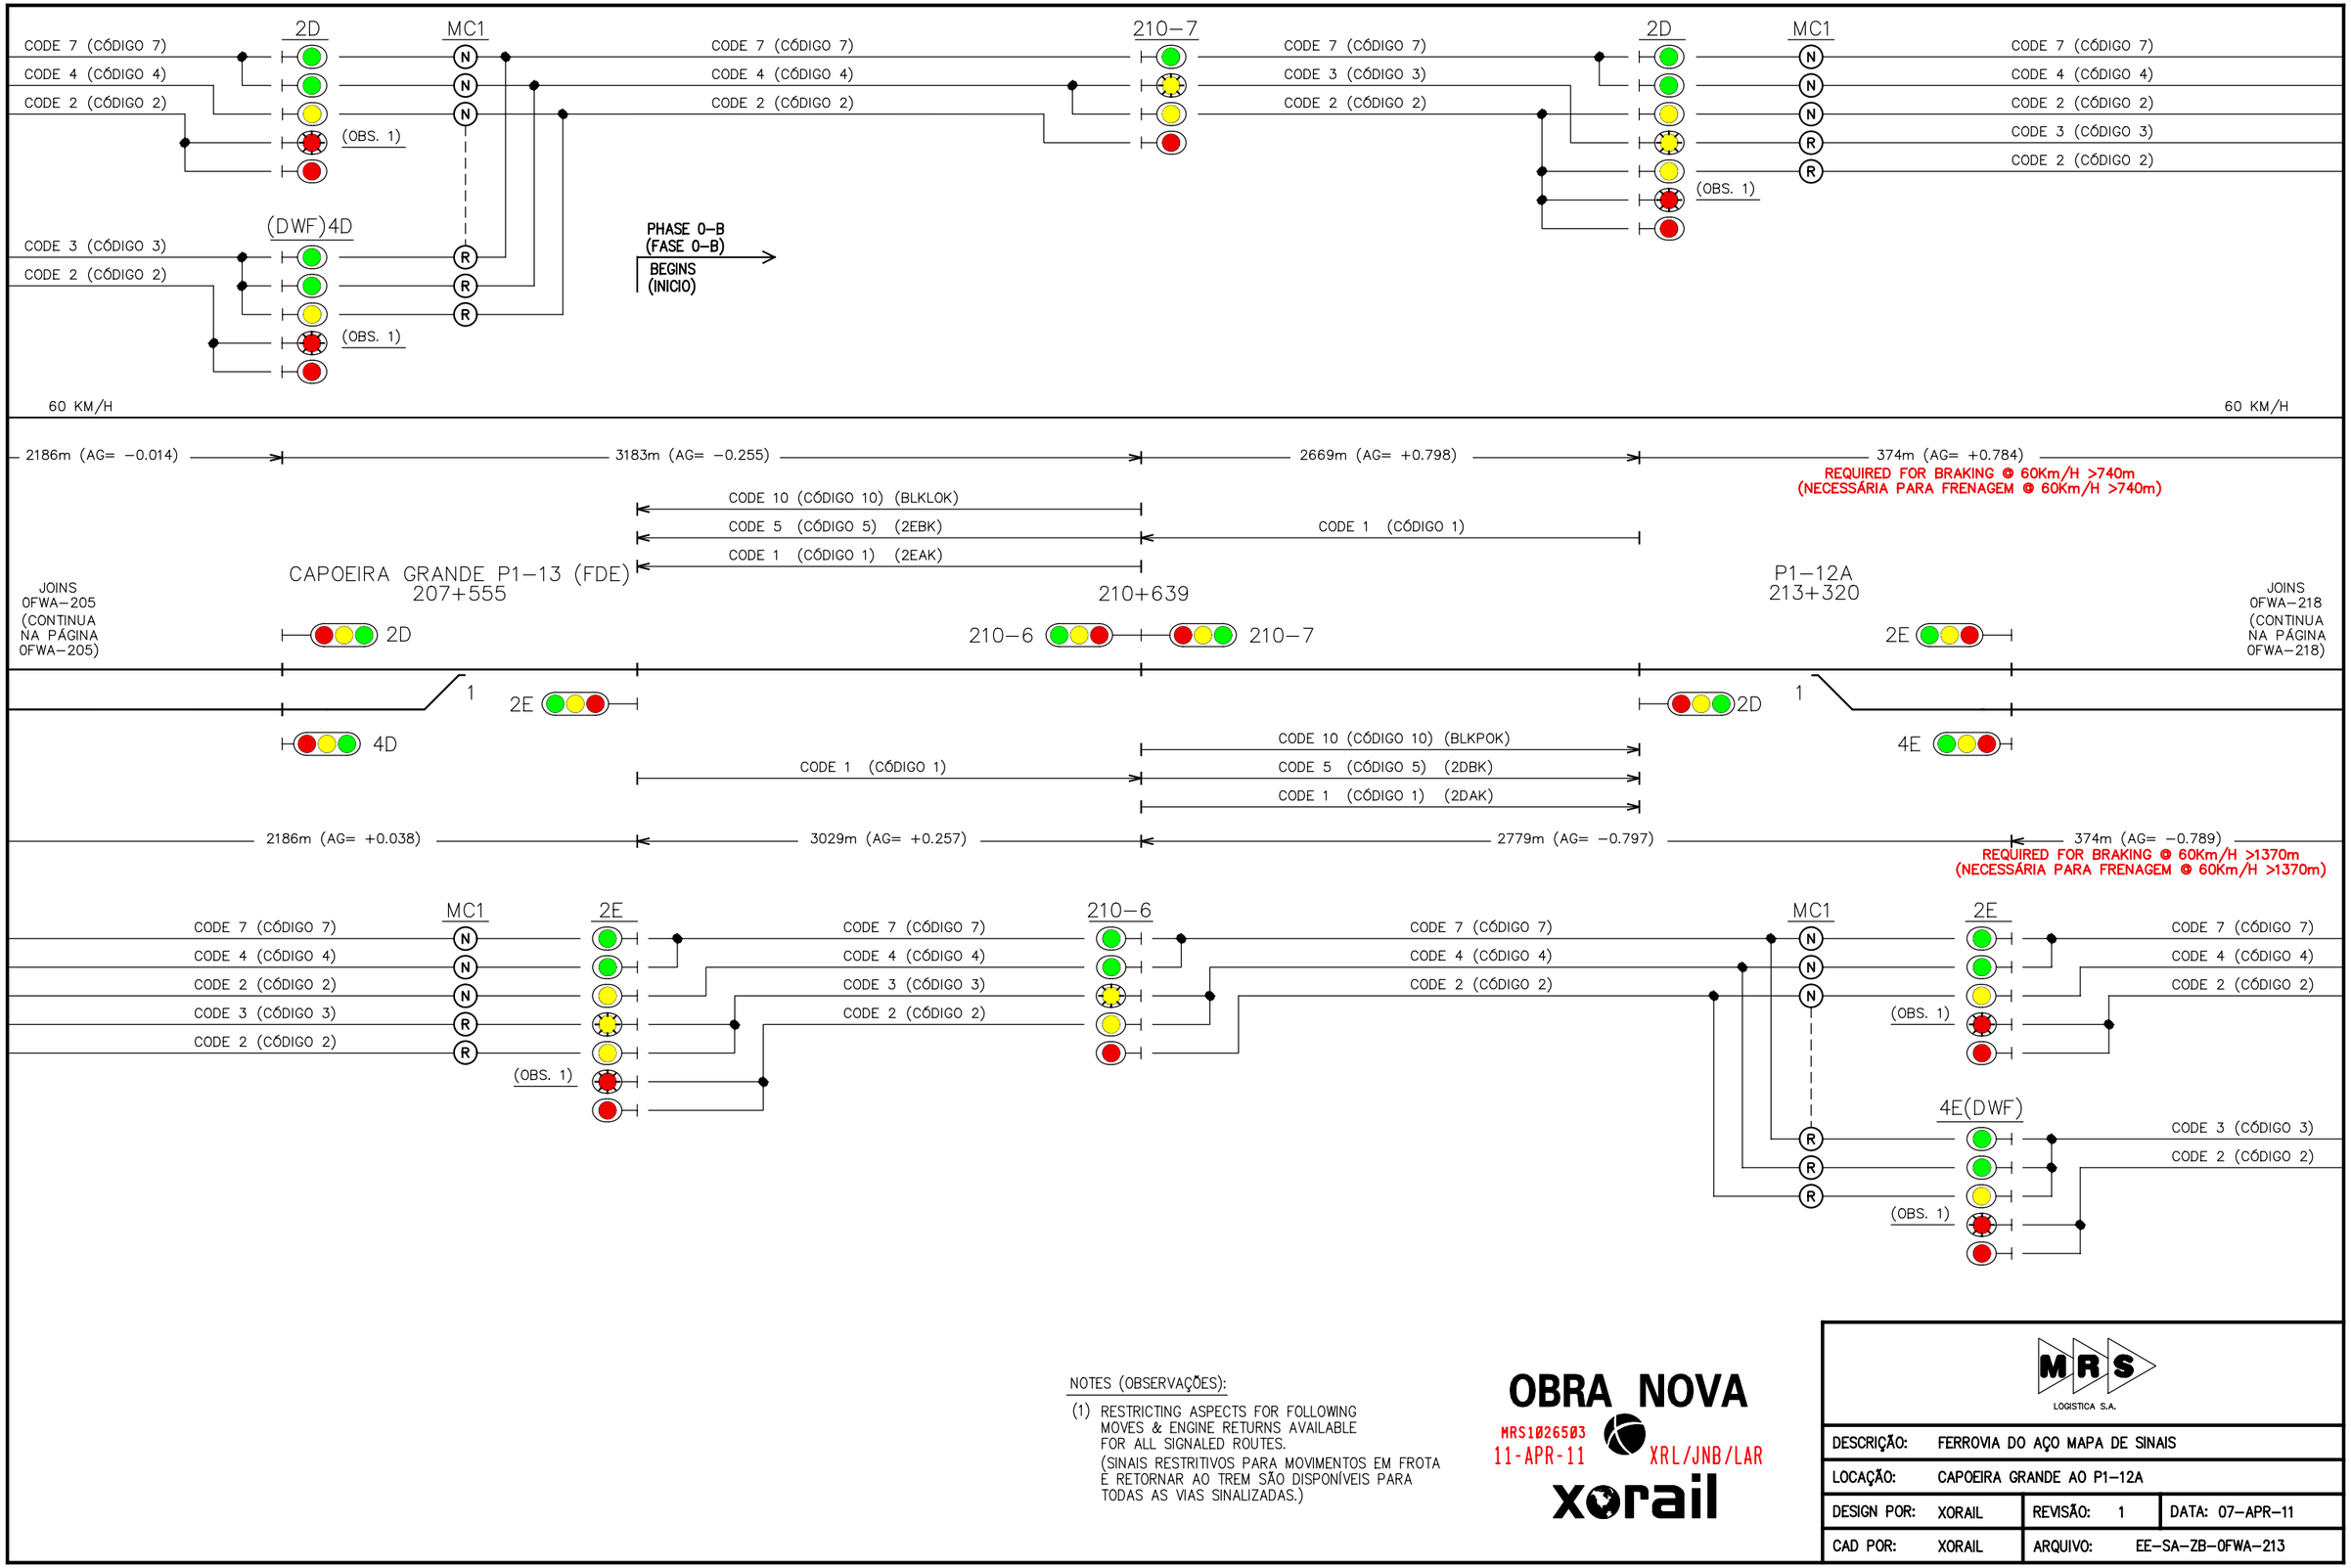

NOTES (OBSERVAÇÕES):

(1) RESTRICTING ASPECTS FOR FOLLOWING MOVES & ENGINE RETURNS AVAILABLE FOR ALL SIGNALED ROUTES.
(SINAIS RESTRITIVOS PARA MOVIMENTOS EM FROTA E RETORNAR AO TREM SÃO DISPONÍVEIS PARA TODAS AS VIAS SINALIZADAS.)


OBRA NOVA

MRS1026503
11-APR-11 XRL/JNB/LAR

xorail

MRS LOGISTICA S.A.

DESCRIÇÃO:	FERROVIA DO AÇO MAPA DE SINAIS		
LOCAÇÃO:	CAPOEIRA GRANDE AO P1-12A		
DESIGN POR:	XORAIL	REVISÃO: 1	DATA: 07-APR-11
CAD POR:	XORAIL	ARQUIVO:	EE-SA-ZB-0FWA-213

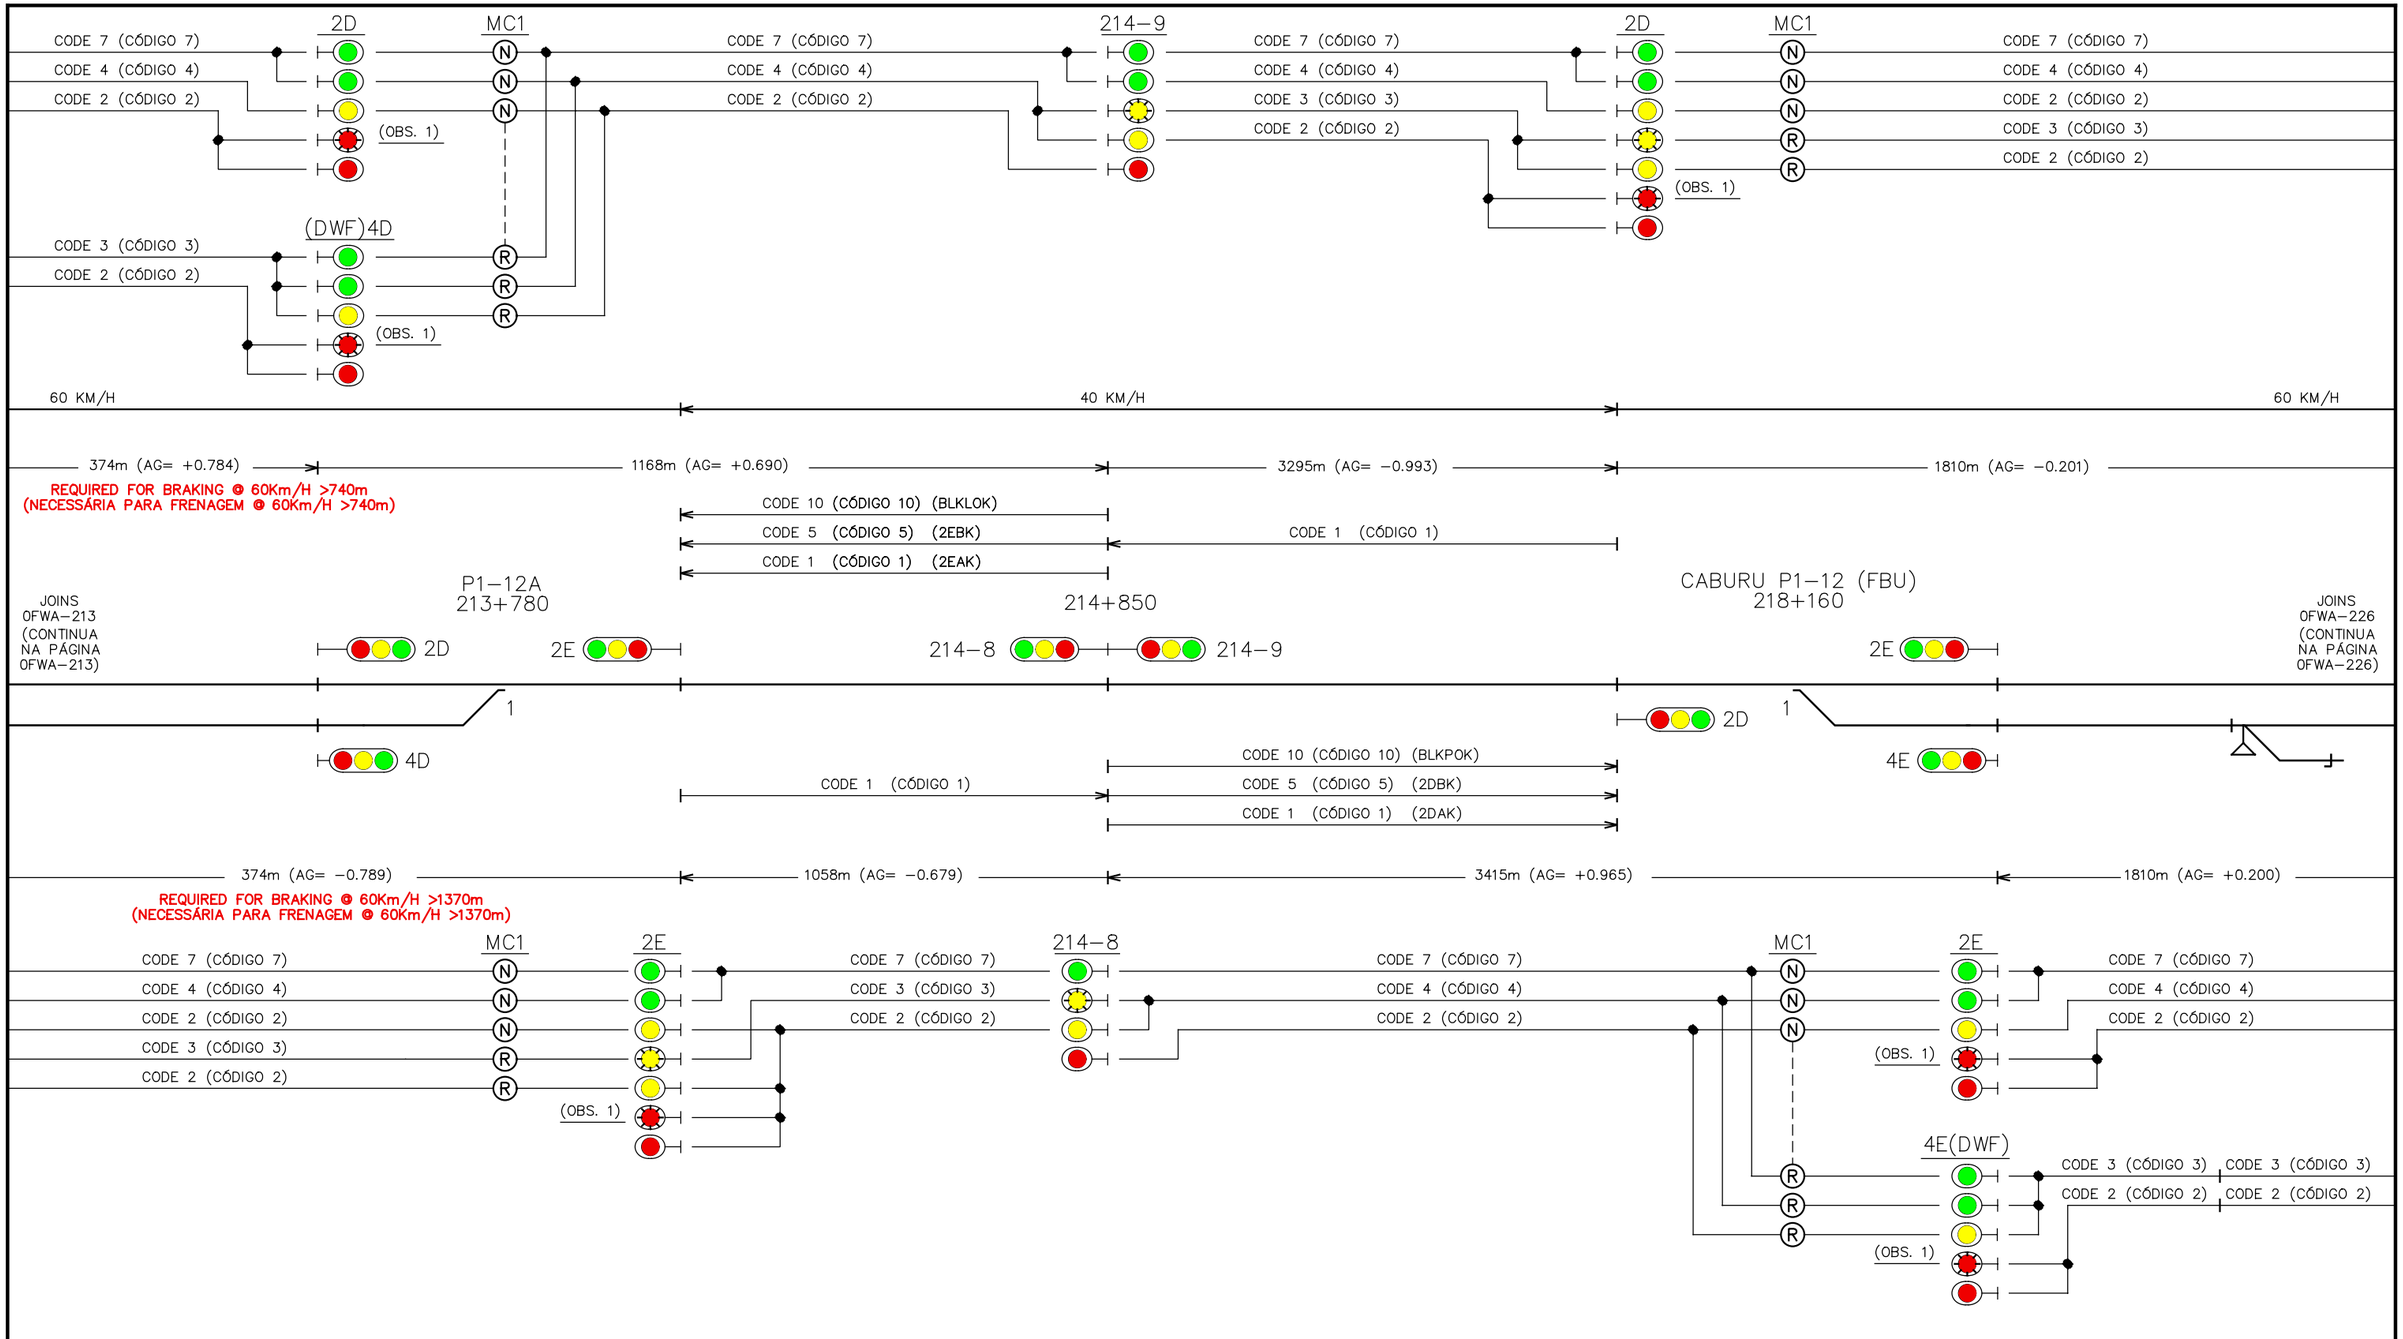

NOTES (OBSERVAÇÕES):

(1) RESTRICTING ASPECTS FOR FOLLOWING MOVES & ENGINE RETURNS AVAILABLE FOR ALL SIGNALED ROUTES.
(SINAIS RESTRITIVOS PARA MOVIMENTOS EM FROTA E RETORNAR AO TREM SÃO DISPONÍVEIS PARA TODAS AS VIAS SINALIZADAS.)


OBRA NOVA

MRS1026503
11-APR-11 XRL/JNB/LAR

xorail

MRS LOGISTICA S.A.

DESCRIÇÃO:	FERROVIA DO AÇO MAPA DE SINAIS		
LOCAÇÃO:	P1–12A AO CABURU		
DESIGN POR: XORAIL	REVISÃO: 1	DATA: 07–APR–11	
CAD POR: XORAIL	ARQUIVO: EE–SA–ZB–0FWA–218		

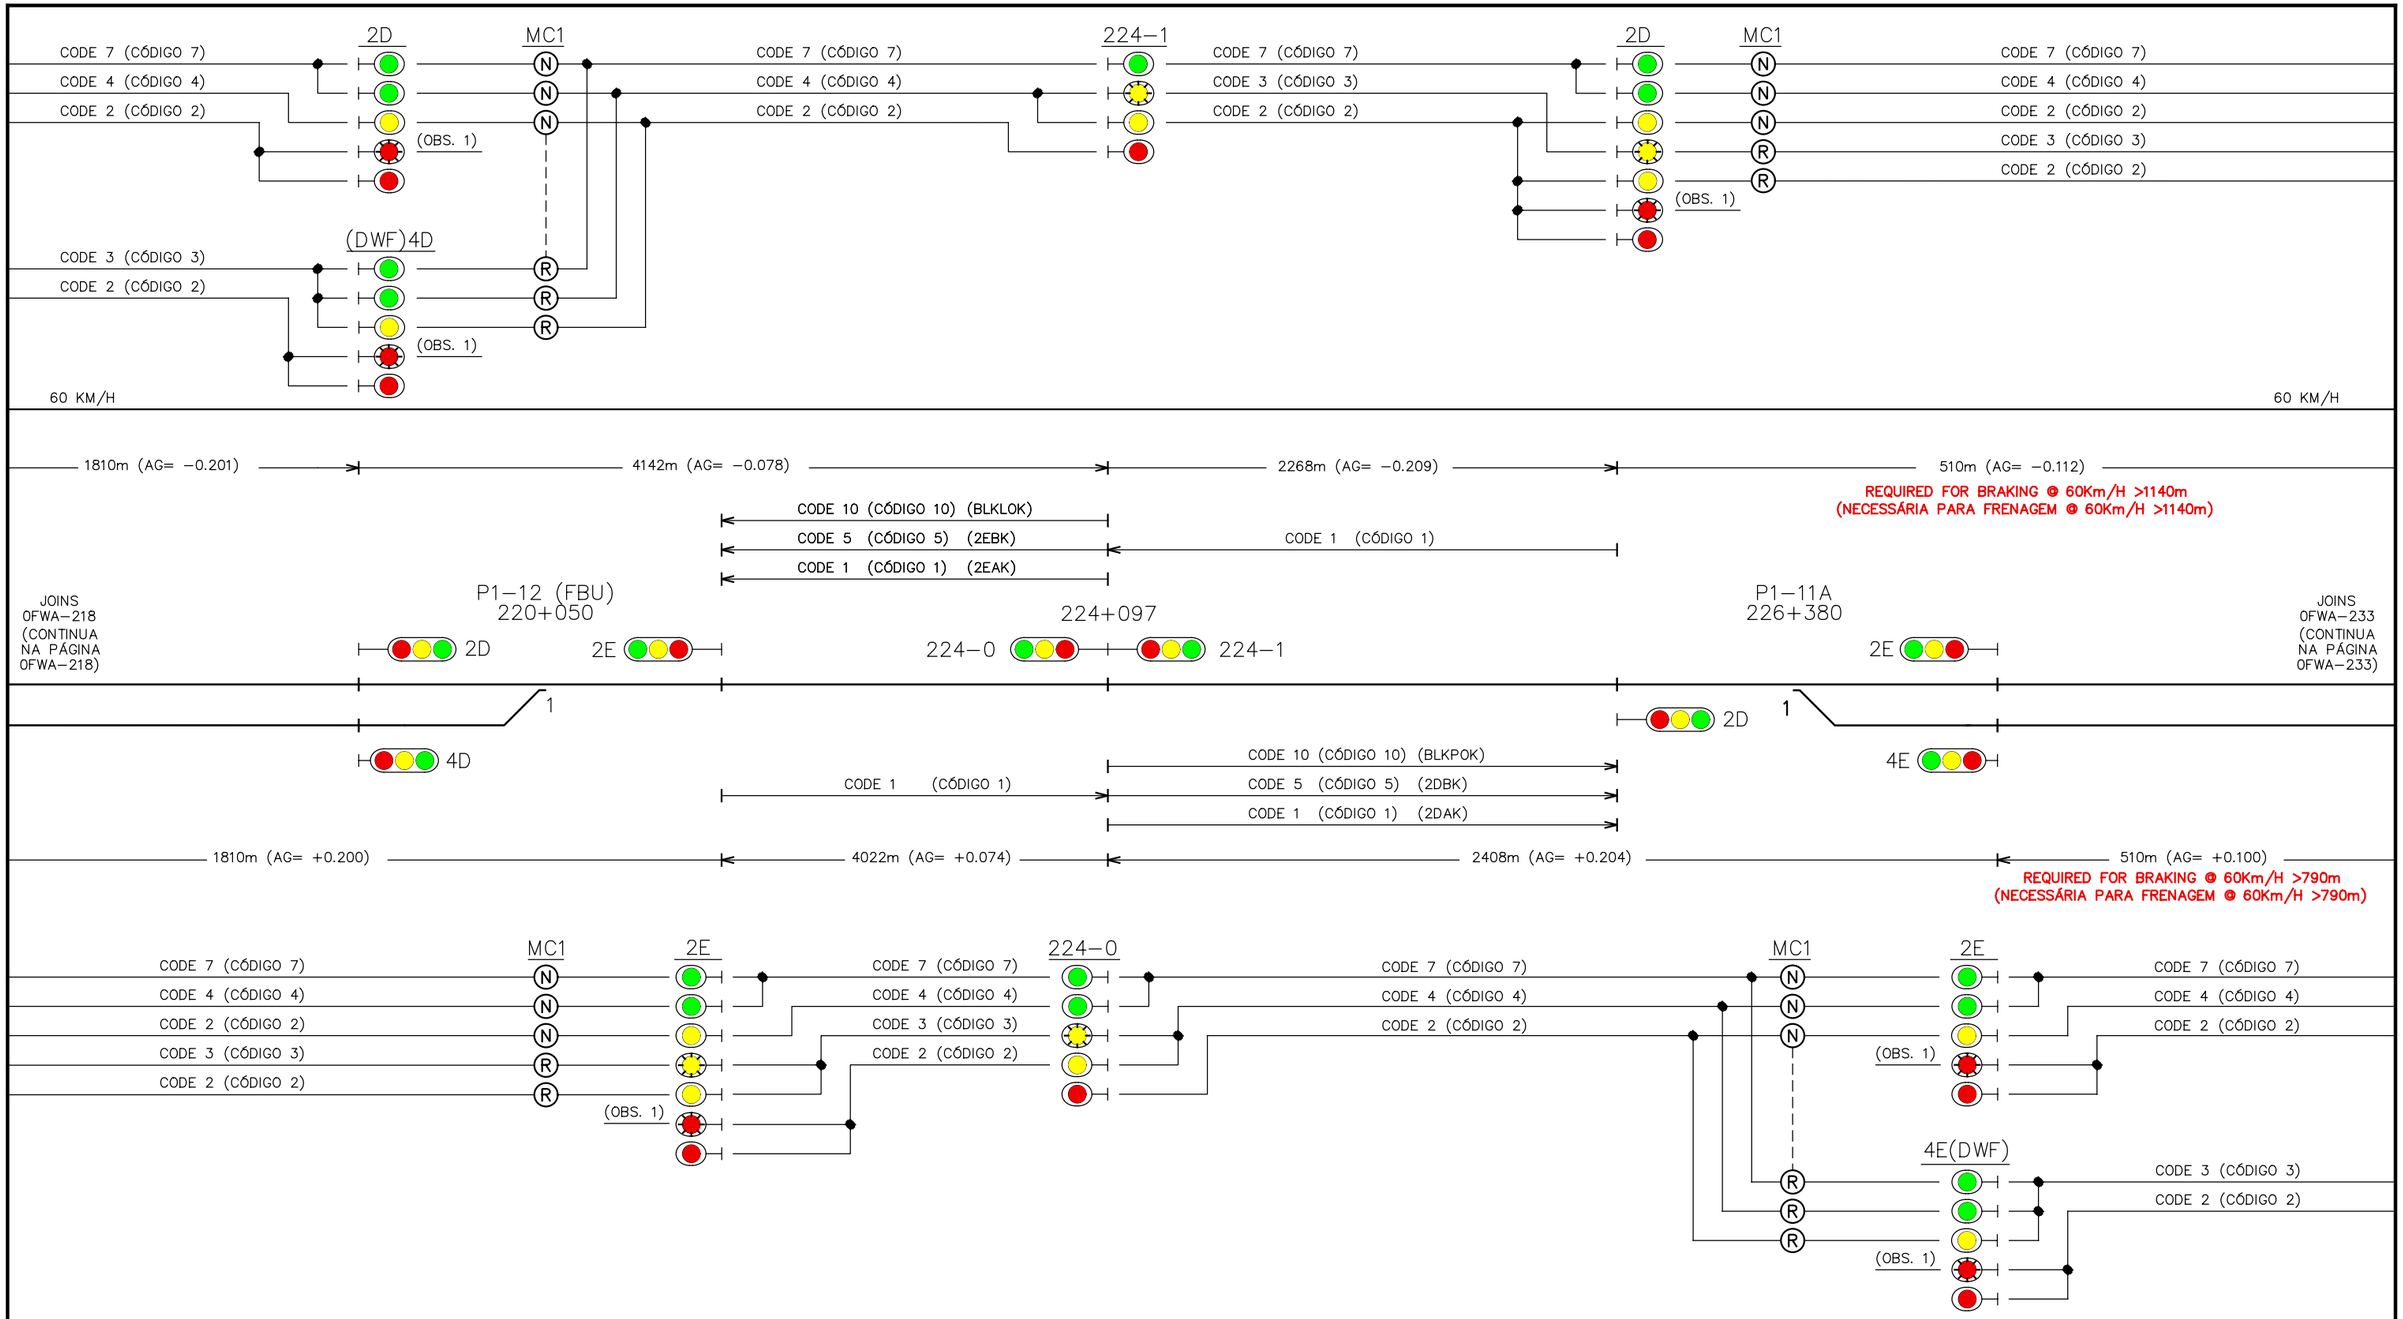

NOTES (OBSERVAÇÕES):

(1) RESTRICTING ASPECTS FOR FOLLOWING MOVES & ENGINE RETURNS AVAILABLE FOR ALL SIGNALED ROUTES.
(SINAIS RESTRITIVOS PARA MOVIMENTOS EM FROTA E RETORNAR AO TREM SÃO DISPONÍVEIS PARA TODAS AS VIAS SINALIZADAS.)


OBRA NOVA

MRS1026503
11-APR-11 XRL/JNB/LAR

xorail

MRS LOGISTICA S.A.

DESCRIÇÃO:	FERROVIA DO AÇO MAPA DE SINAIS		
LOCAÇÃO:	CABURU AO P1–11A		
DESIGN POR:	XORAIL	REVISÃO: 1	DATA: 07–APR–11
CAD POR:	XORAIL	ARQUIVO:	EE–SA–ZB–0FWA–226

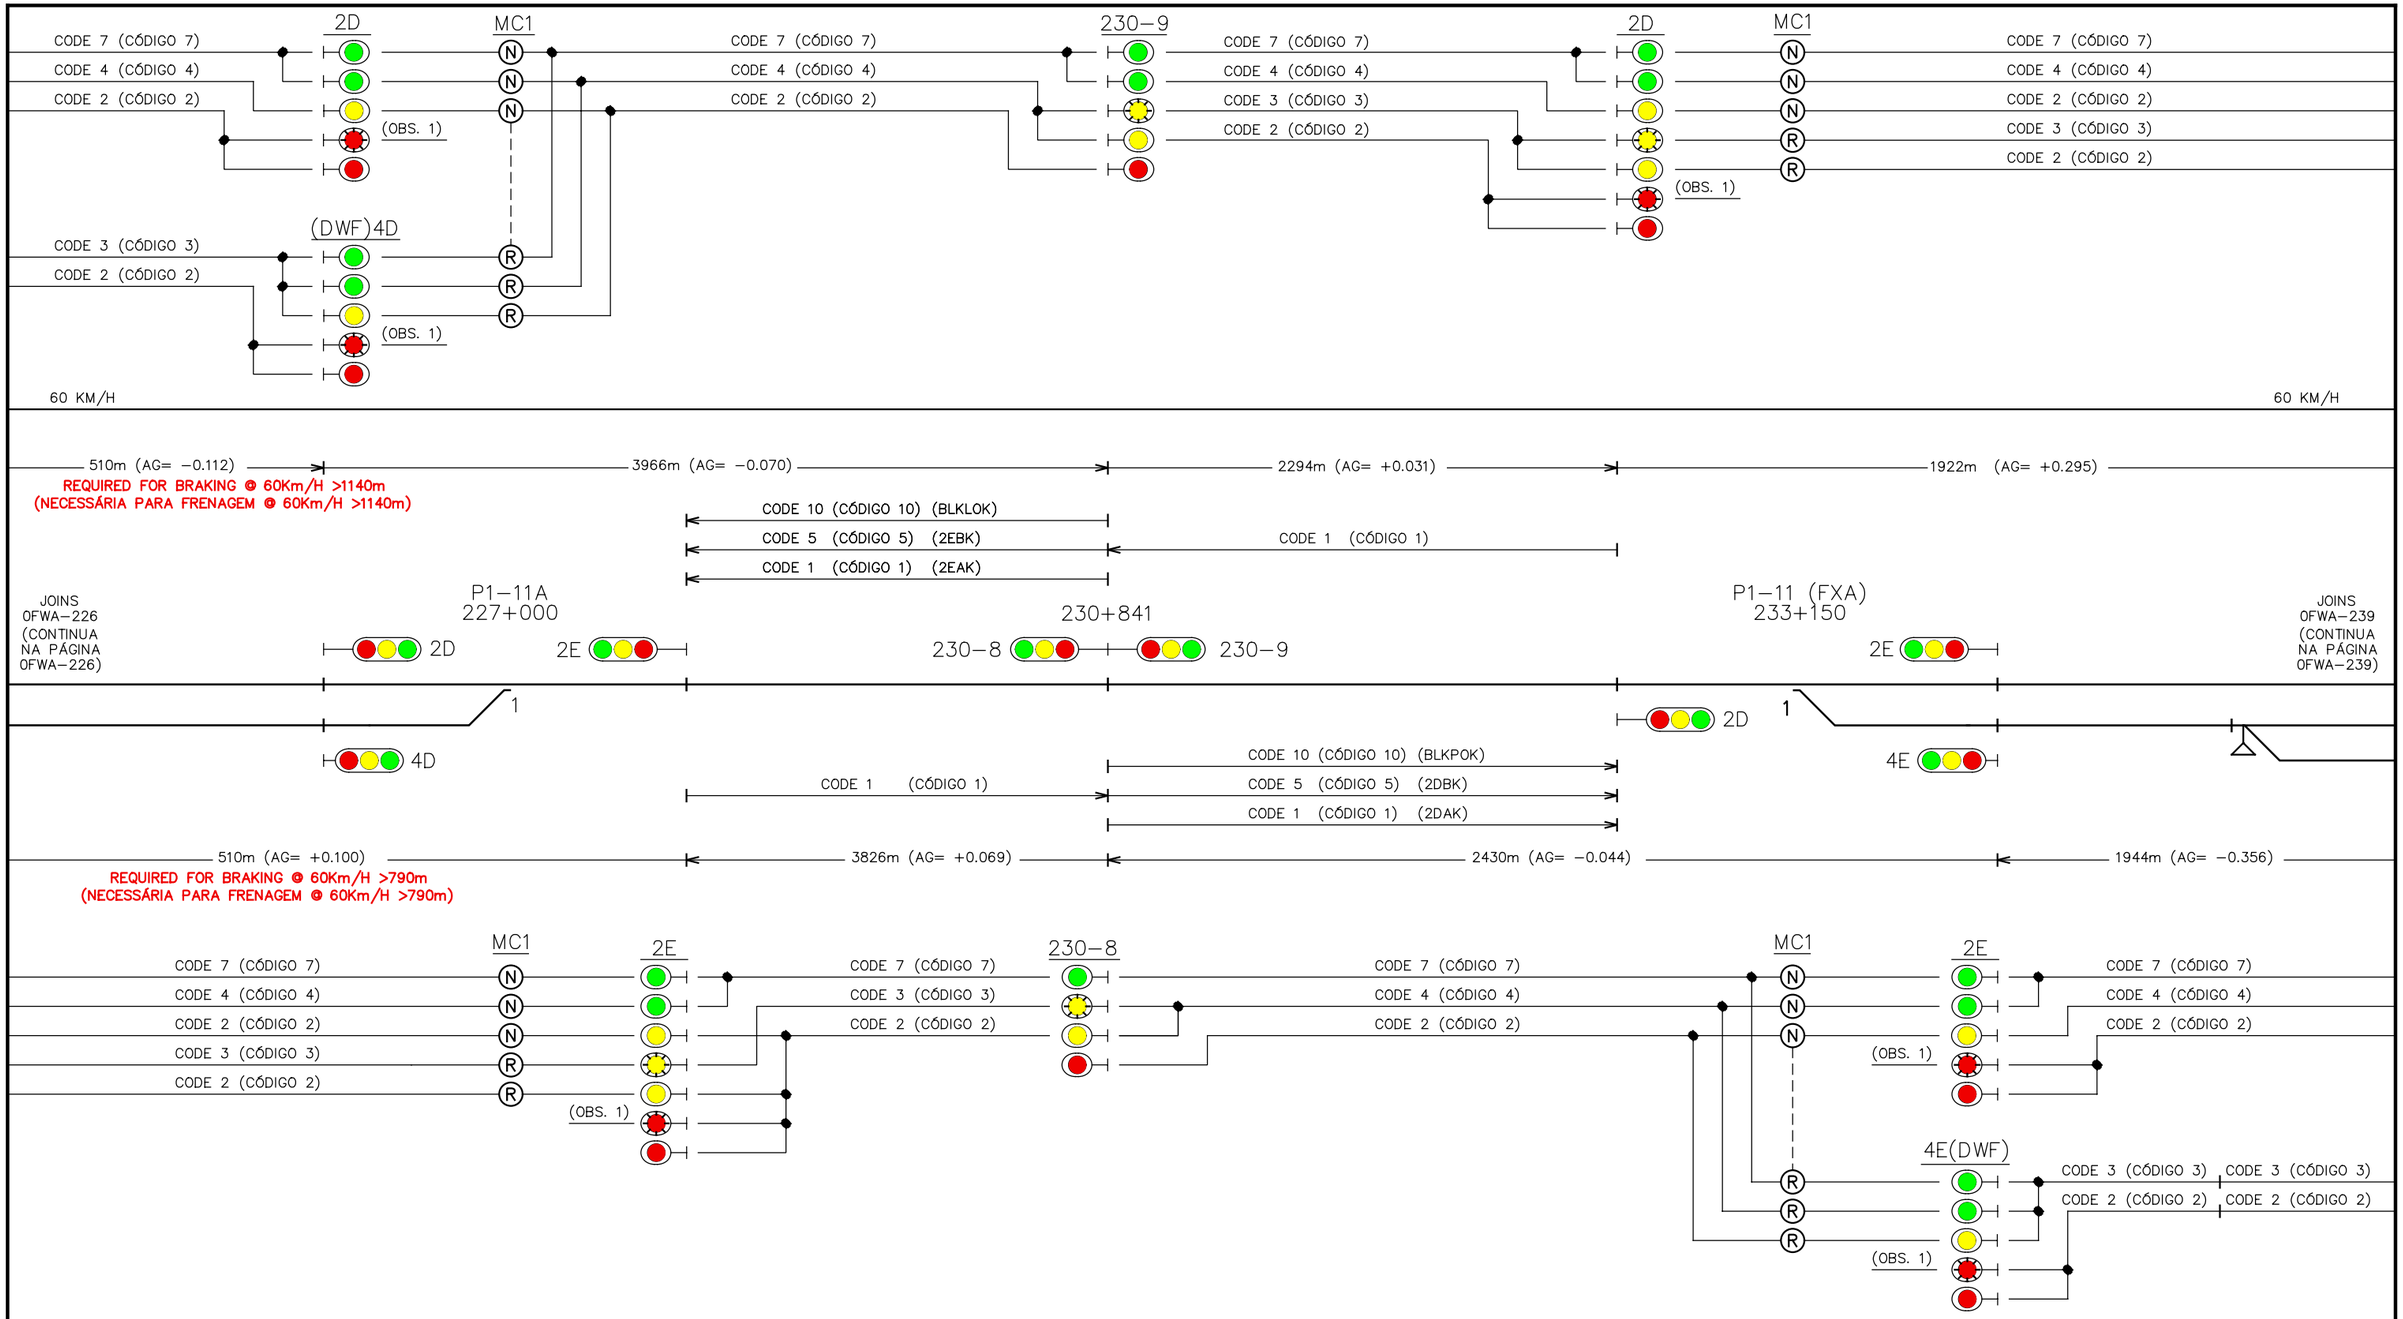

NOTES (OBSERVAÇÕES):

(1) RESTRICTING ASPECTS FOR FOLLOWING MOVES & ENGINE RETURNS AVAILABLE FOR ALL SIGNALED ROUTES.
(SINAIS RESTRITIVOS PARA MOVIMENTOS EM FROTA E RETORNAR AO TREM SÃO DISPONÍVEIS PARA TODAS AS VIAS SINALIZADAS.)


OBRA NOVA

MRS1026503
11-APR-11 XRL/JNB/LAR

xorail

MRS LOGISTICA S.A.

DESCRIÇÃO:	FERROVIA DO AÇO MAPA DE SINAIS		
LOCAÇÃO:	P1–11A AO XAVIER CHAVES		
DESIGN POR: XORAIL	REVISÃO: 1	DATA: 07–APR–11	
CAD POR: XORAIL	ARQUIVO: EE–SA–ZB–0FWA–233		

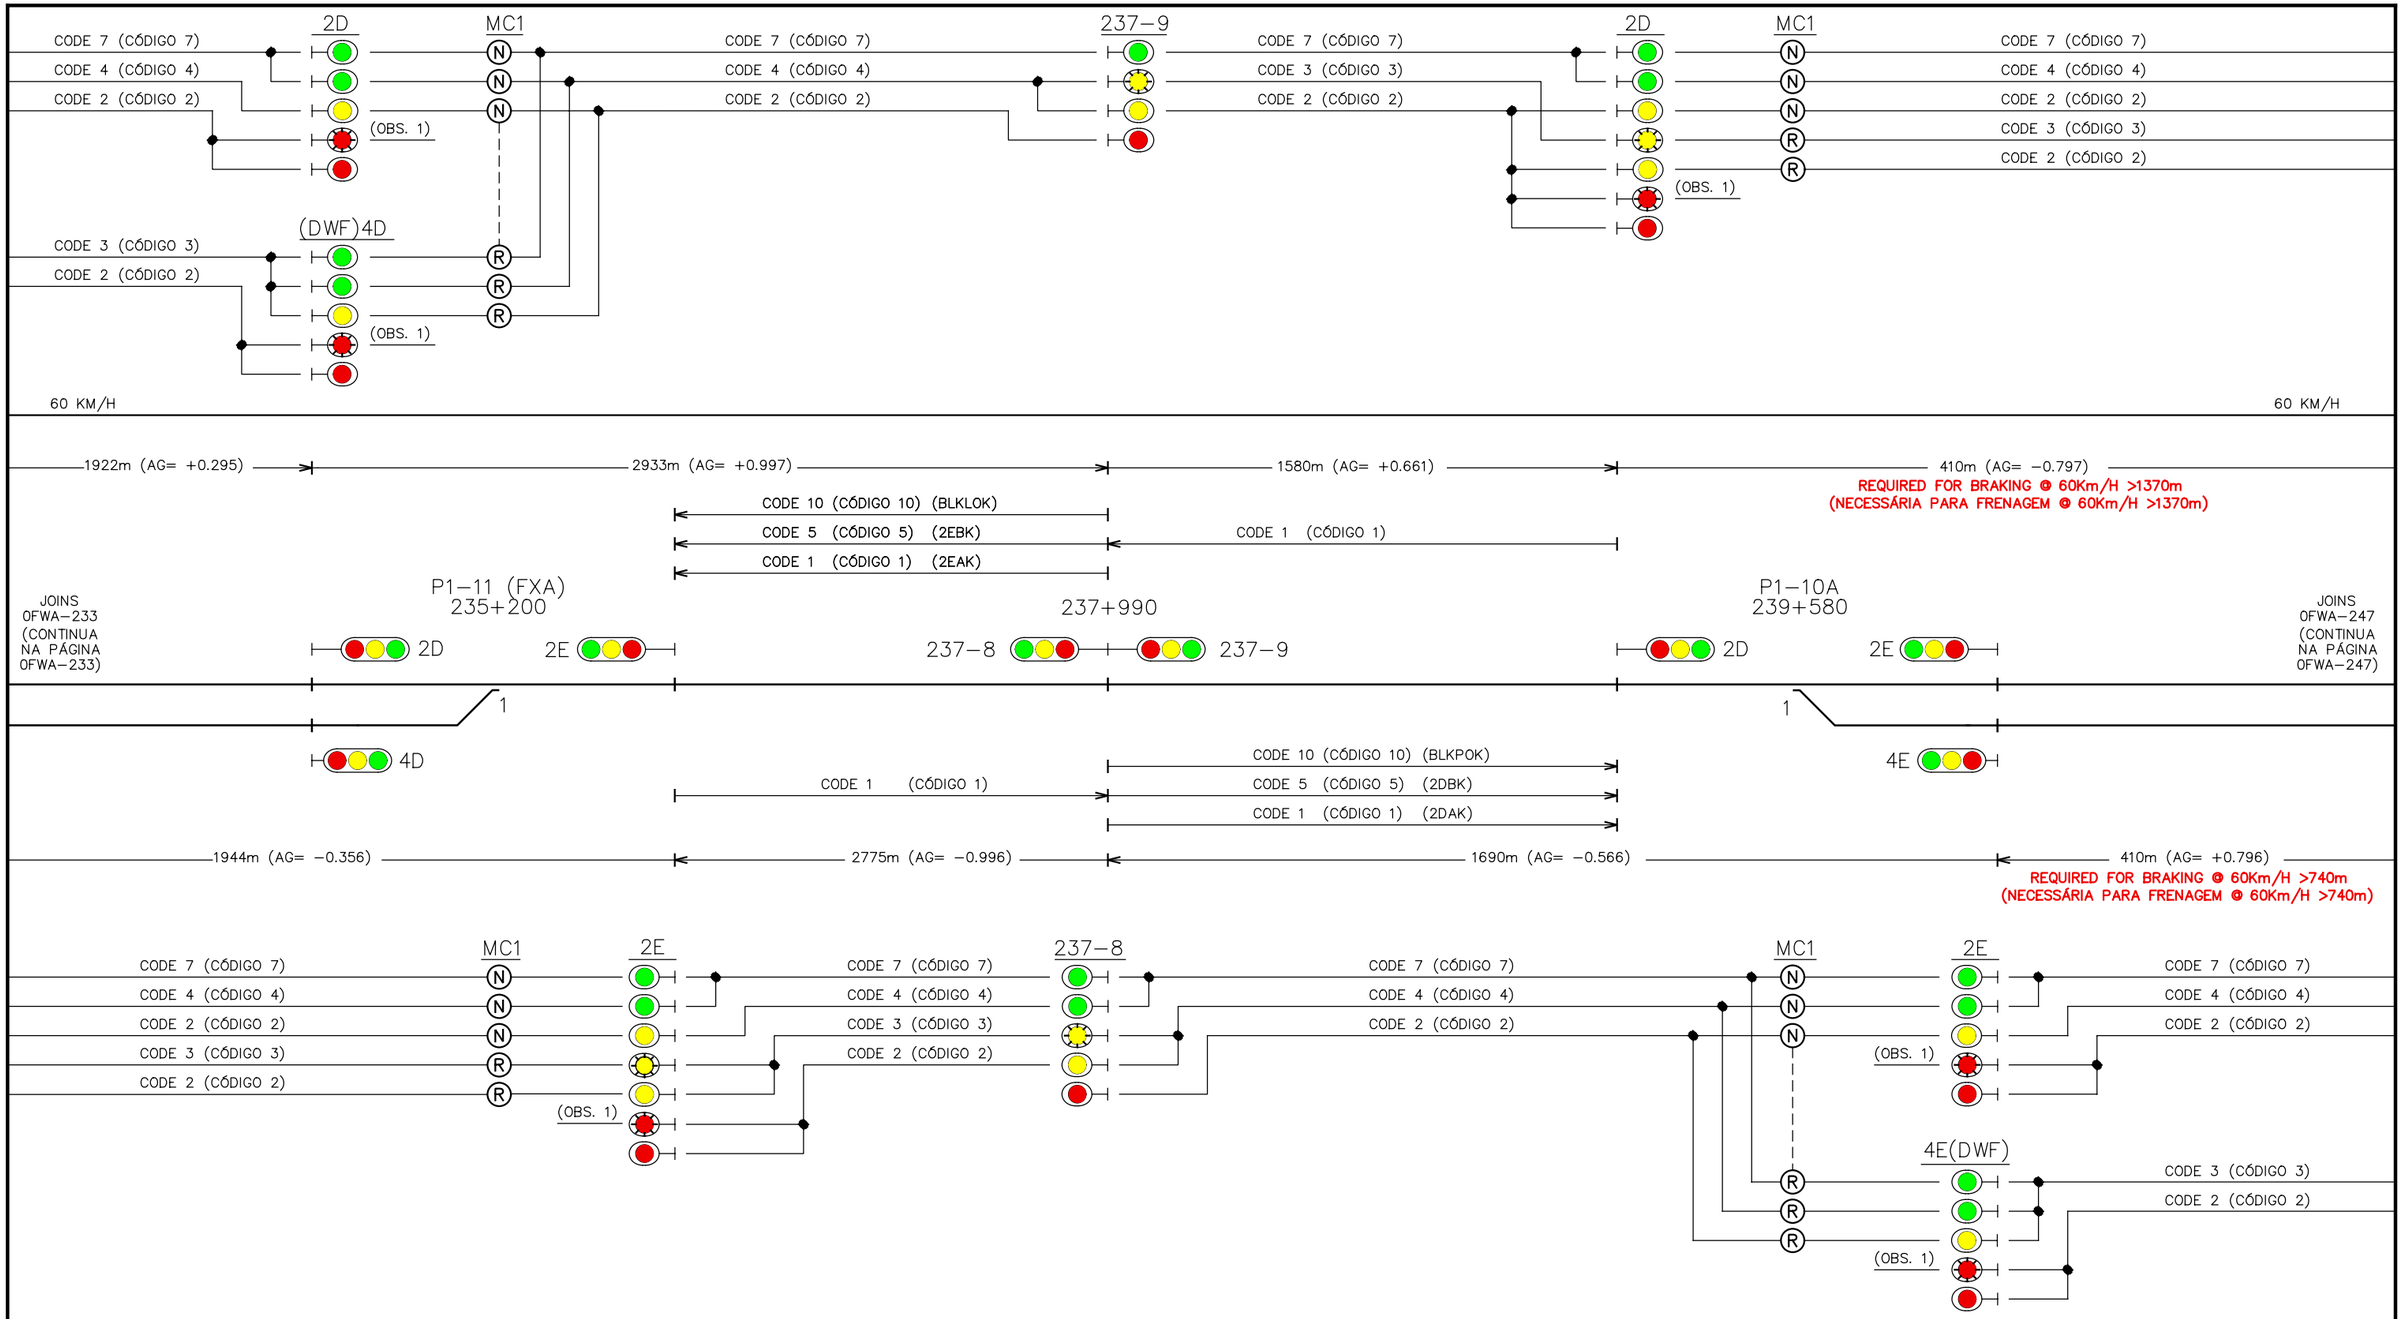

NOTES (OBSERVAÇÕES):

(1) RESTRICTING ASPECTS FOR FOLLOWING MOVES & ENGINE RETURNS AVAILABLE FOR ALL SIGNALED ROUTES.
(SINAIS RESTRITIVOS PARA MOVIMENTOS EM FROTA E RETORNAR AO TREM SÃO DISPONÍVEIS PARA TODAS AS VIAS SINALIZADAS.)


OBRA NOVA

MRS1026503
11-APR-11 XRL/JNB/LAR

xorail

MRS LOGISTICA S.A.

DESCRIÇÃO:	FERROVIA DO AÇO MAPA DE SINAIS		
LOCAÇÃO:	XAVIER CHAVES AO P1–10A		
DESIGN POR: XORAIL	REVISÃO: 1	DATA: 07–APR–11	
CAD POR: XORAIL	ARQUIVO: EE–SA–ZB–0FWA–239		

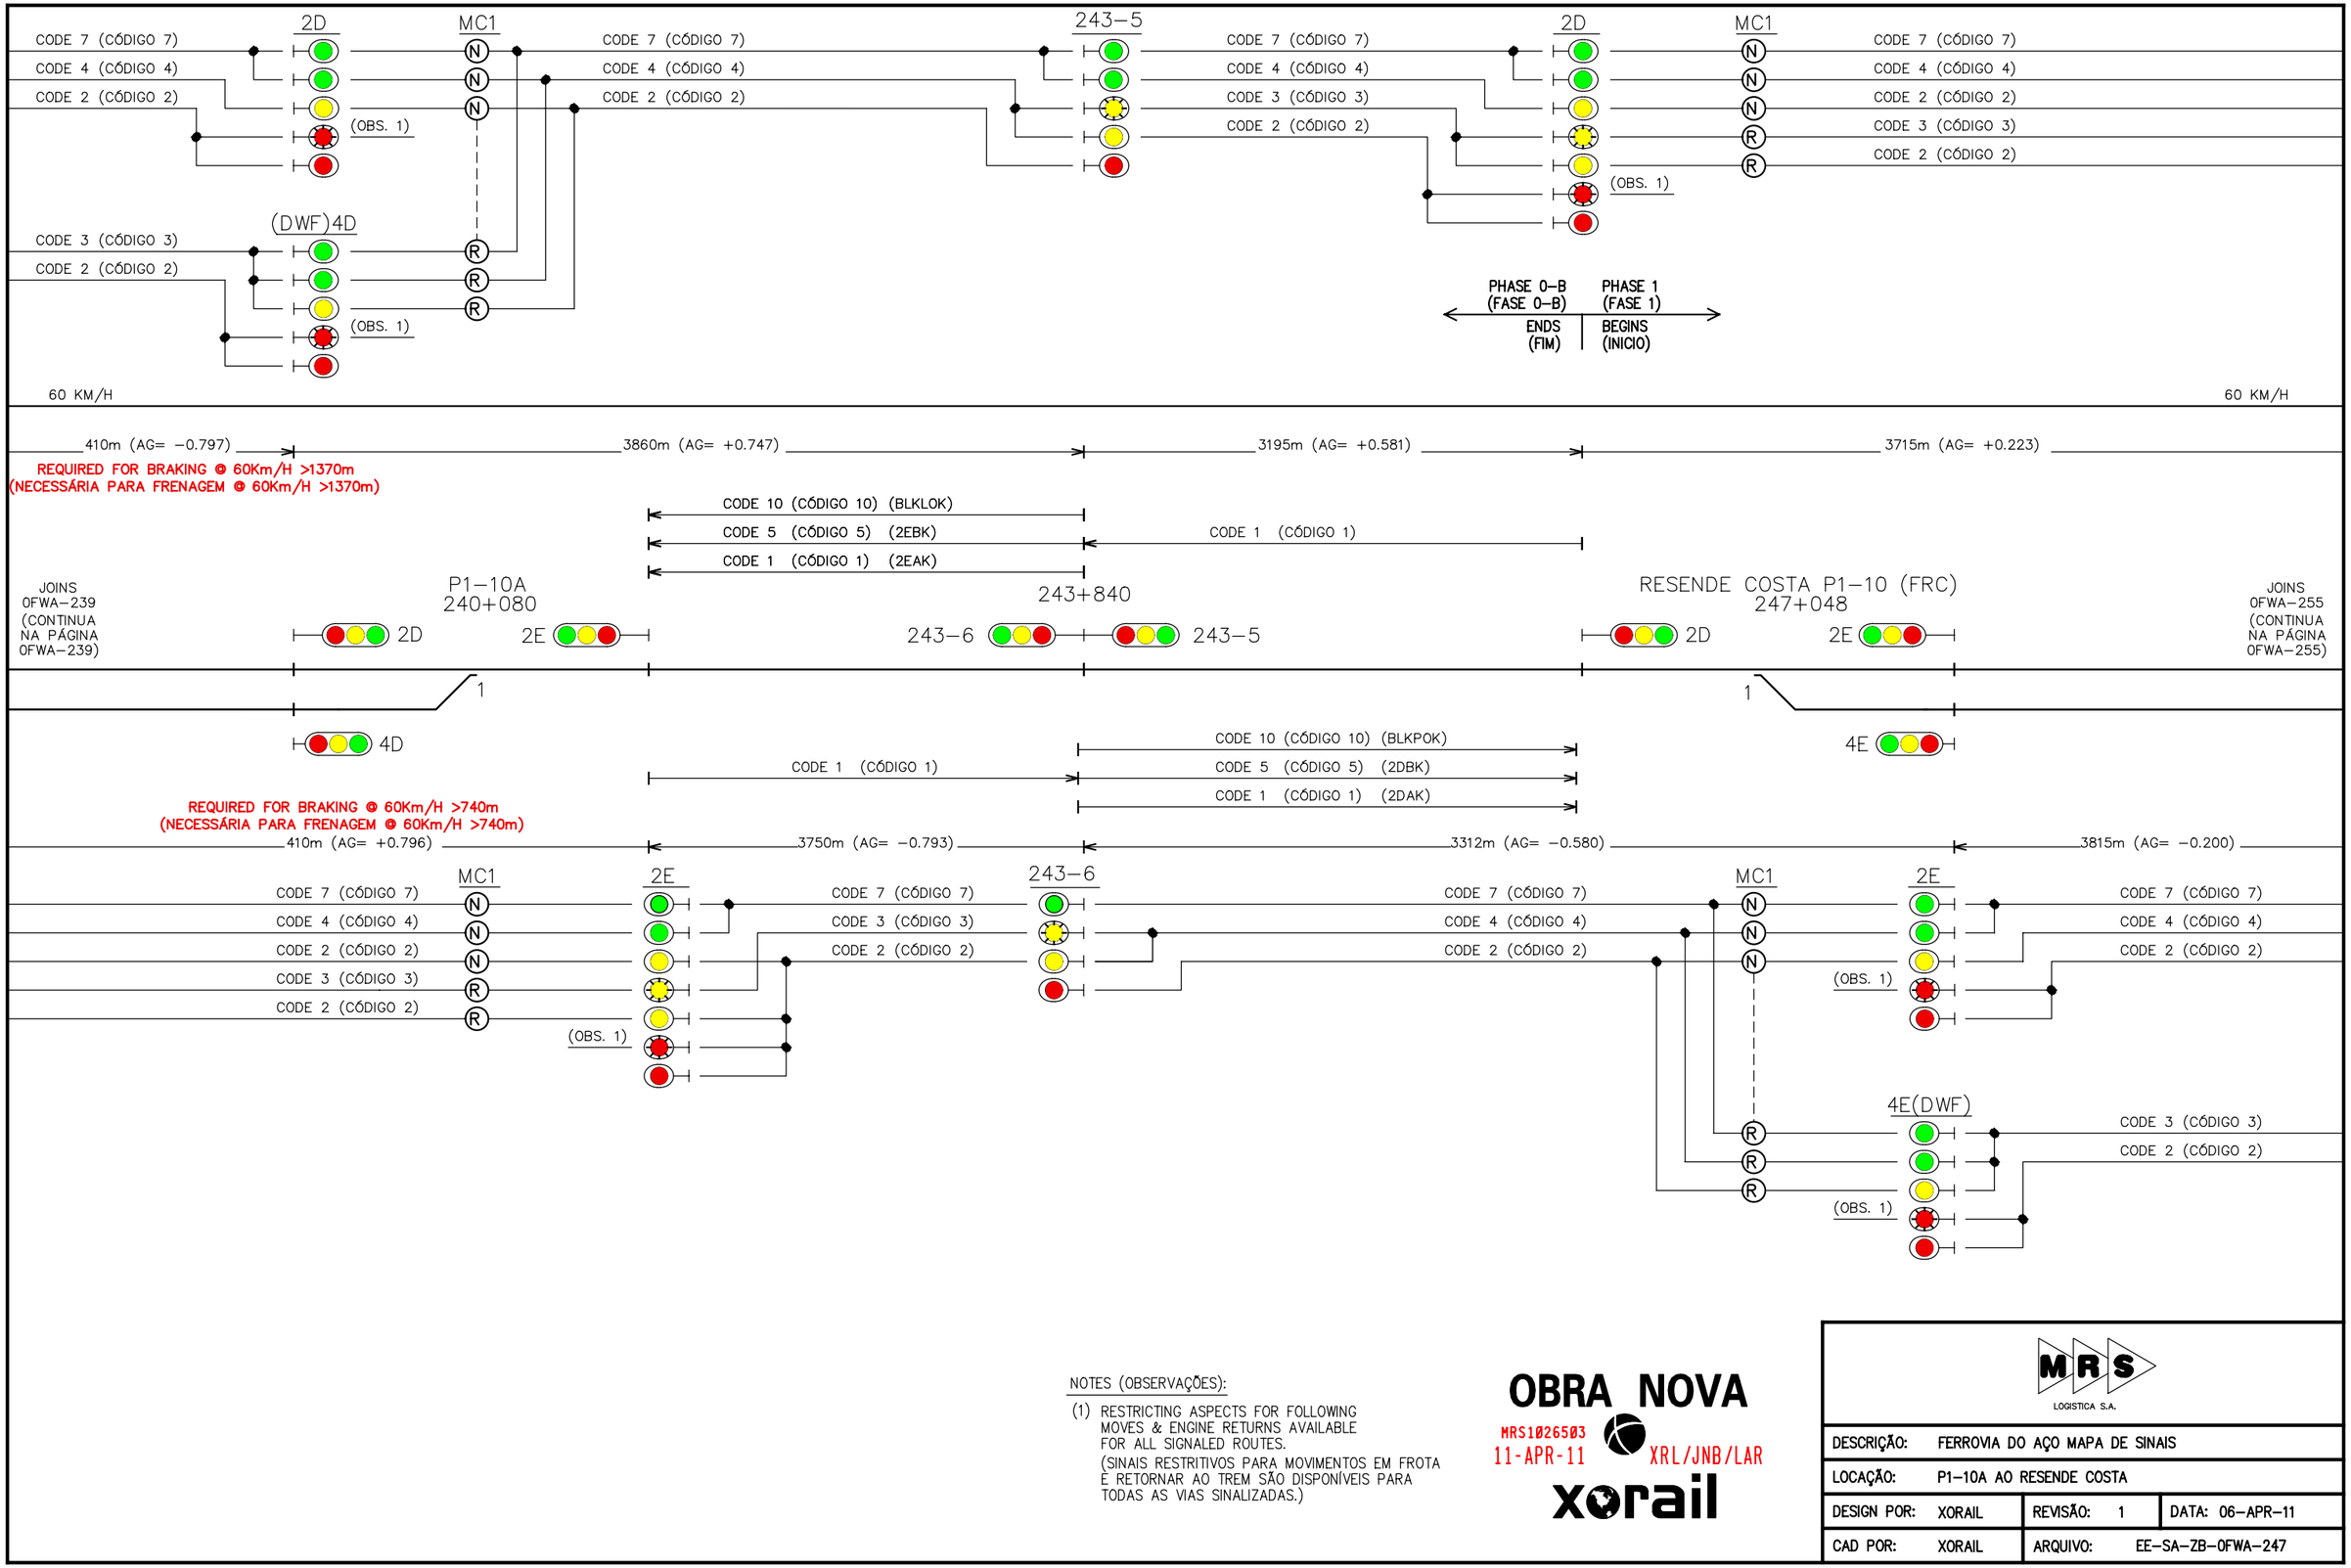

NOTES (OBSERVAÇÕES):

(1) RESTRICTING ASPECTS FOR FOLLOWING MOVES & ENGINE RETURNS AVAILABLE FOR ALL SIGNALED ROUTES.
(SINAIS RESTRITIVOS PARA MOVIMENTOS EM FROTA E RETORNAR AO TREM SÃO DISPONÍVEIS PARA TODAS AS VIAS SINALIZADAS.)

OBRA NOVA

MRS1026503
11-APR-11 XRL/JNB/LAR

xorail

MRS LOGISTICA S.A.

DESCRIÇÃO:	FERROVIA DO AÇO MAPA DE SINAIS		
LOCAÇÃO:	P1–10A AO RESENDE COSTA		
DESIGN POR: XORAIL	REVISÃO: 1	DATA: 06–APR–11	
CAD POR: XORAIL	ARQUIVO: EE–SA–ZB–0FWA–247		